




Traggerüste für Montage Fertigteile, Längsschnitt M 1:50

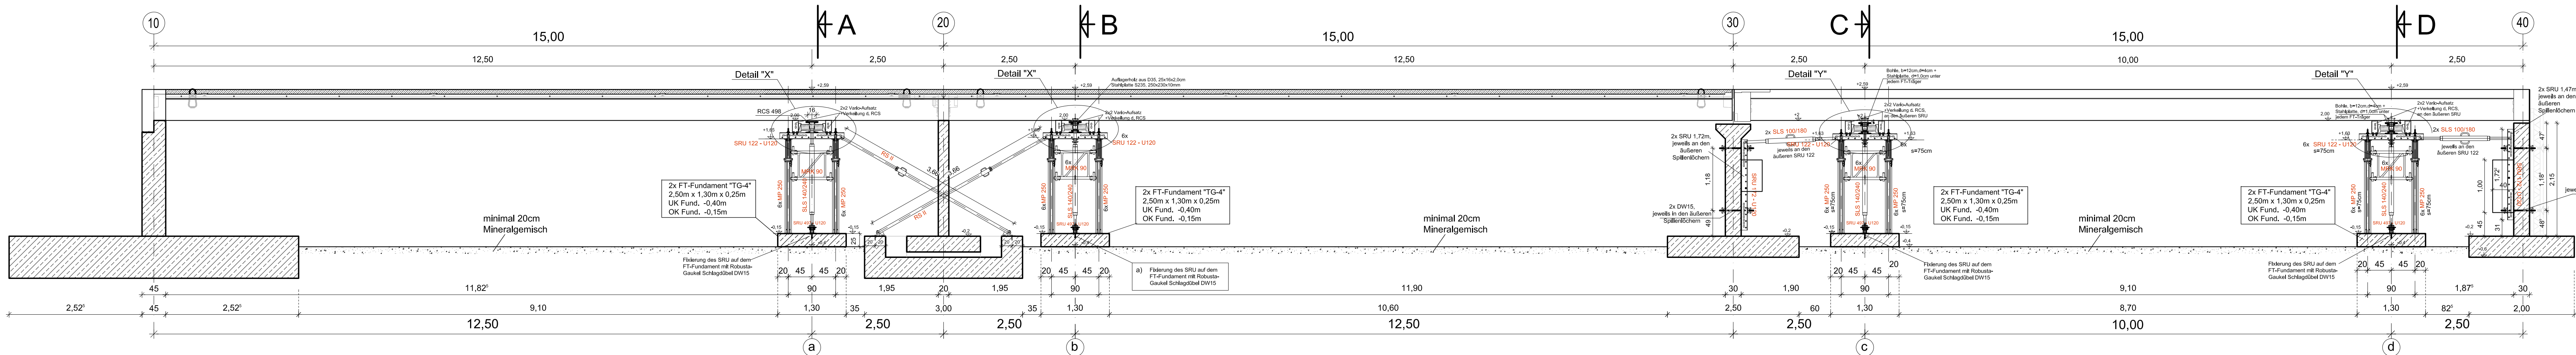


Traggerüst für Montage Fertigteile, Joch "a", Schnitt "A", M 1:25

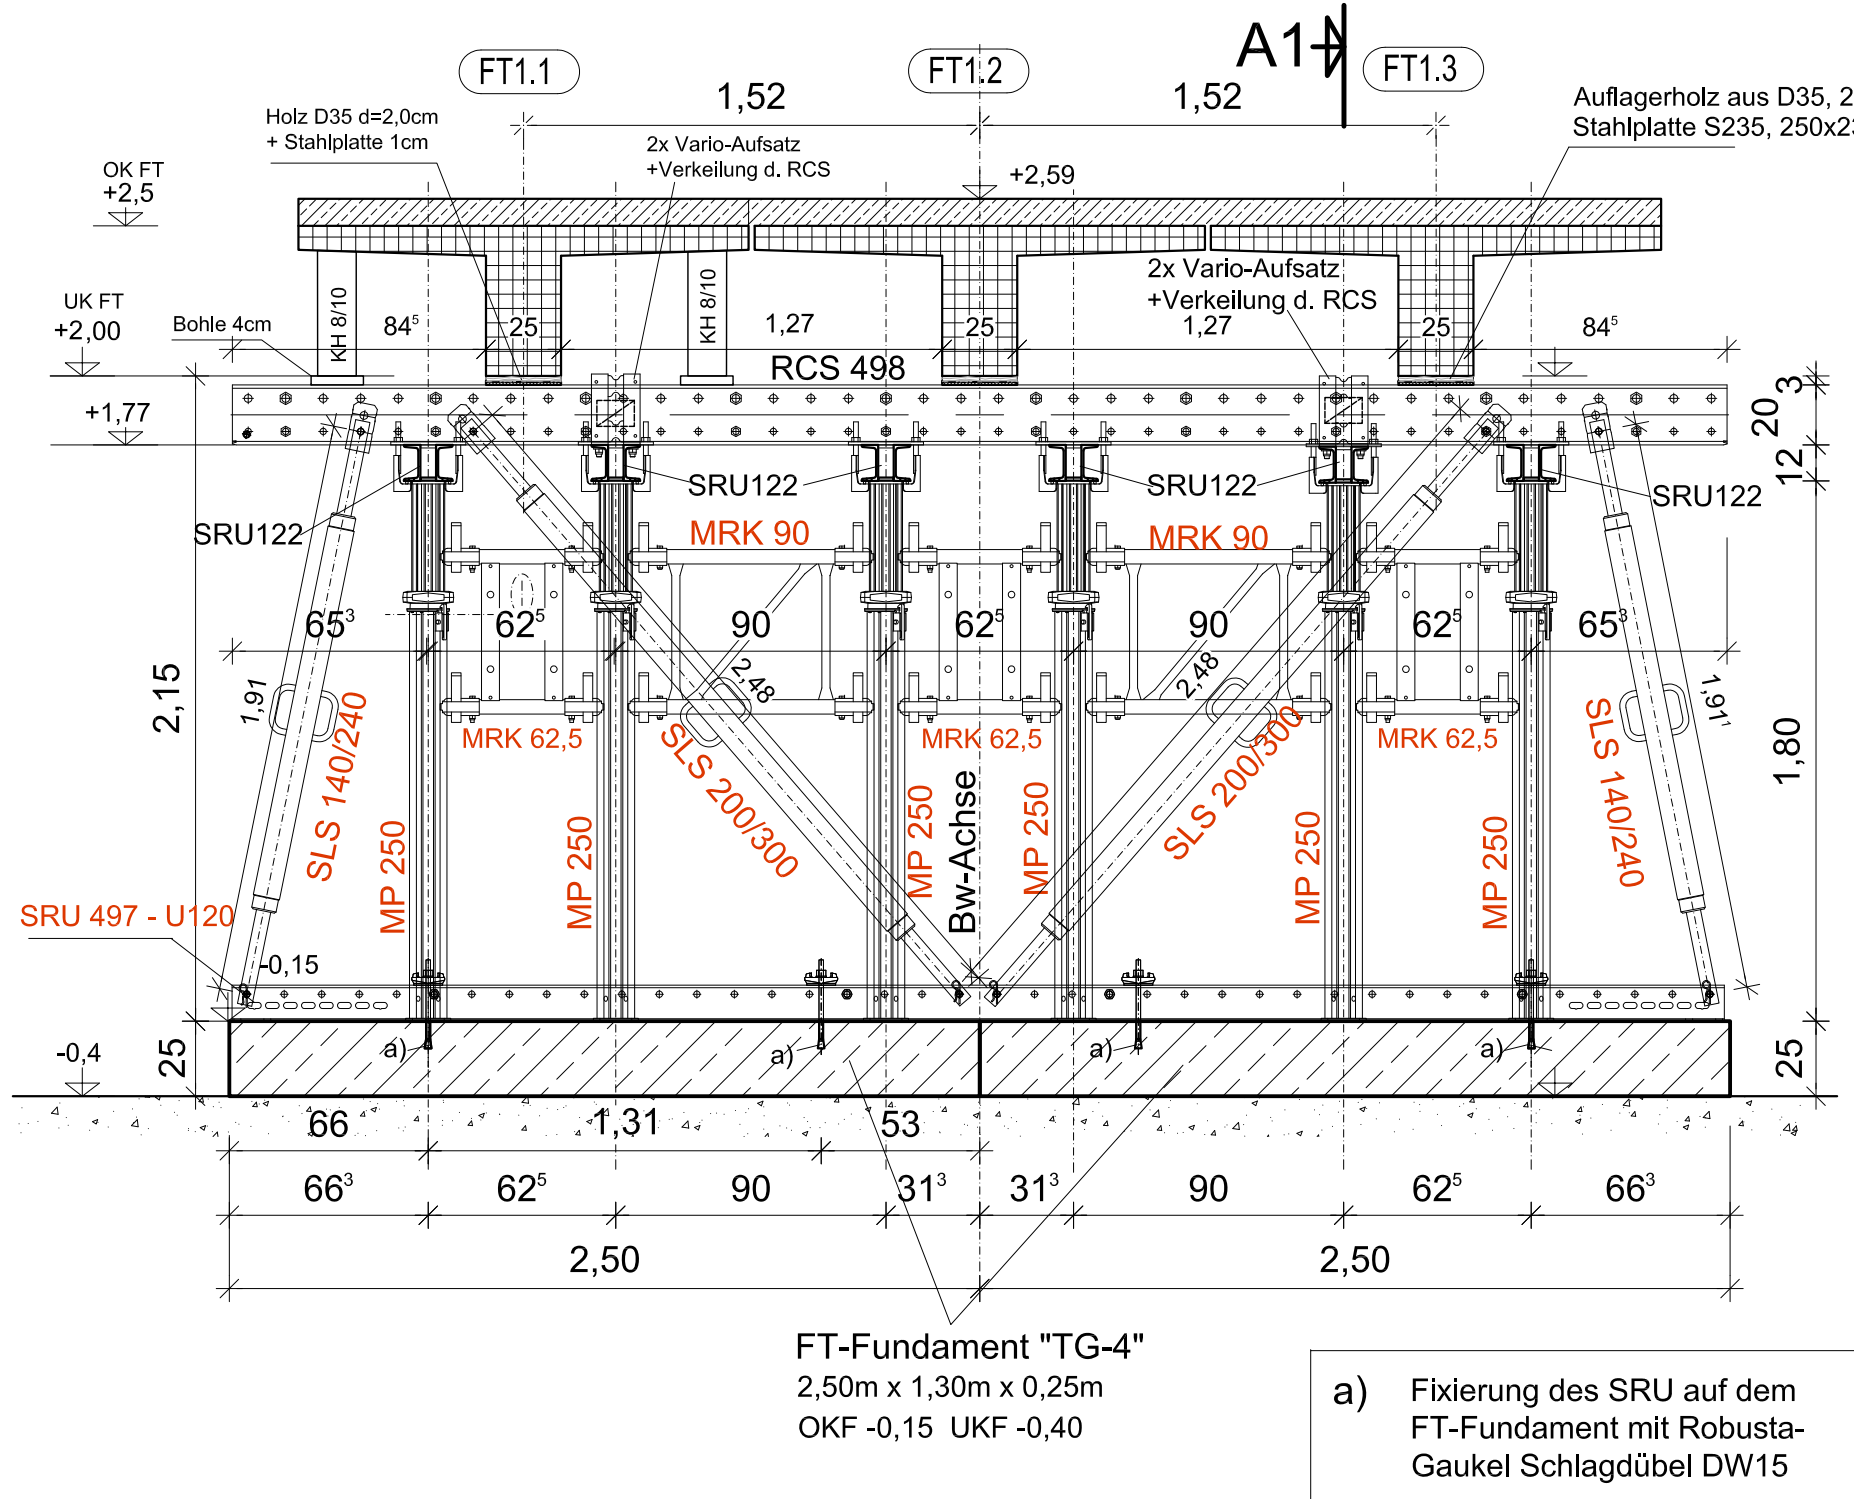


Teilschnitt "A1"

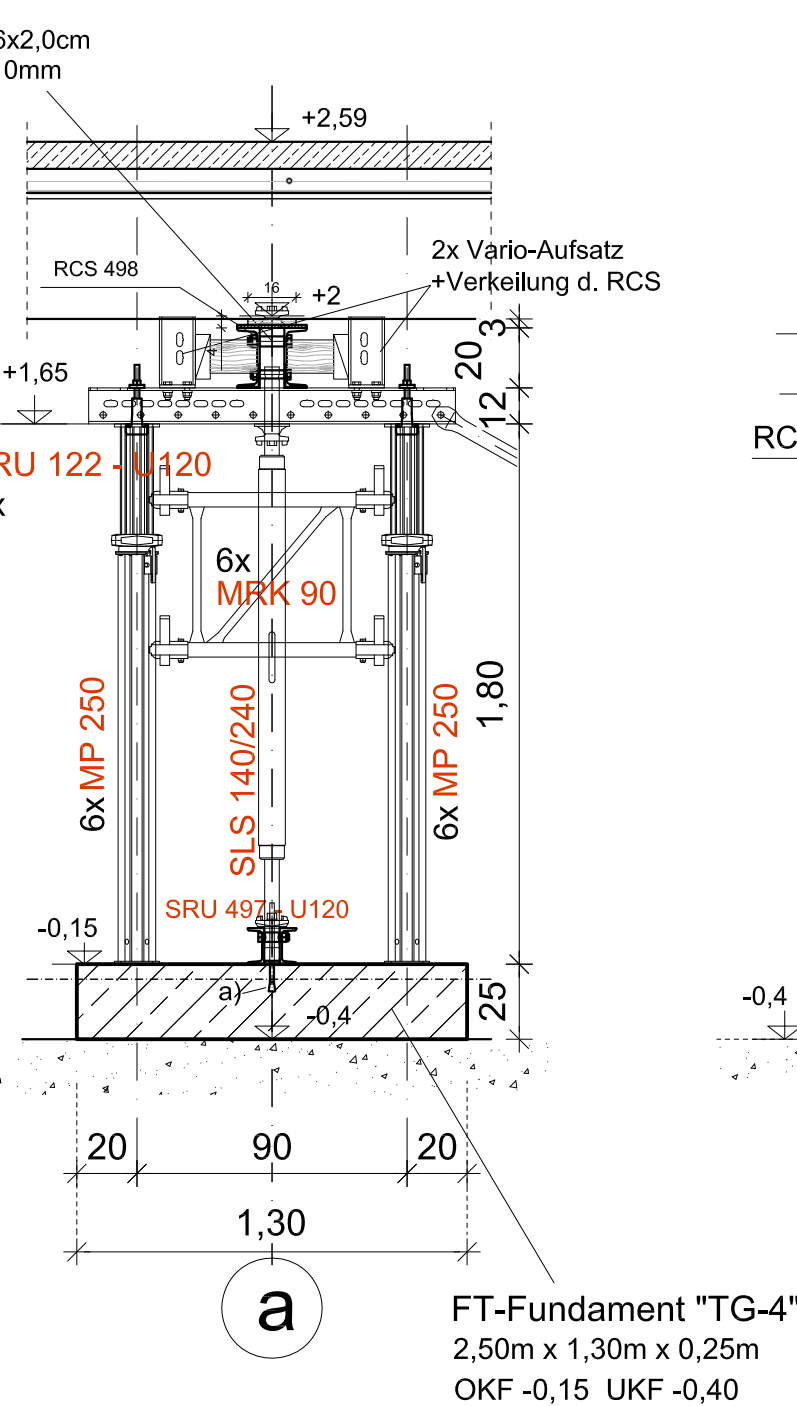

Traggerüst für Montage Fertigteile, Joch "c", Schnitt "C", M 1:25

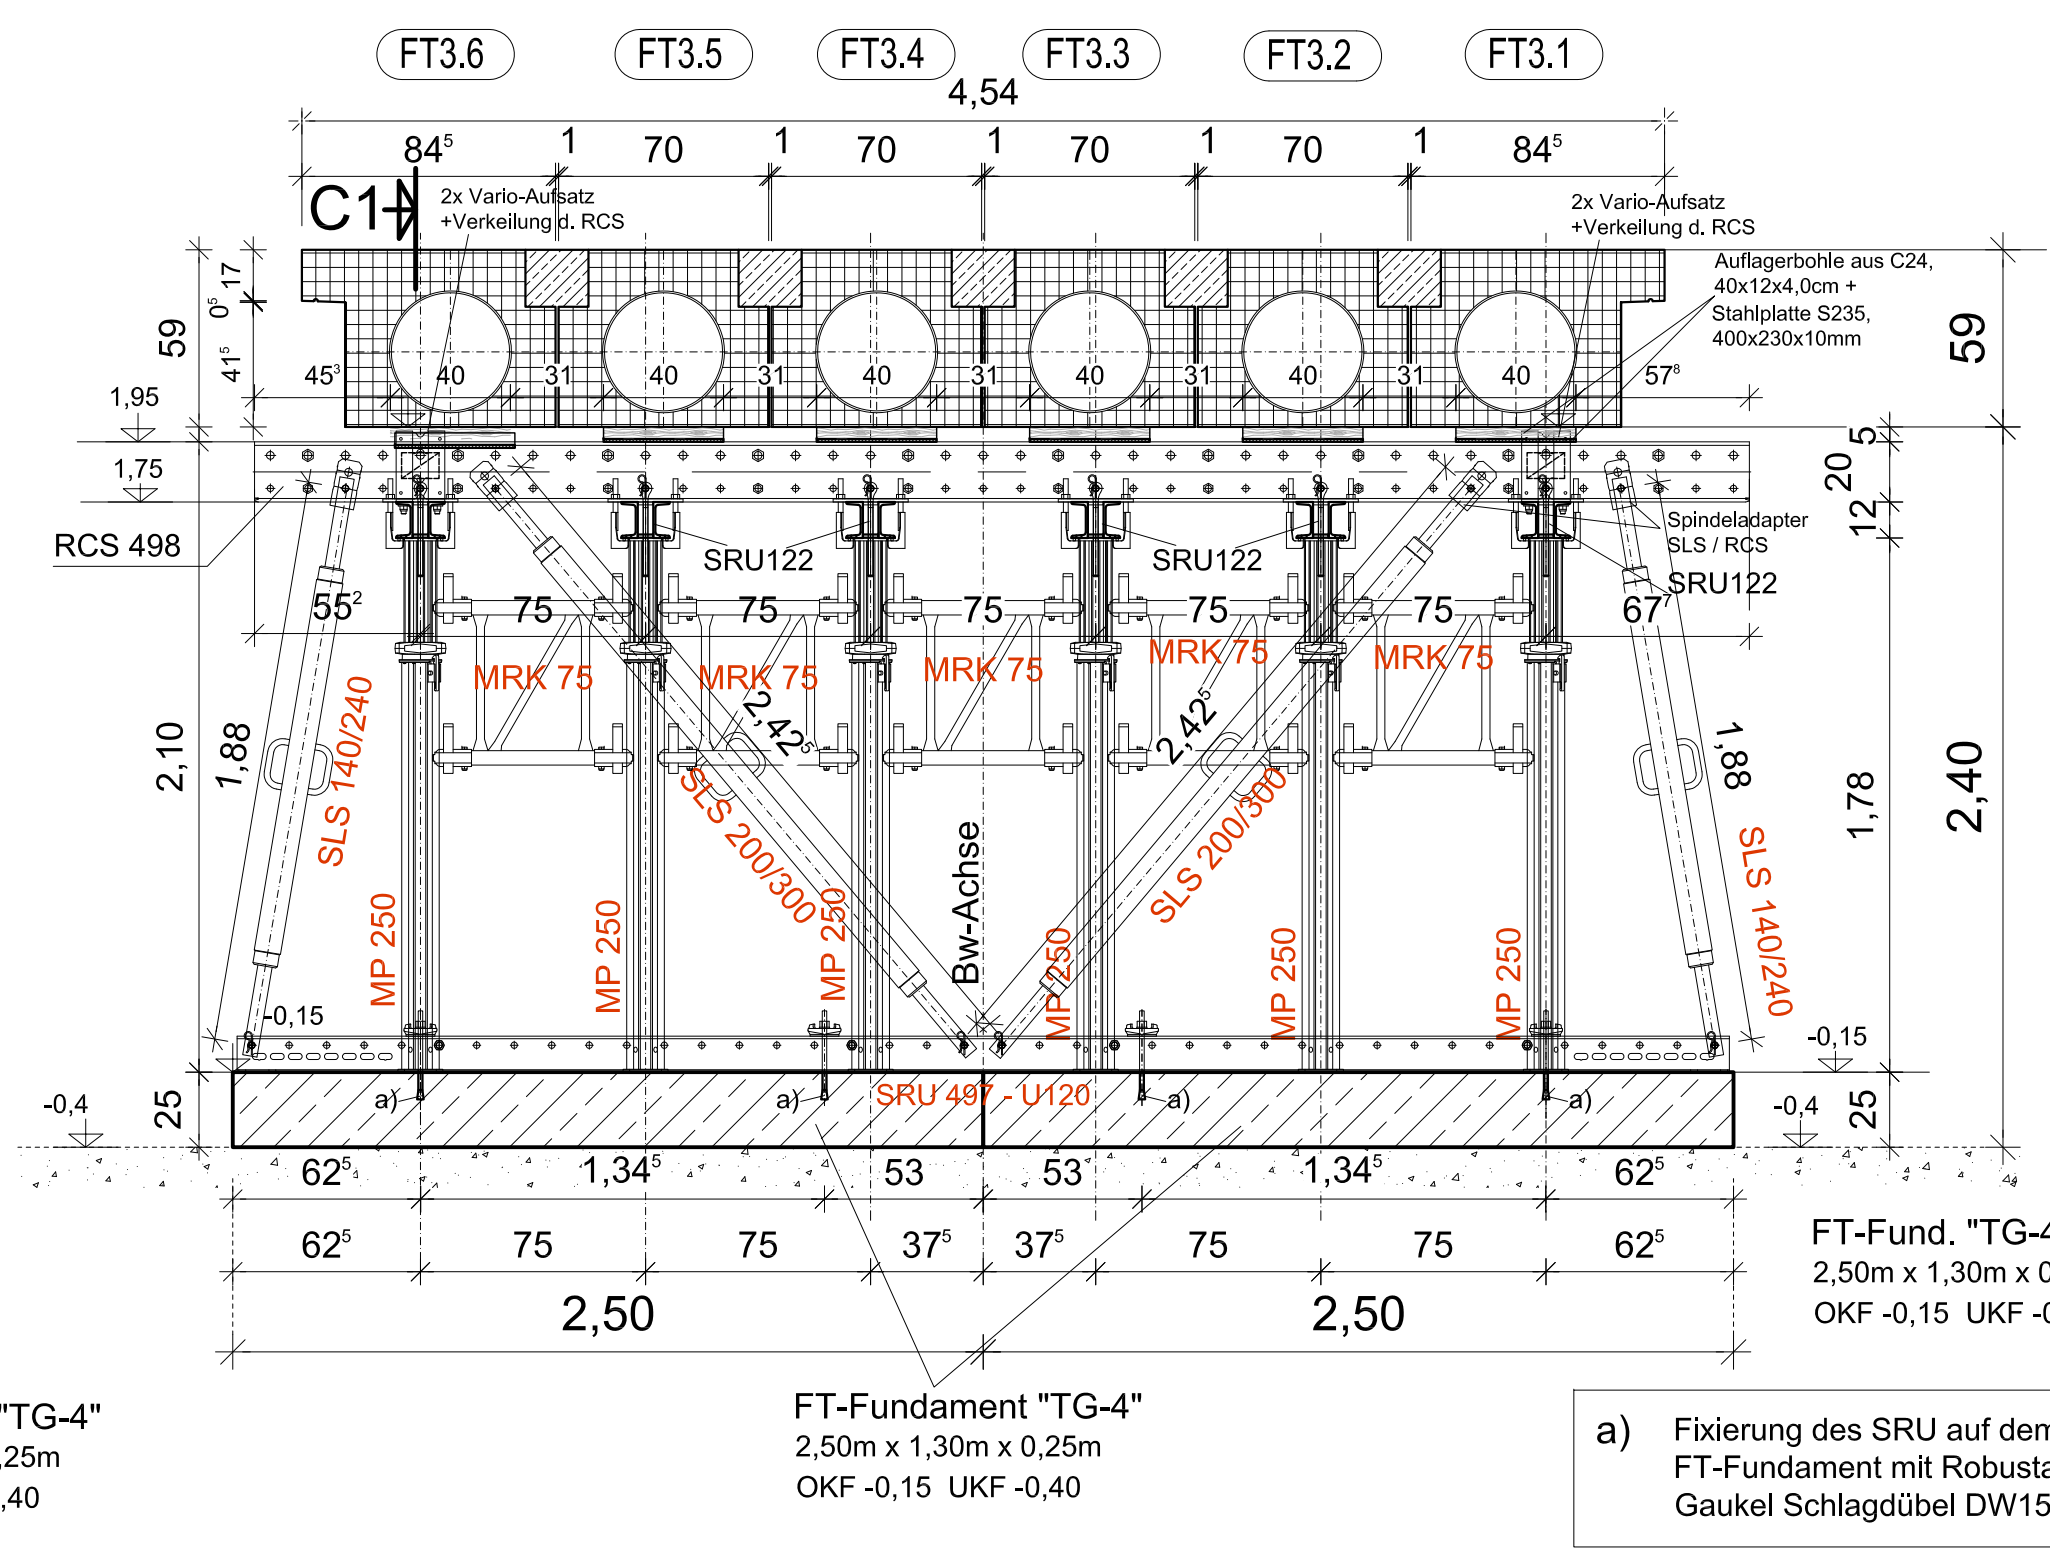


Teilschnitt "C1"

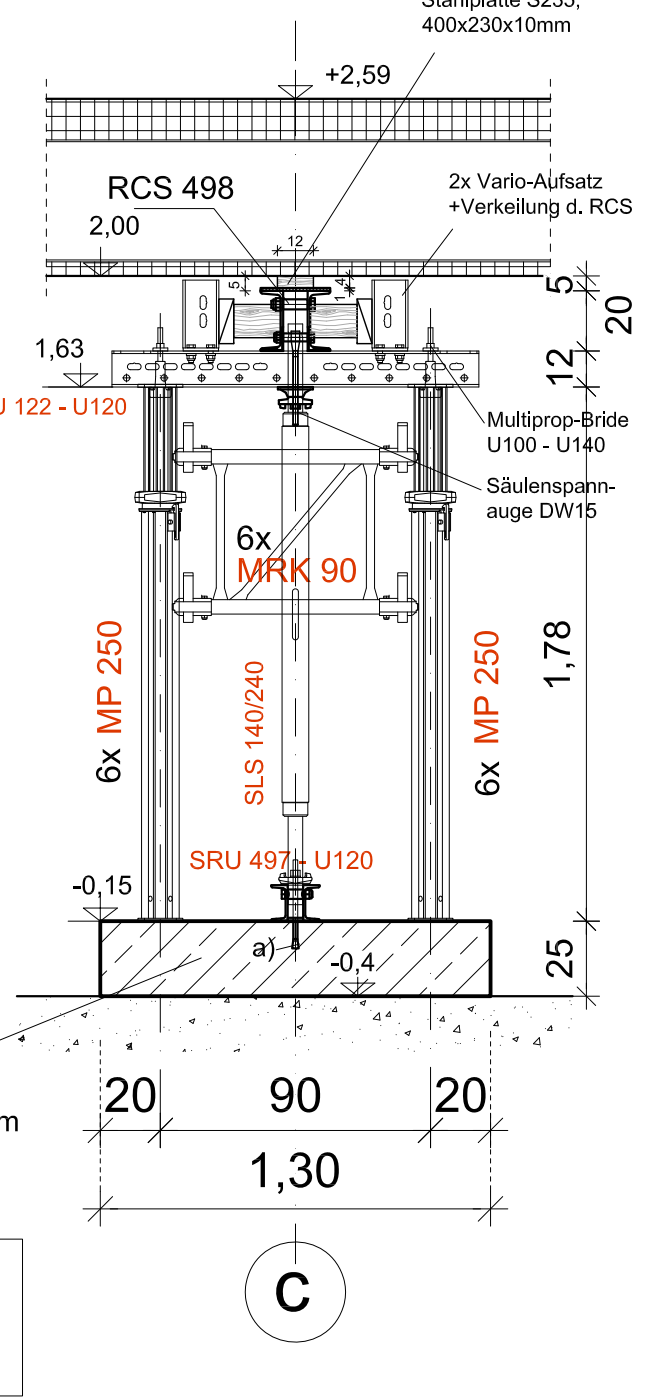


Detail "X", M 1:10

Feld 10-20 und 20-30,  
unter FT 1.1- 1.3 und 2.1 - 2.3

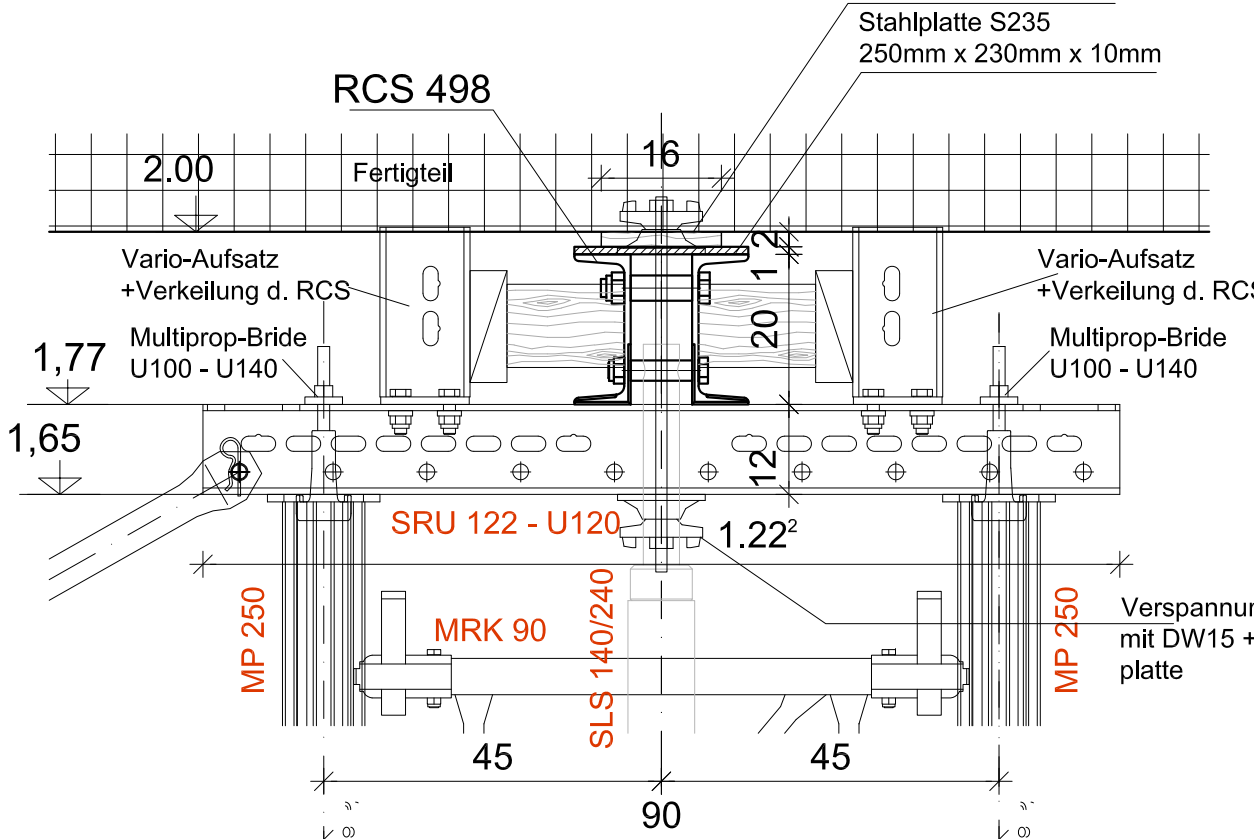


Vorfertigung, M 1:10


Stahlplatte, Feld 1+2:  
Bedarf: 6 Stück

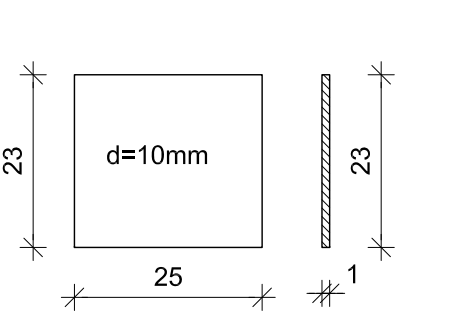


Stahlplatte, Feld 1+2:  
Bedarf: 12 Stück

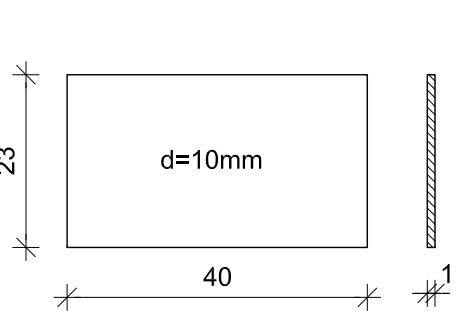

Auflagerholz D35,  
Feld 1+2:  
Bedarf: 6 Stück

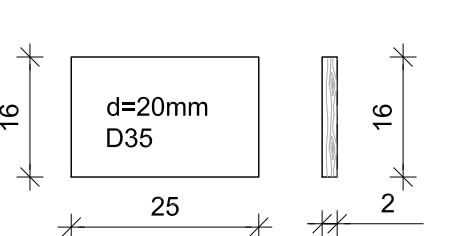


Auflagerholz C24 (S10),  
Feld 3:  
Bedarf: 12 Stück

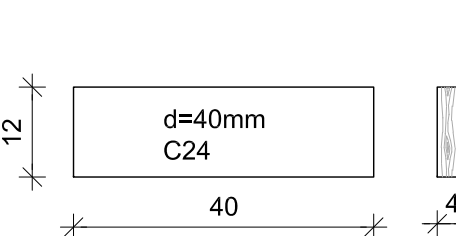

Detail "Y", M 1:10

Feld 30-40, unter FT 3.1- 3.6

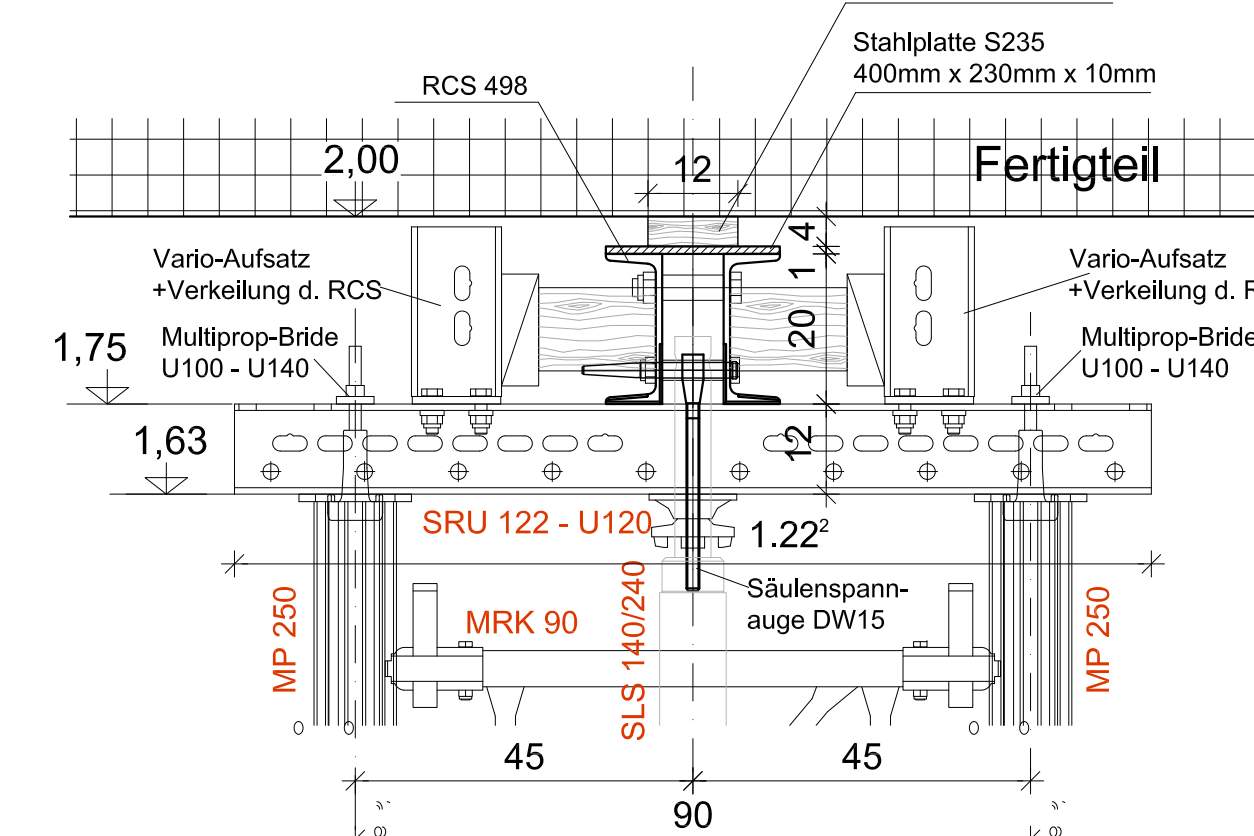

ANMERKUNGEN


**Material:**  
Schnittholz: NH C24 (S10)  
LH D35 (LS10)  
Beton FT-Fund.: C35/45 XC4 XD2 XF2, gemäß gesonderter Planung FT-Fund.  
Spannstahl: DW15 incl. Systemzubehör Z-12.5-82  
Stahlbauteile: S235  
Systembauteile PERI: Stahlriegel RCS, SRU incl. Zubehör  
PERI-Stützensystem "MultiProp", incl. Systemzubehör  
Robusta-Gaukel Schlagdübel DW15

PERI-Bauteile gemäß gesonderter Liste!  
Die RCS-Schienen sind aus dem Lager im Fertigteilwerk zu beziehen


Fertigteil-Fundamente "TG-4" gemäß Plan-Nr. Sp-TG-4

**Legende:**  
Stahlbeton  
Fertigteil  
Holz  
Stahl  
Mineralgemisch


Übersicht:

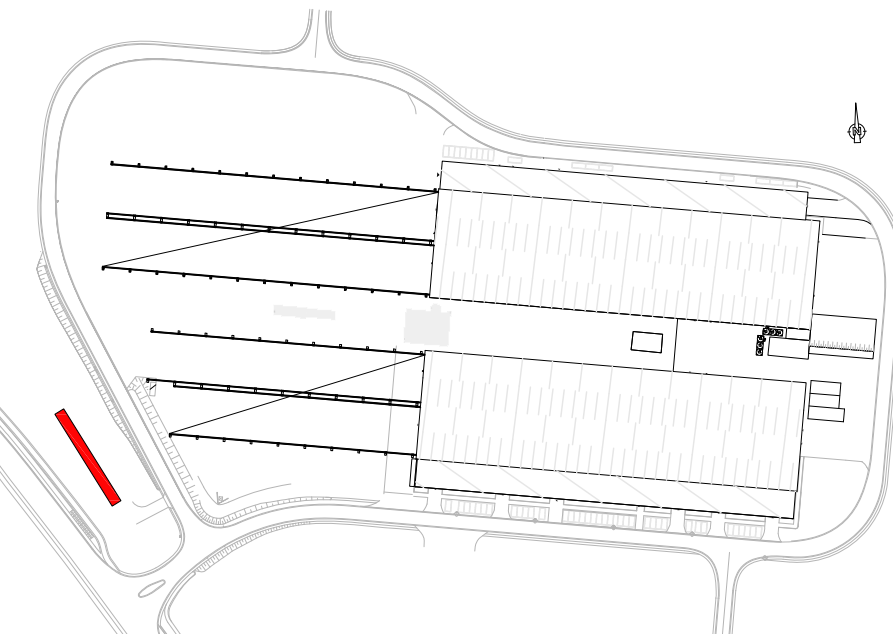


Traggerüst für Montage Fertigteile, Joch "b", Schnitt "B", M 1:25

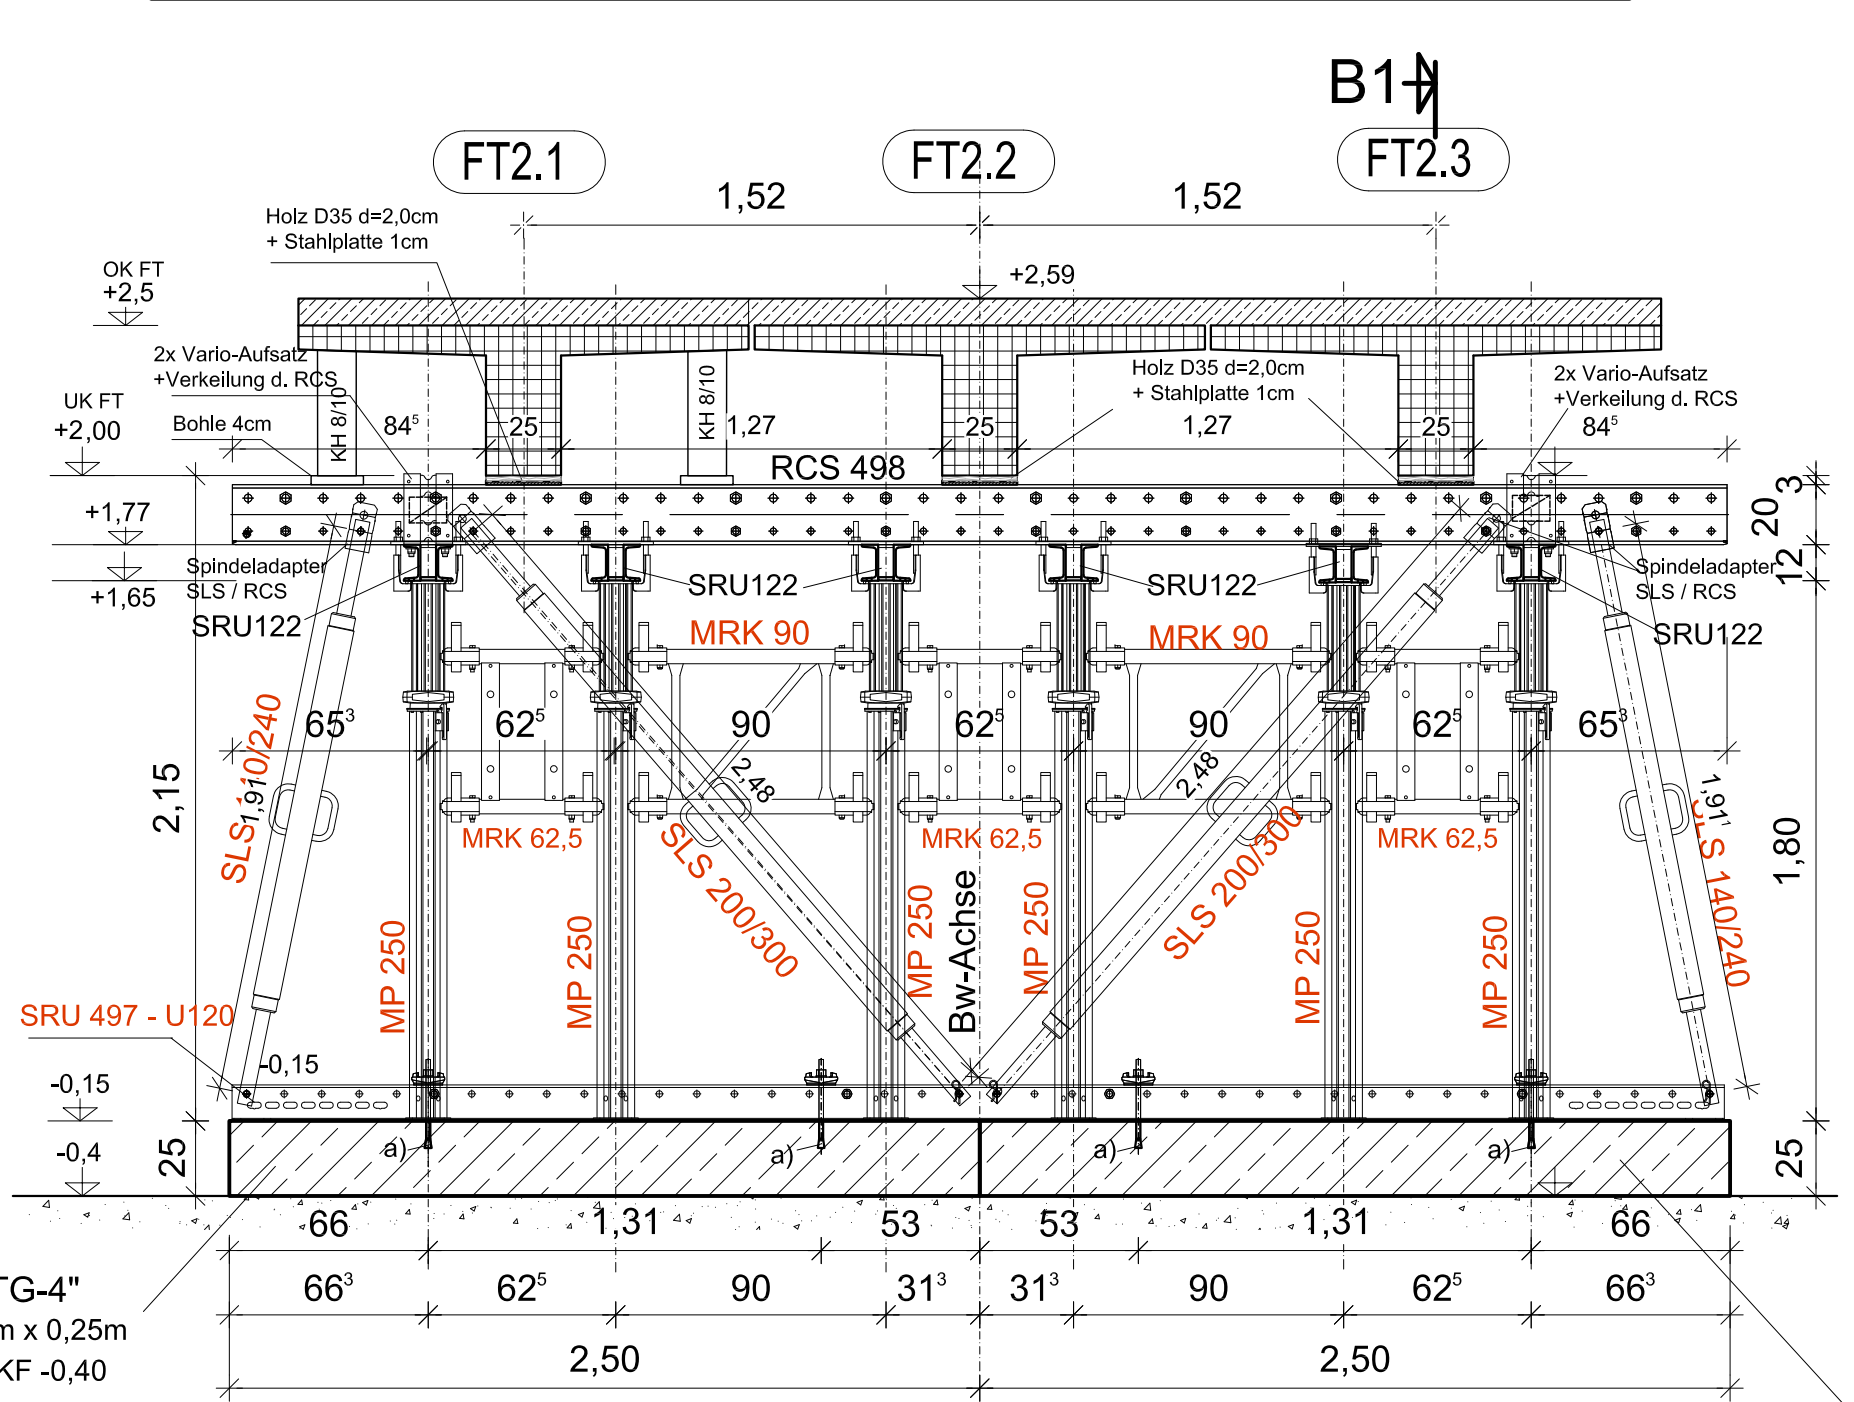


Teilschnitt "B1"

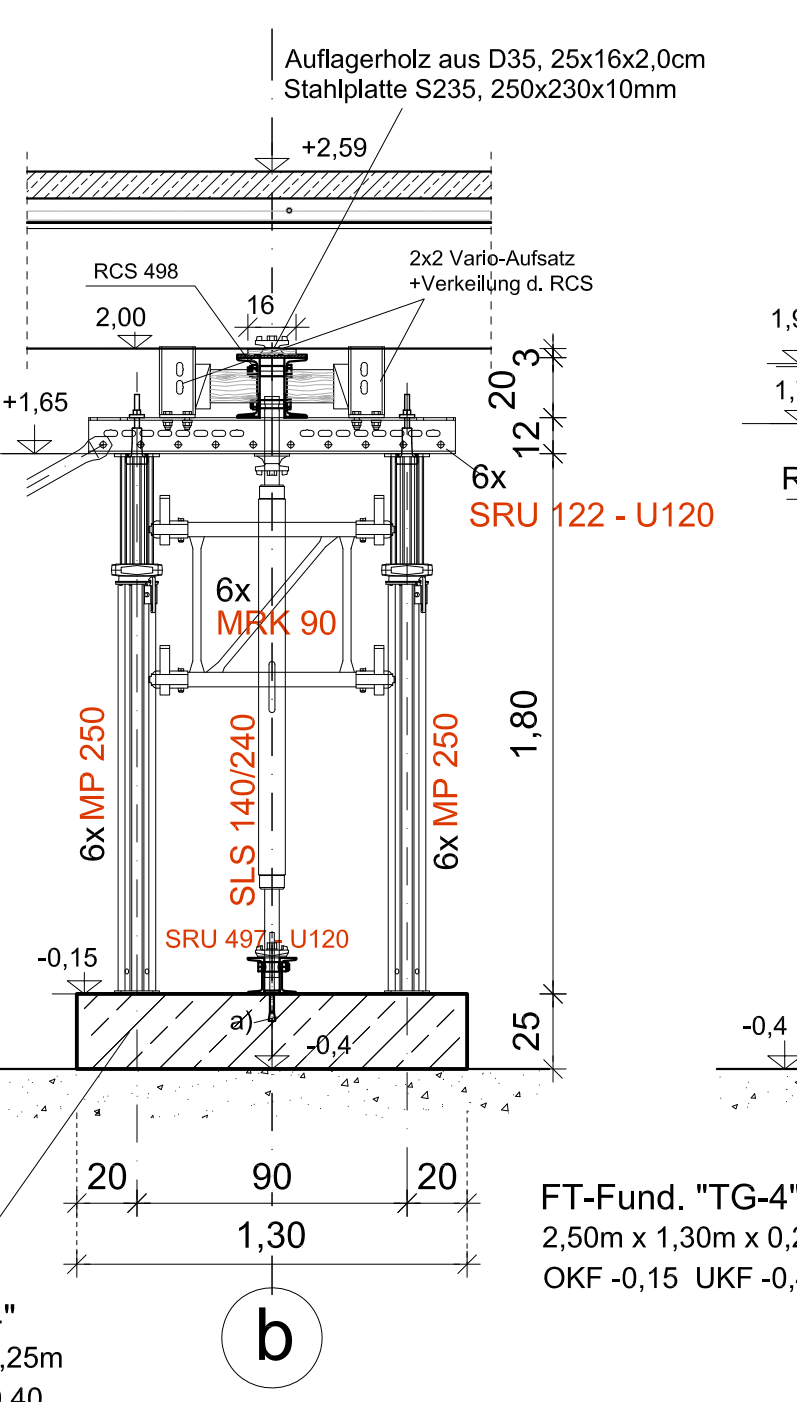



Traggerüst für Montage Fertigteile, Joch "d", Schnitt "D", M 1:25

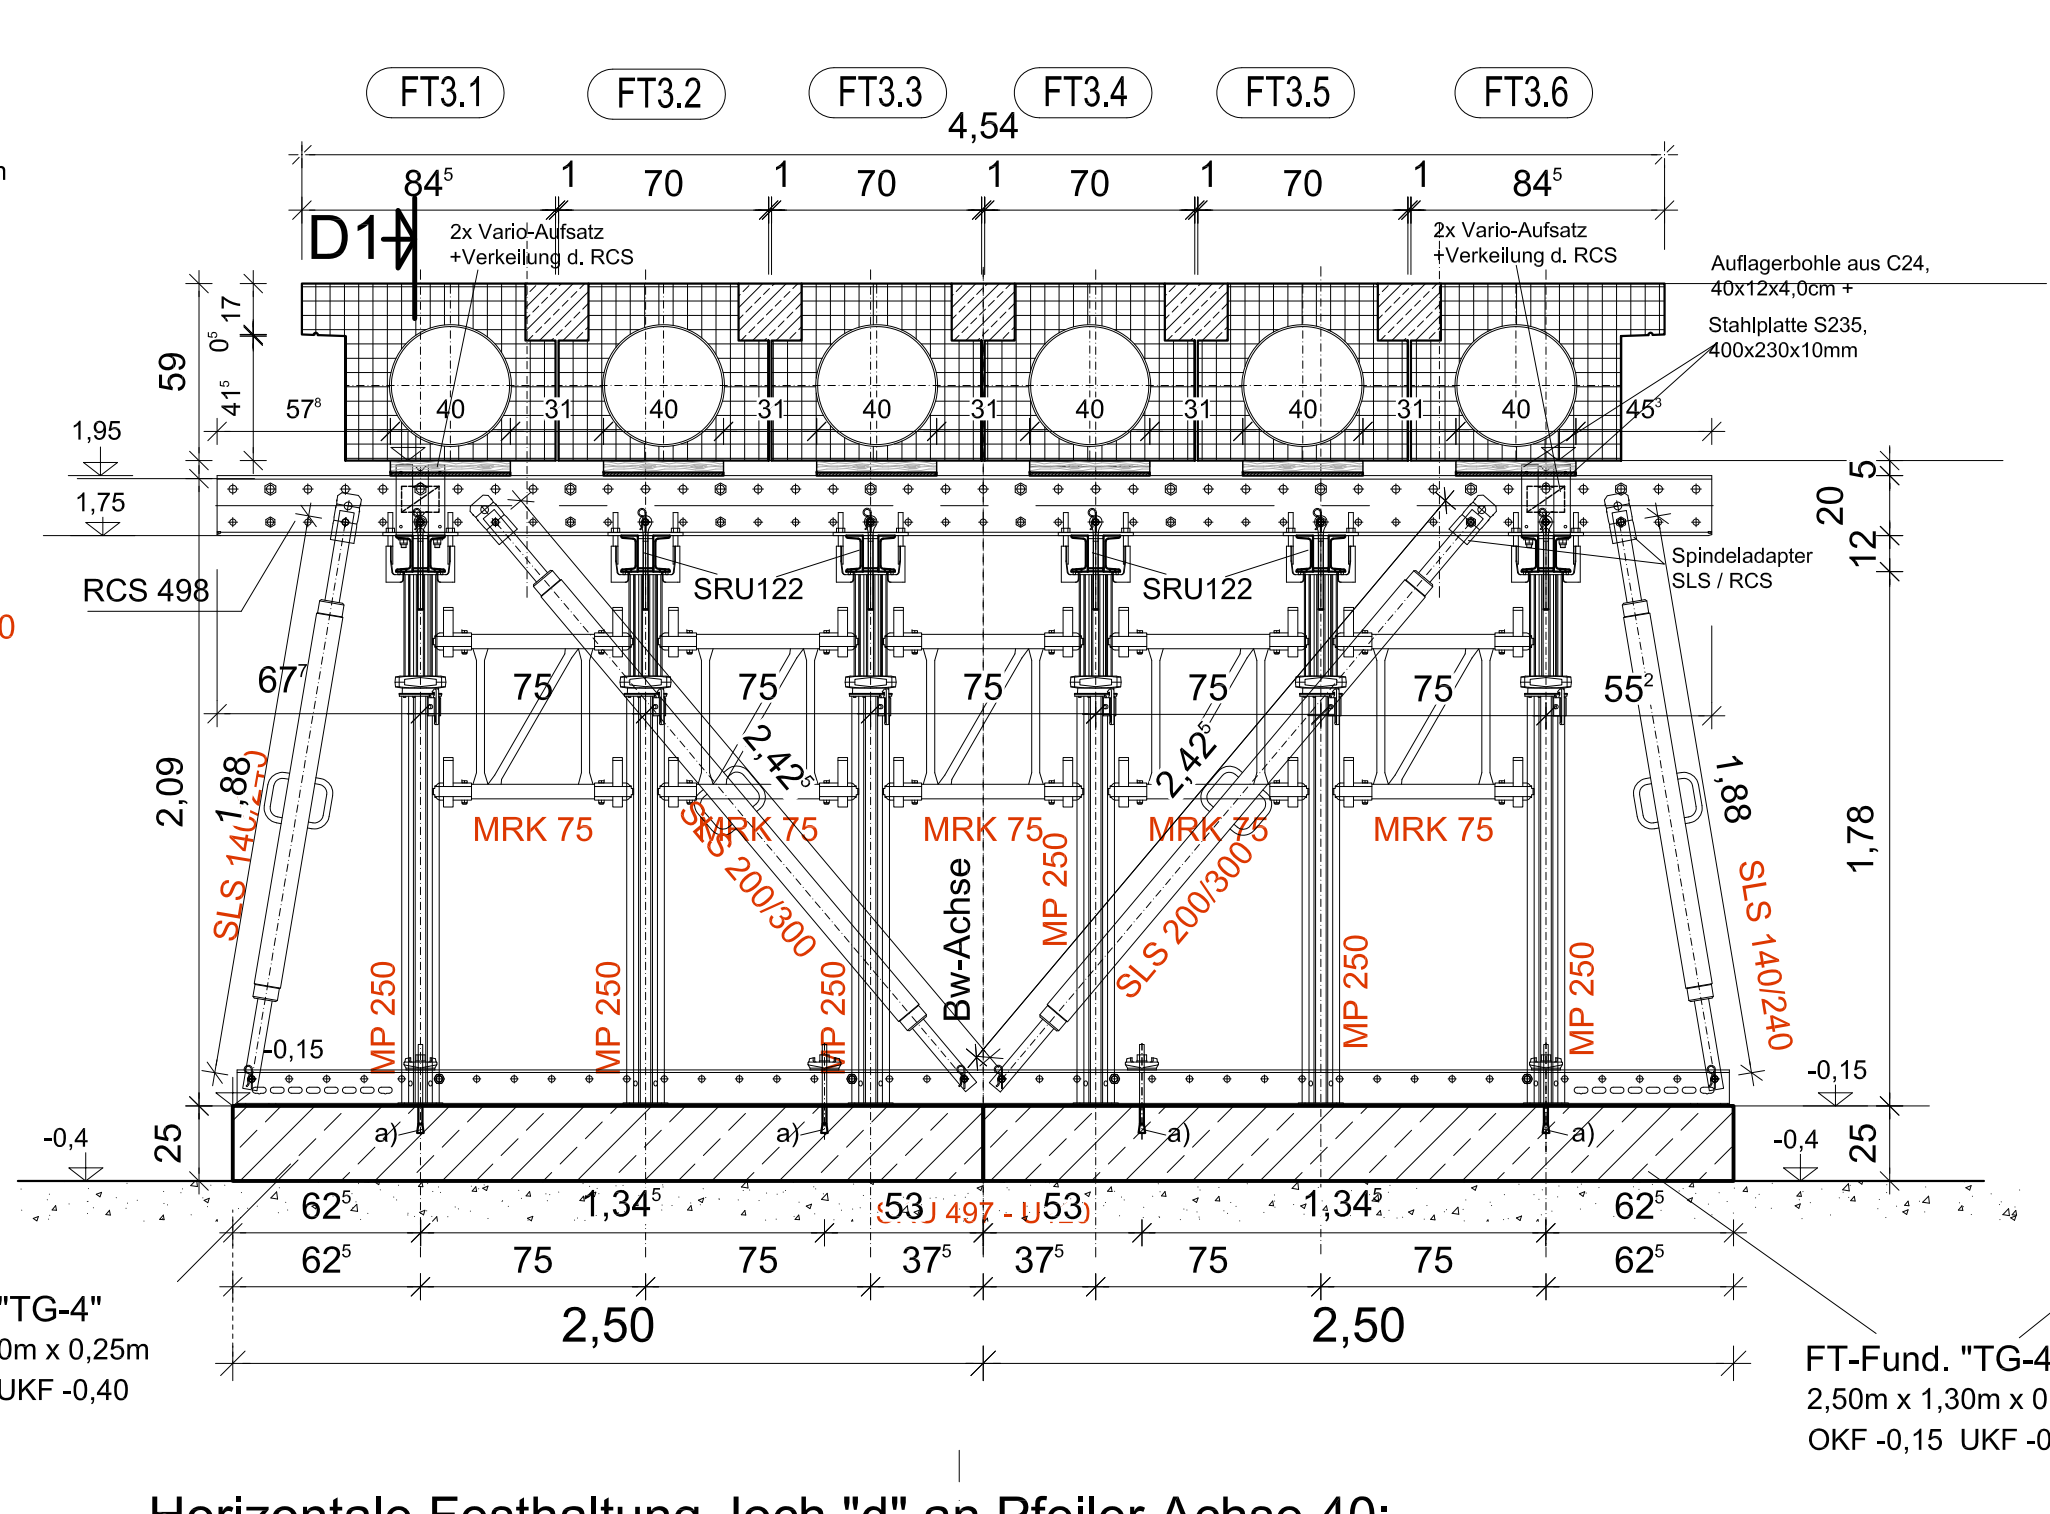

Teilschnitt "D1"

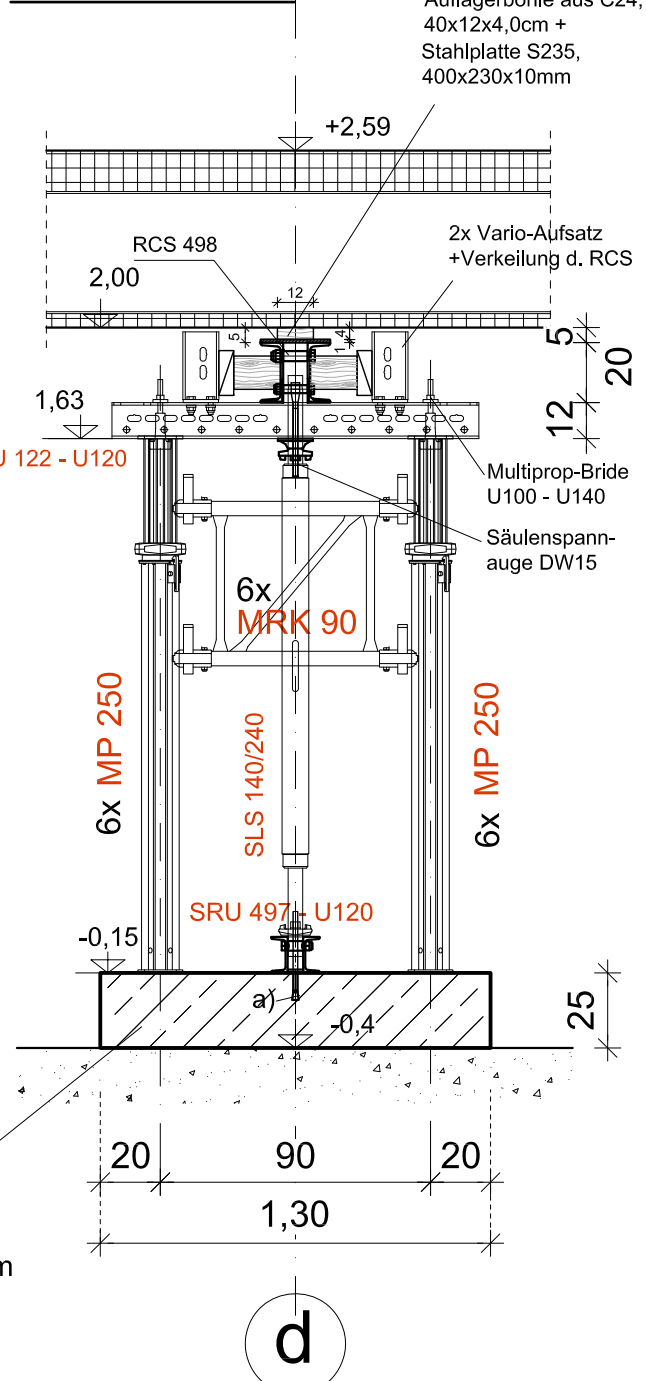


Verbindung SRU-RCS

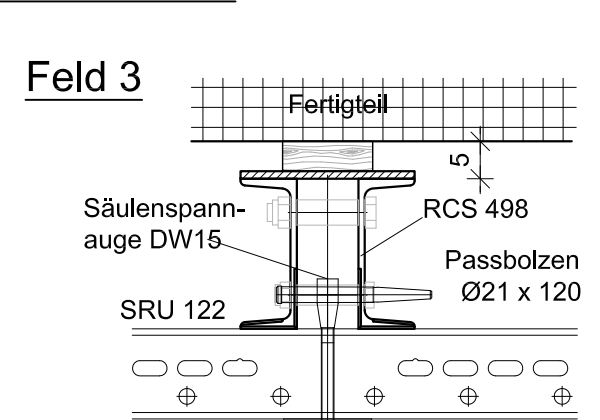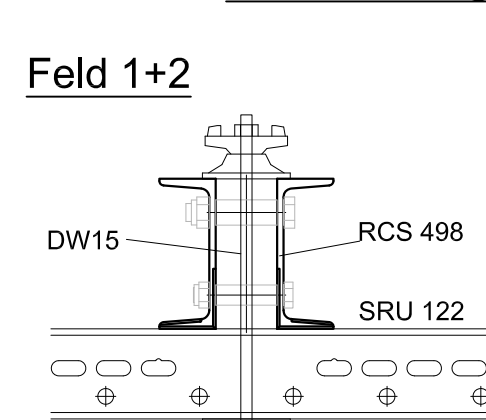


Zugehörige Pläne

| Plan-Nr.            | Bezeichnung                    |
|---------------------|--------------------------------|
| BÜP01               | Bauwerksübersichtsplan         |
| SP-UB A10           | Schalplan Unterbauten Achse 10 |
| SP-UB A20           | Schalplan Unterbauten Achse 20 |
| SP-UB A30           | Schalplan Unterbauten Achse 30 |
| SP-UB A40           | Schalplan Unterbauten Achse 40 |
| EP-F1.1 bis EP-F1.3 | Spannbetonträger Feld 1        |
| EP-F2.1 bis EP-F2.3 | Spannbetonträger Feld 2        |
| EP-F3.1 bis EP-F3.6 | Hentschke-Träger Feld 3        |


Horizontale Festhaltung Joch "c" an Pfeiler Achse 30:

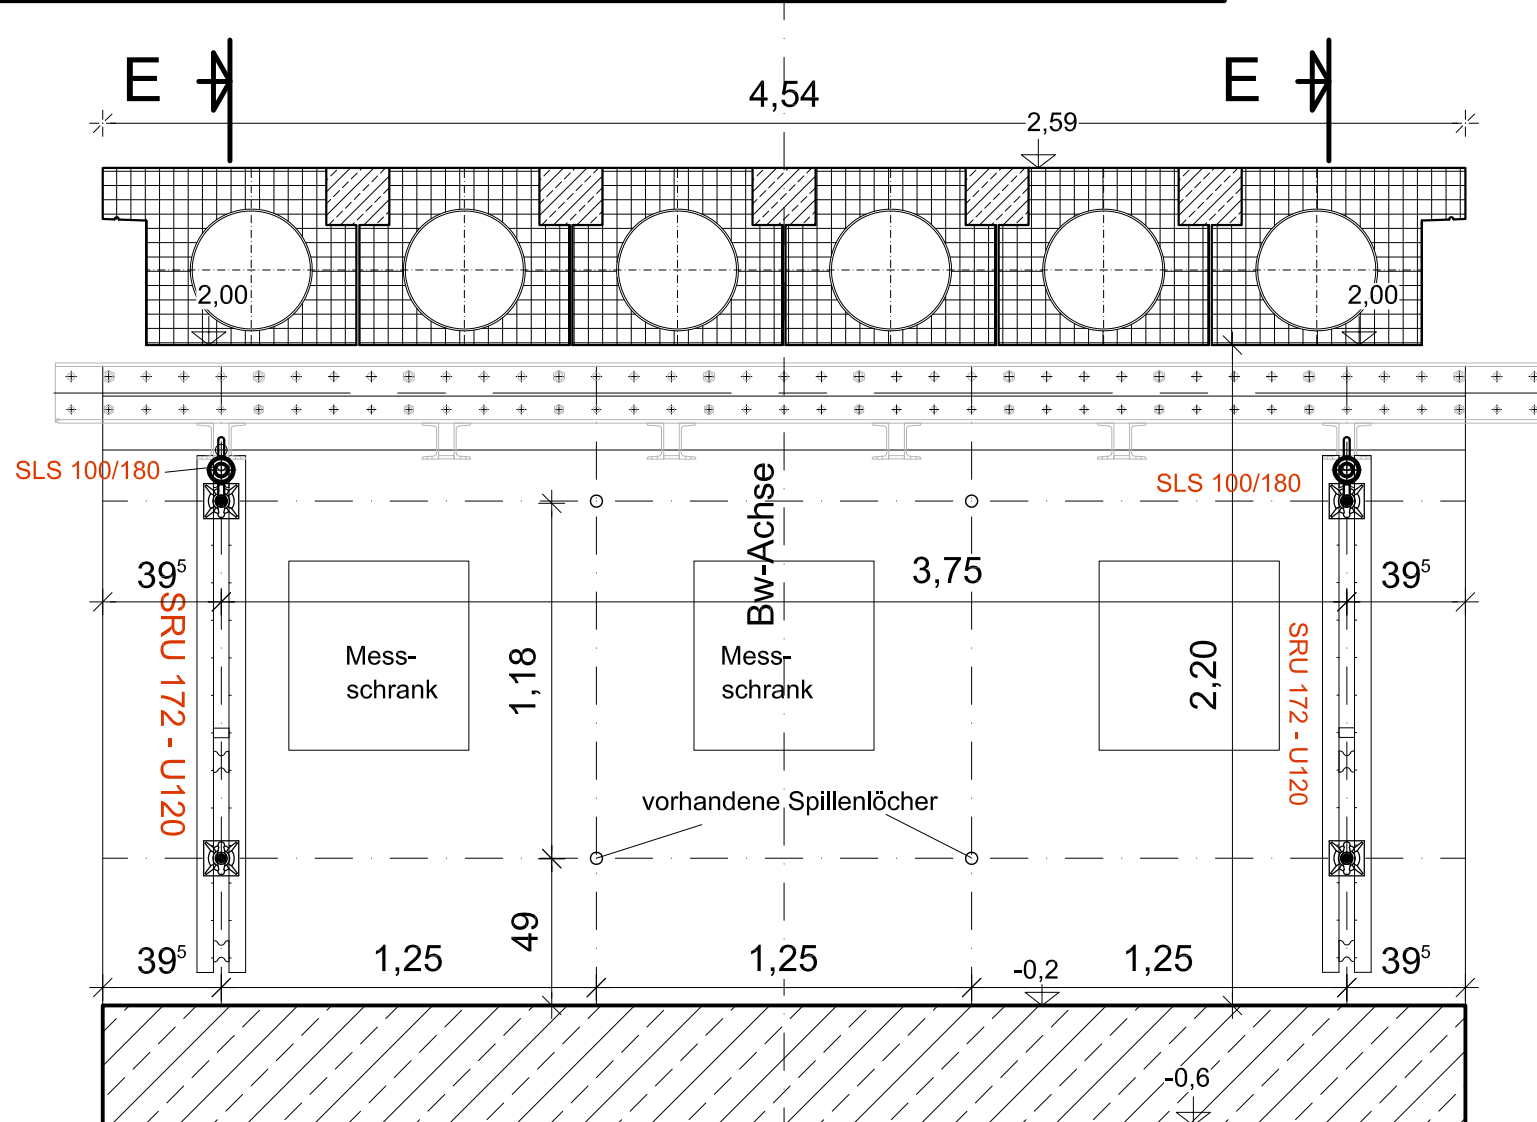


Teilschnitt "E":

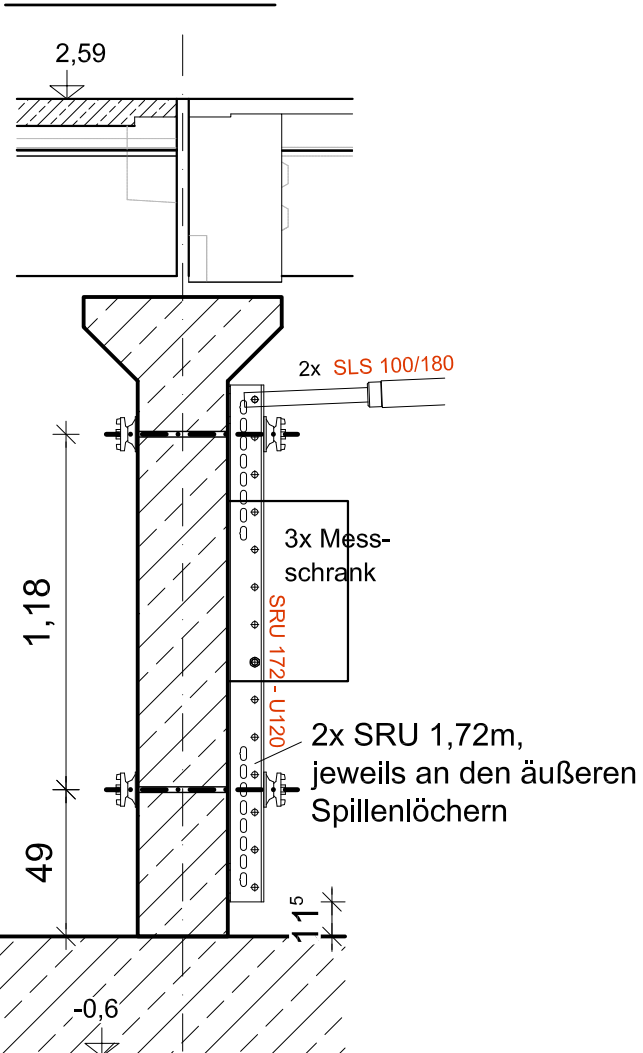



Horizontale Festhaltung Joch "d" an Pfeiler Achse 40:

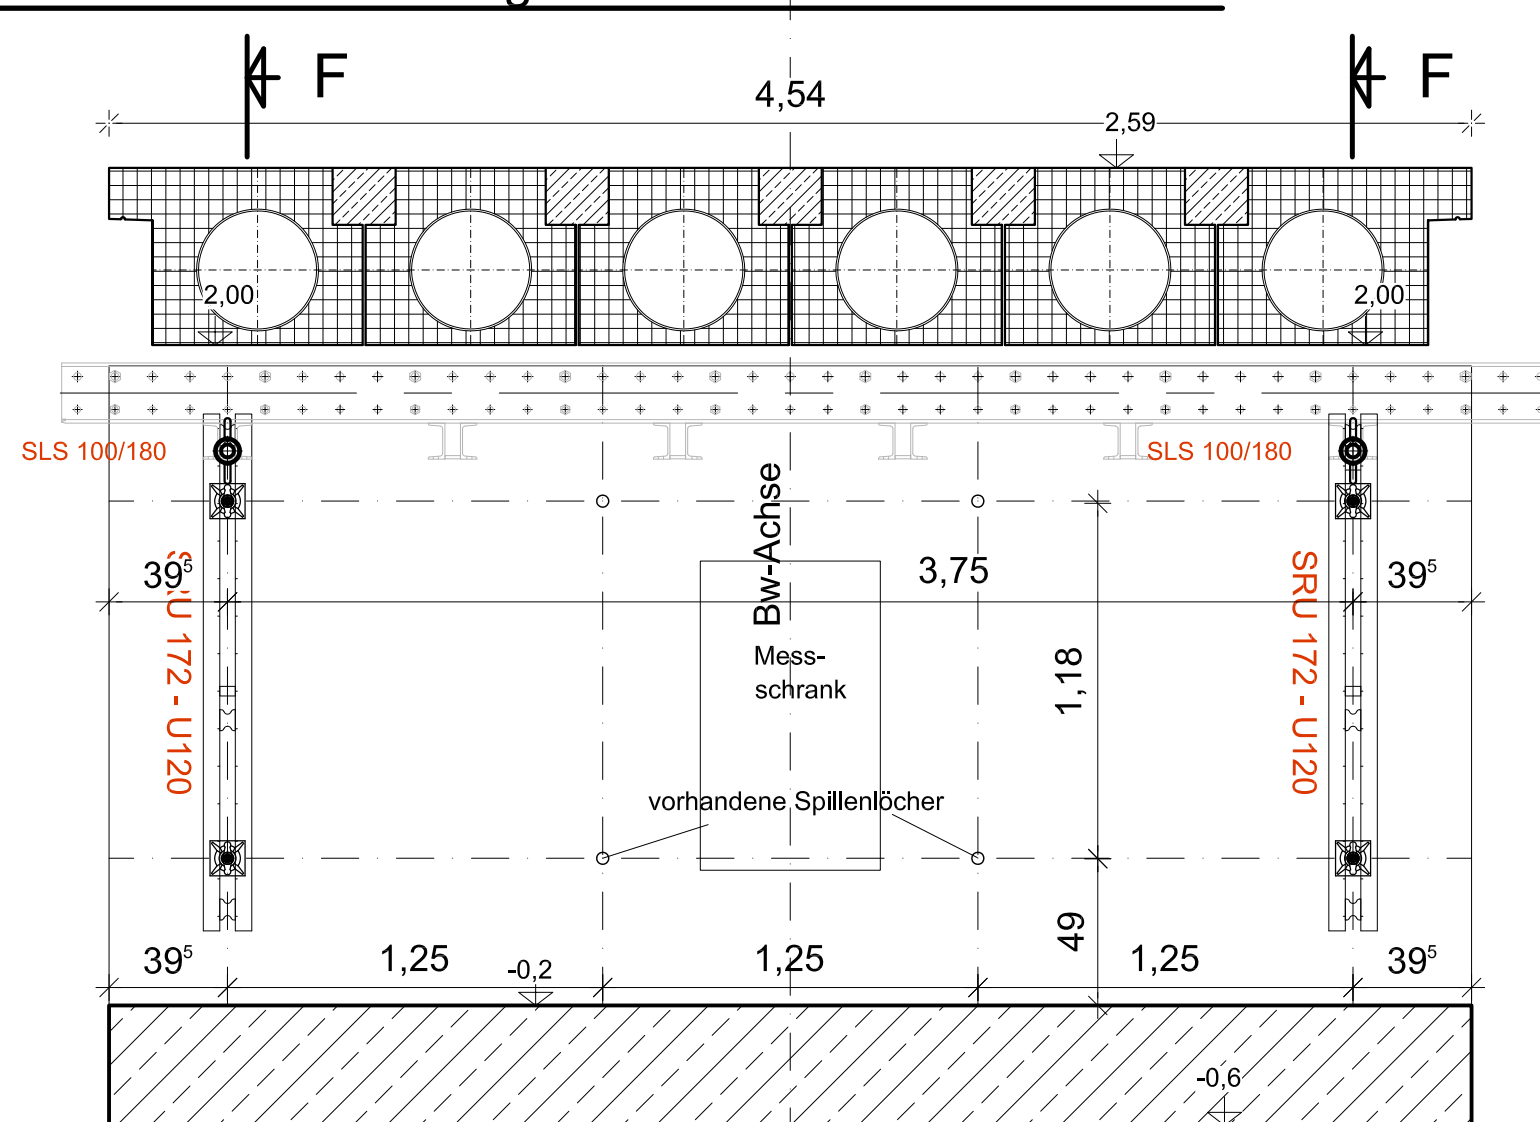

Teilschnitt "F":

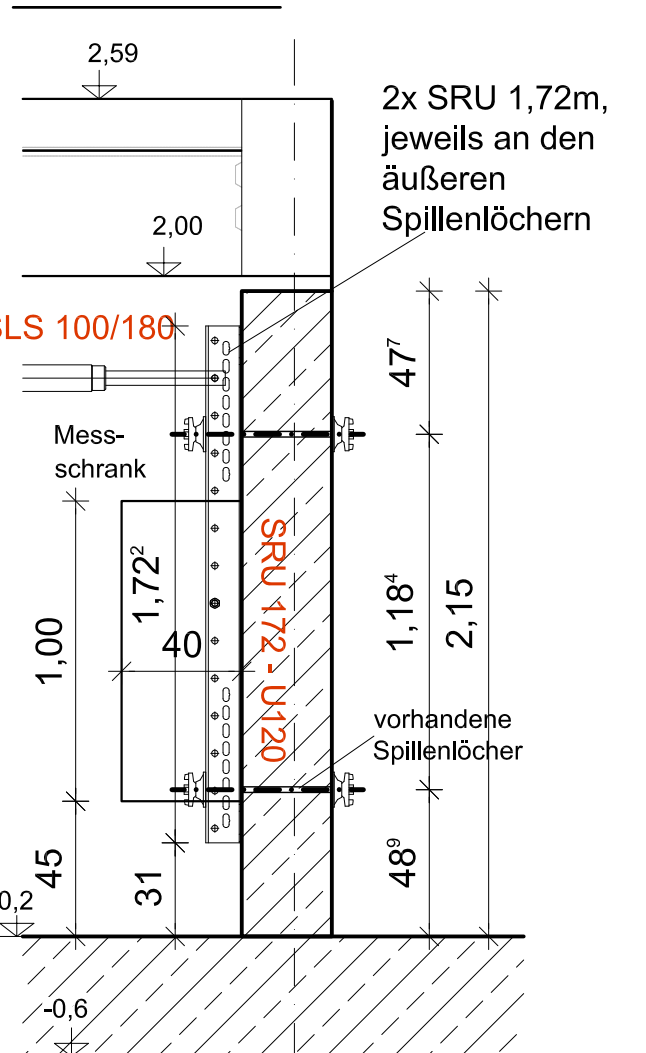

Übersicht:

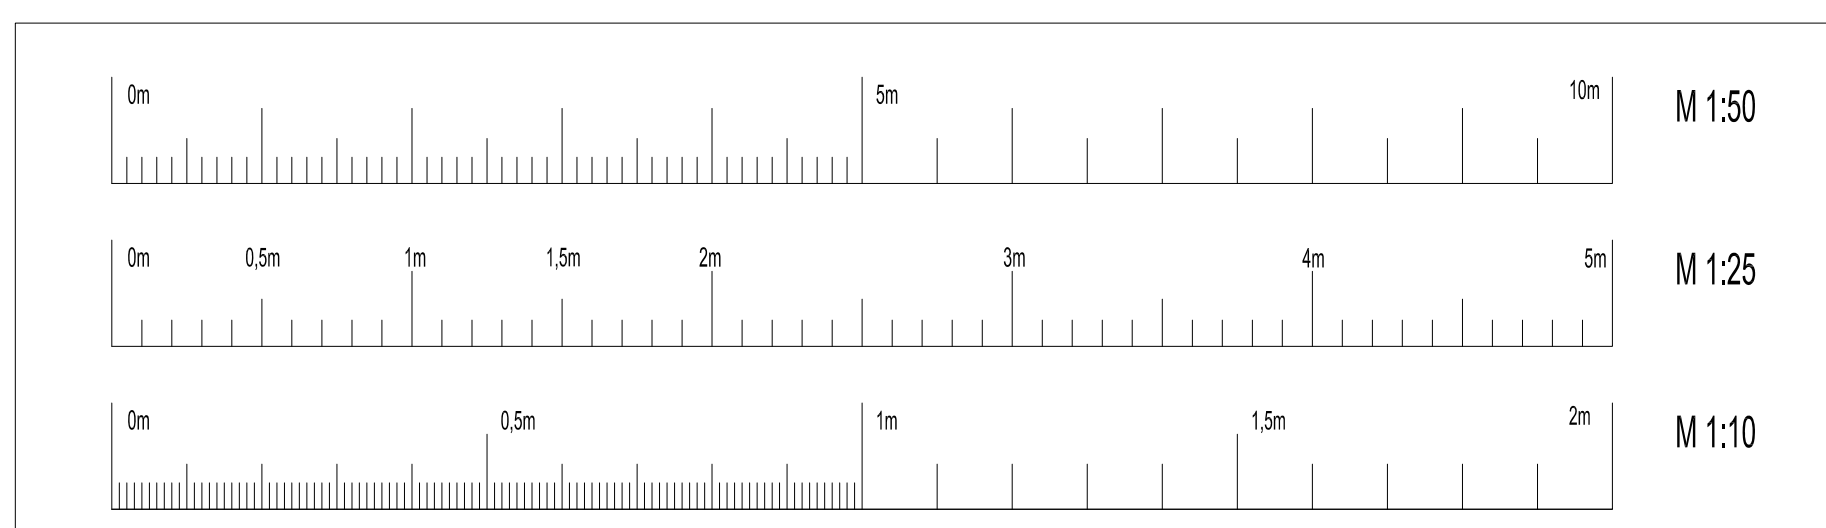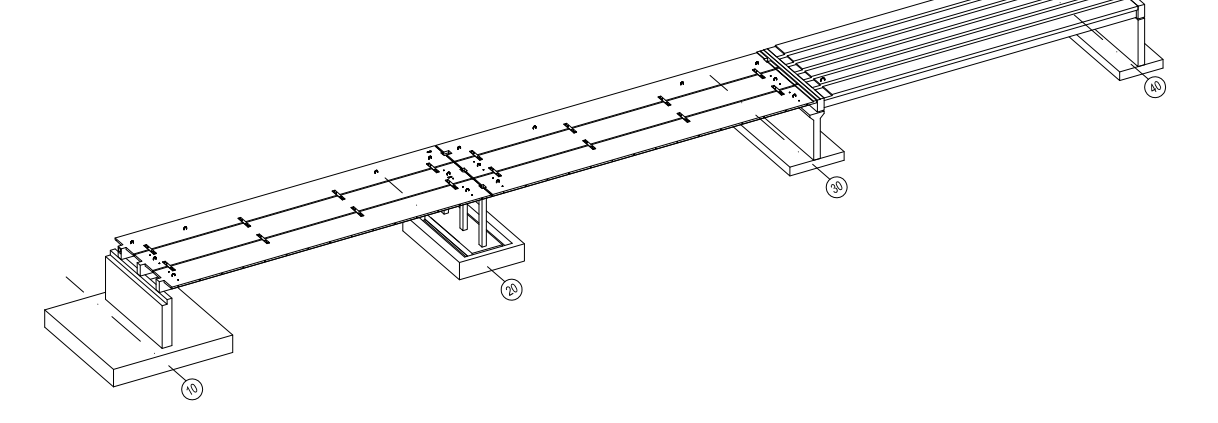

Werkplanung

|                |   |
|----------------|---|
| Bauherr:       | Intern   |
| Bauvorhaben:   | IDA-KI<br>Errichtung einer 3-Feld-Brücke   |
| Darstellung:   | Traggerüste für Montage der Fertigteile<br>3-Feld-Brücke IDA-KI                                                                                         |
| Planung:       | Hentschke<br>Betonfertigteilwerk Bautzen<br>Hentschke Bau GmbH<br>Hoyerswerder Straße 42<br>02625 Bautzen<br>Tel.: 03591 6703-896<br>Fax: 03591 6703-42 |
| Projekt-Nr.:   | 187.215   |
| 50 - 999 - 035 |   |
| gezeichnet:    | U. Kögler   |
| Datum:         | 12.10.2023   |
| Unterschrift:  | <i>U. Kögler</i>   |
| Maßstab:       | 1:50; 25:10   |
| Plan-Nr.:      | TG-01   |