
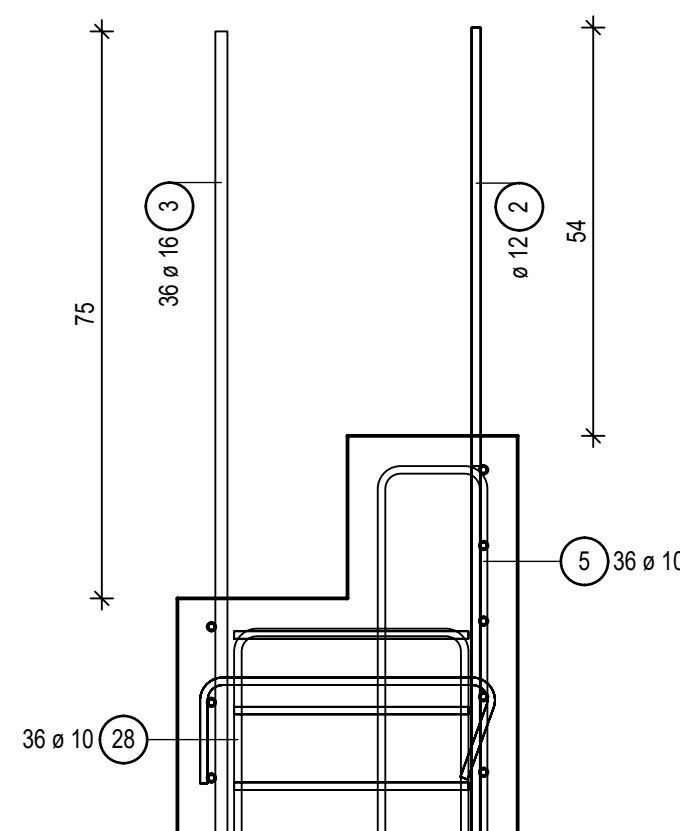



Schalung
Draufsicht

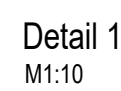

Pos.	Stück	Mattenbez.	Länge [m]	Breite [m]	Gewicht [kg]
1	4	Q636A	5.430	2.350	477.84
2	2	Q636A	5.430	1.520	154.54

Figure 1: Schematic representation of the two experimental conditions. The left panel shows a 4°Q636A mutant with a single binding site (red) and a single binding event (red arrow). The right panel shows a 2°Q636A mutant with two binding sites (red) and two binding events (red arrows).

Schnitt 1 - 1

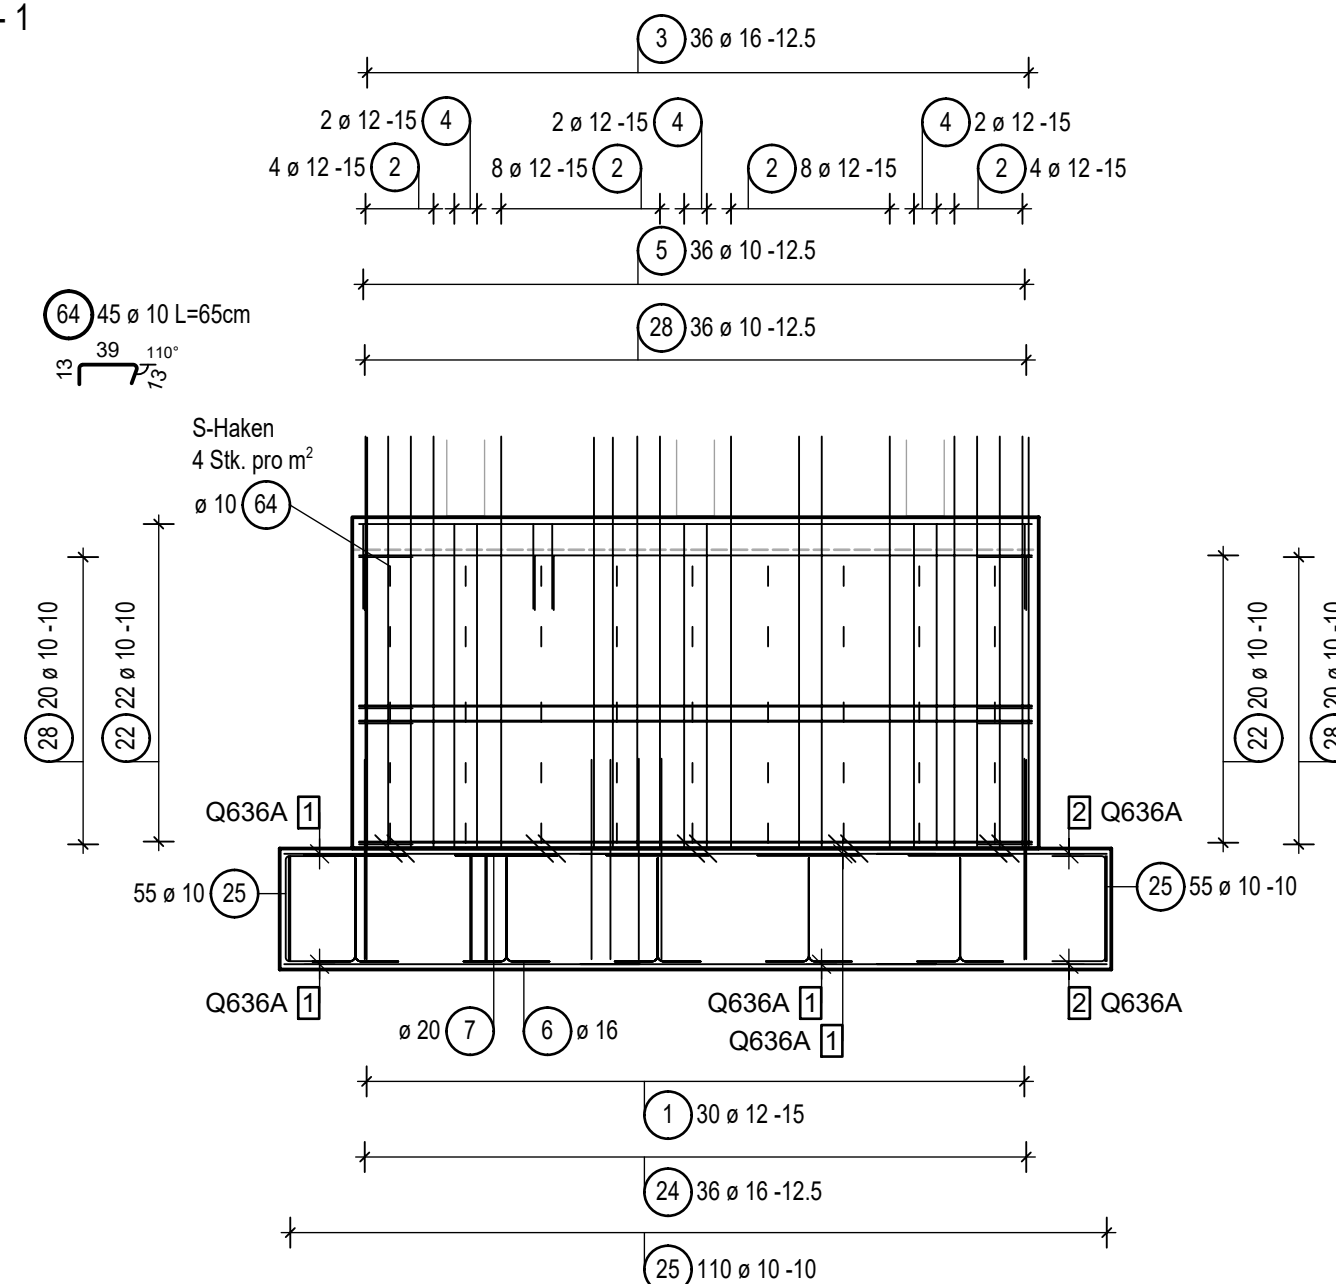

Pos.	Stck	ø	Einzel Länge	Bemaßte Biegeform (unmaßstäblich)	Gesamt Länge	Masse
		[mm]	[m]		[m]	[kg]
1	30	12	1.94		58.20	51.68
2	24	12	2.73		65.52	58.18
3	36	16	2.73		98.28	155.28
4	6	12	2.15		12.90	11.46
5	36	10	1.29		46.44	28.65
6	25	16	2.30		57.50	90.85
7	25	20	0.70		17.50	43.23
22	42	10	4.46		187.32	115.58
24	36	16	1.94		69.84	110.35
25	220	10	1.43		314.60	194.11
28	76	10	1.04		79.04	48.77
64	45	10	0.65		29.25	18.05

Gesamtmasse : 926.18

BAUSTOFFFANGABEN (Planspezifisch)					
Bauteile	Expositionsklassen	Beton	Δs	min c	nom c
Fundament (FU01)	XC2	C30/37			3,5cm
Widerlagewand (WLW01)	XC4	C30/37			4,0cm
Bereiche mit höheren Betonfestigkeiten beachten					
Betonstahl : BSt 500 M(B) BSt 500 S(B)		Standardfaser: 1,0/ 1,0 cm			
f					
e					
d					
c					
b					
a	11.07.2023	Graf	Freigabe		
INDEX	DATUM	GEZ.			

Werkplanung		Planung:  Betonfertigteilterwerk Bautzen Hentschke Bau GmbH Hoyerswerdaer Straße 42 02625 Bautzen Tel.: 03591 6703- Fax: 03591 6703-42
		Projekt-Nr.: XXXX-XX 50 - 999 - 035
Bauherr: Intern		
Bauvorhaben: IDA-KI Errichtung einer 3-Feld-Brücke	gezeichnet: Graf Datum: 04.07.2023 Unterschrift:	
Darstellung: Bewehrungsplan Unterbauten Achse 10	Maßstab: 1 : 50 Plan-Nr. Planbezeichnung BP-UB10	a