



Bewehrungsplan Unterbauten Achse (20)


Bewehrung Fundament (FU02.1)
Draufsicht

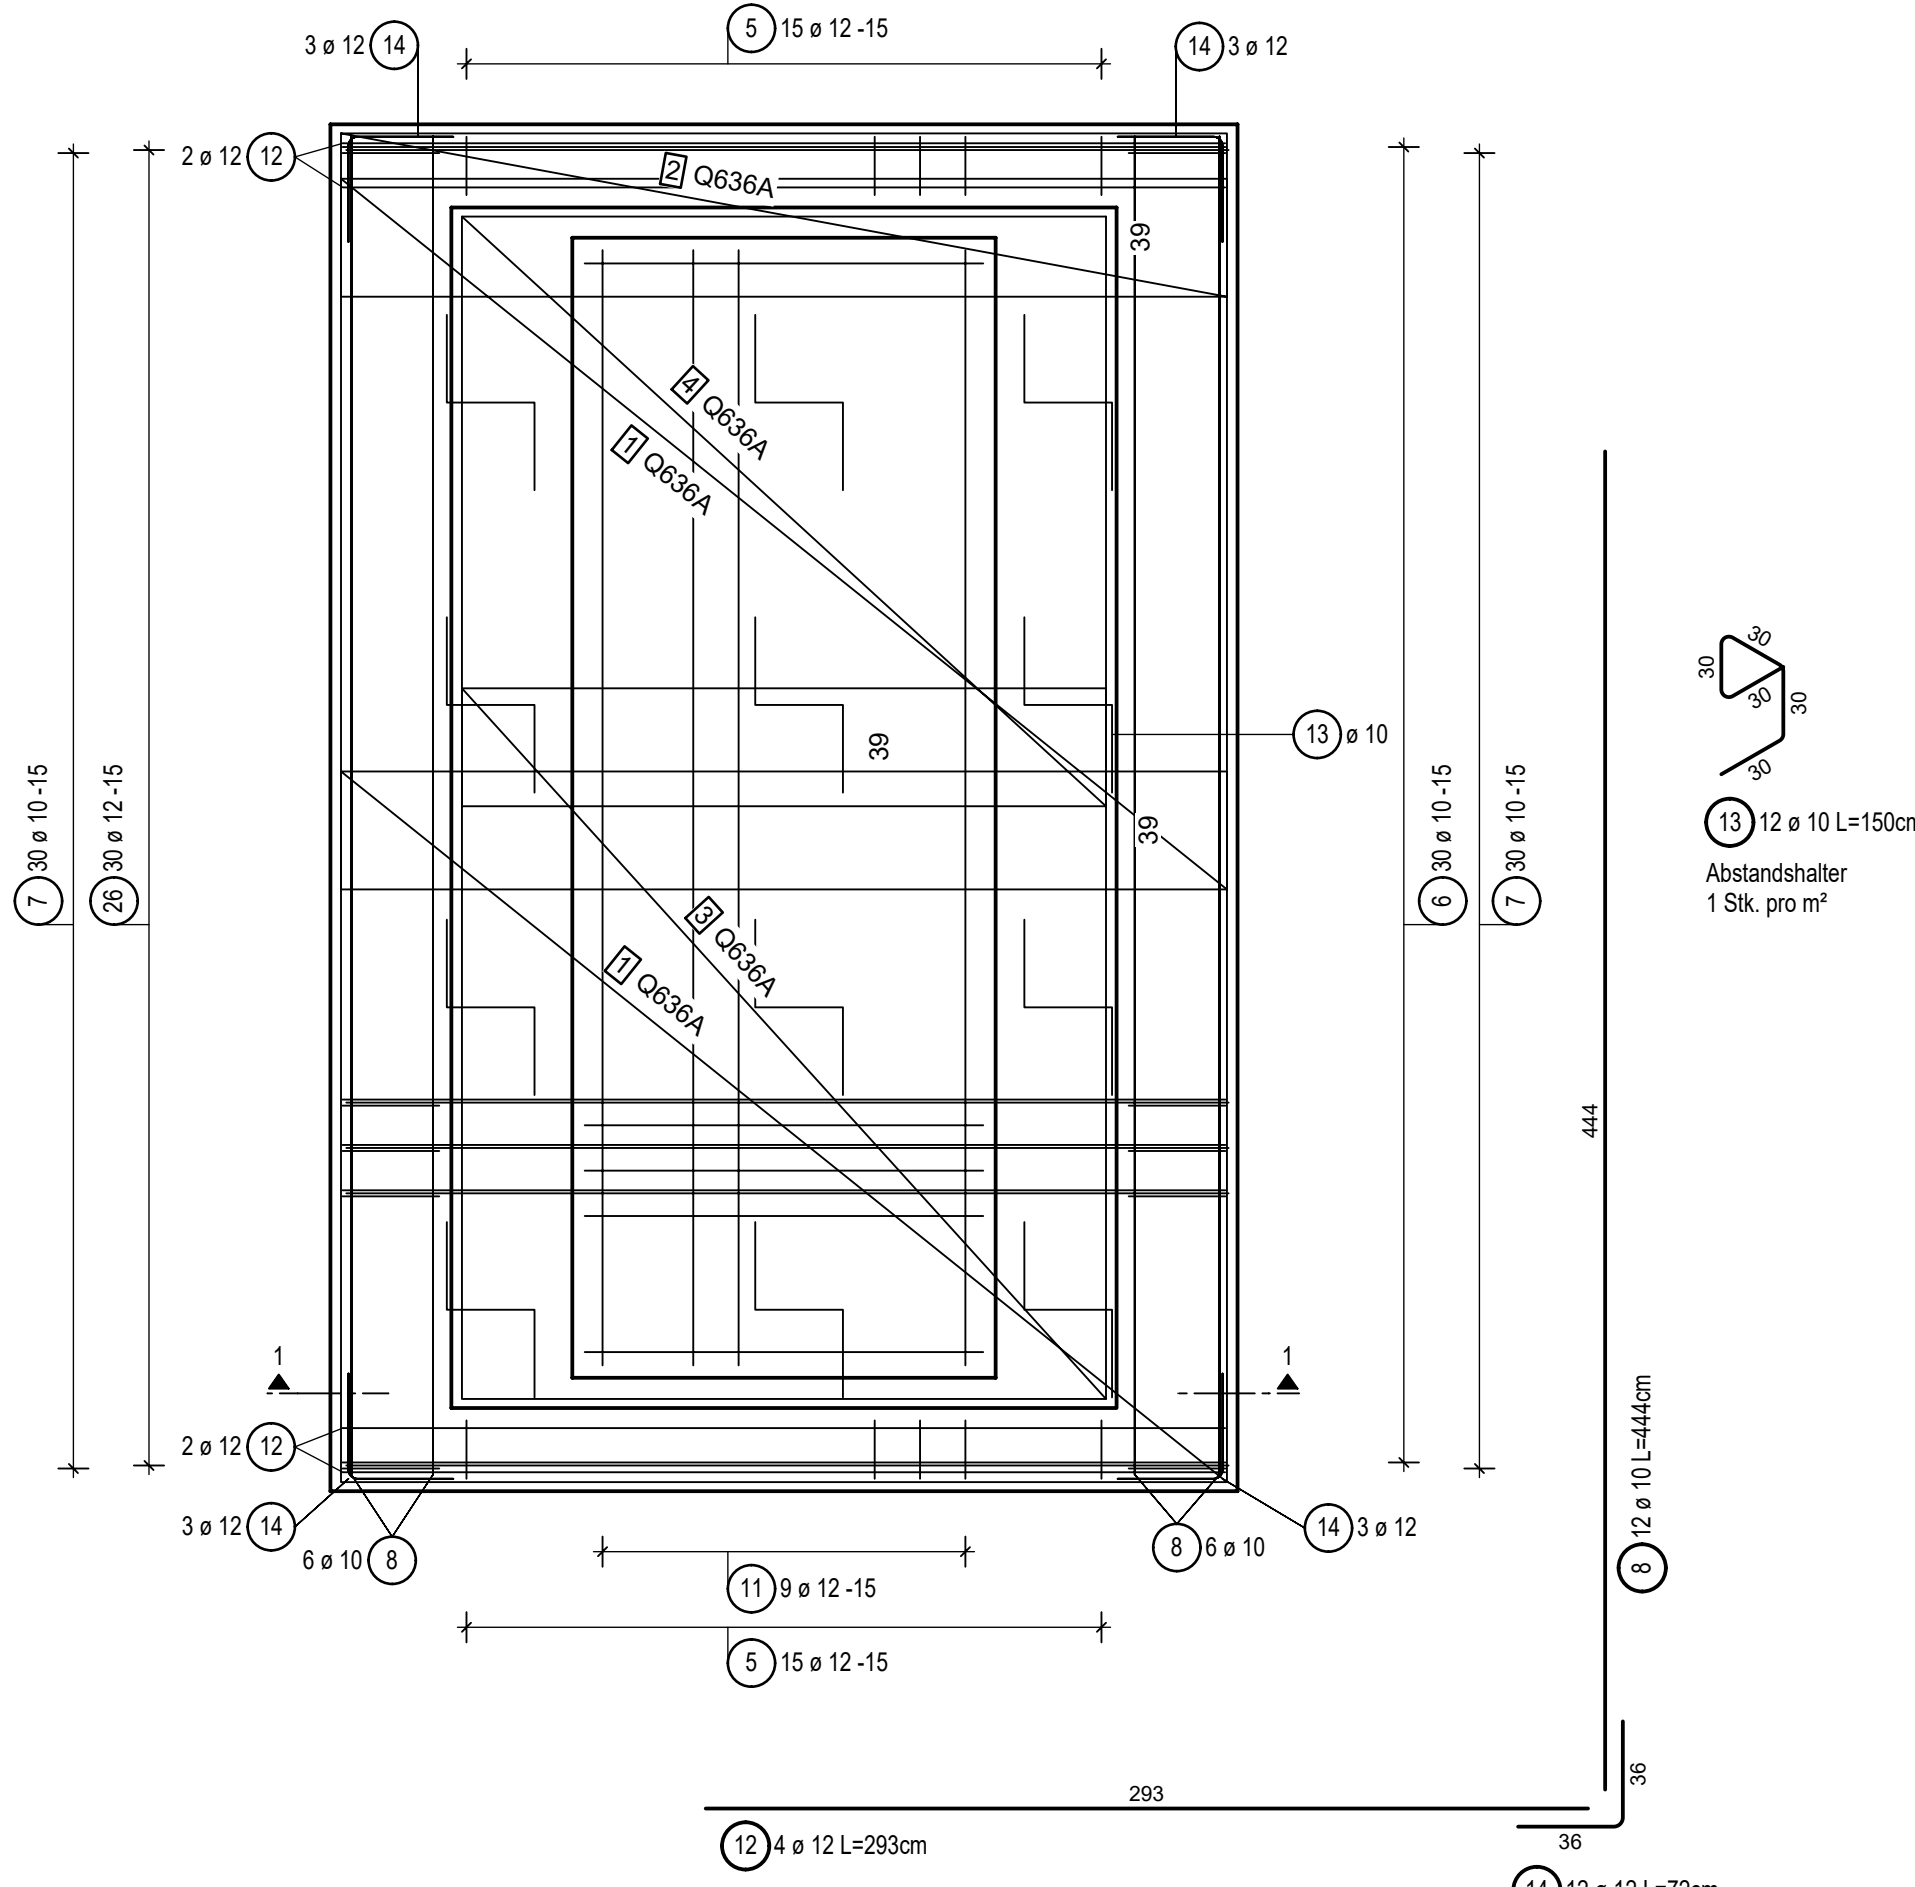


Schnitt 1 - 1

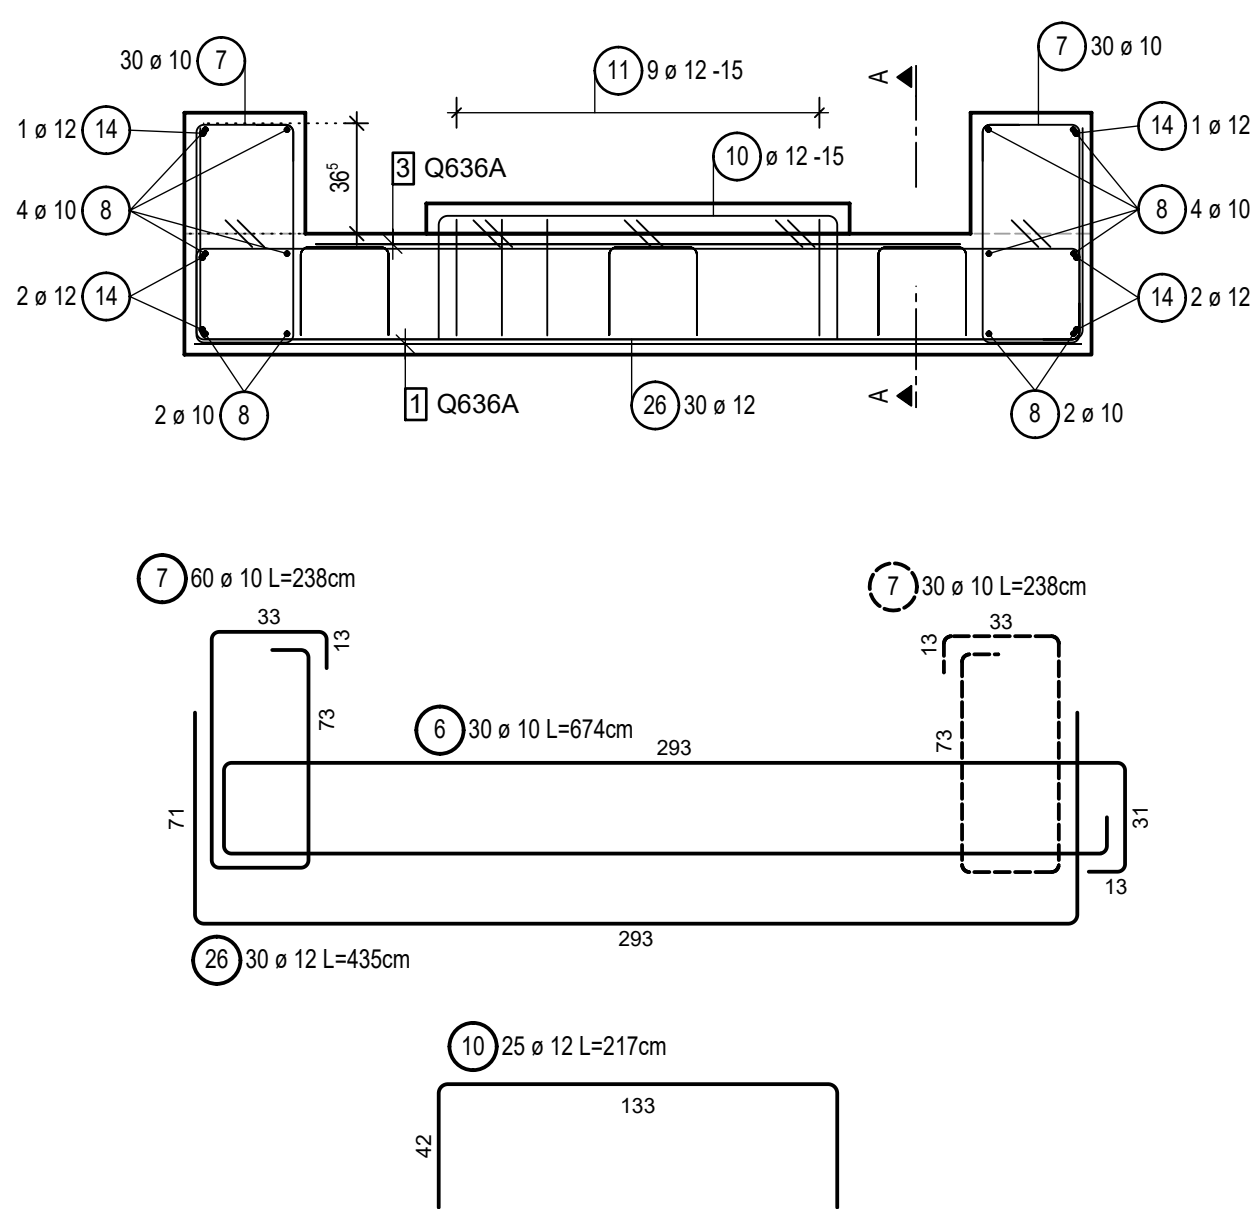


Schnitt A - A

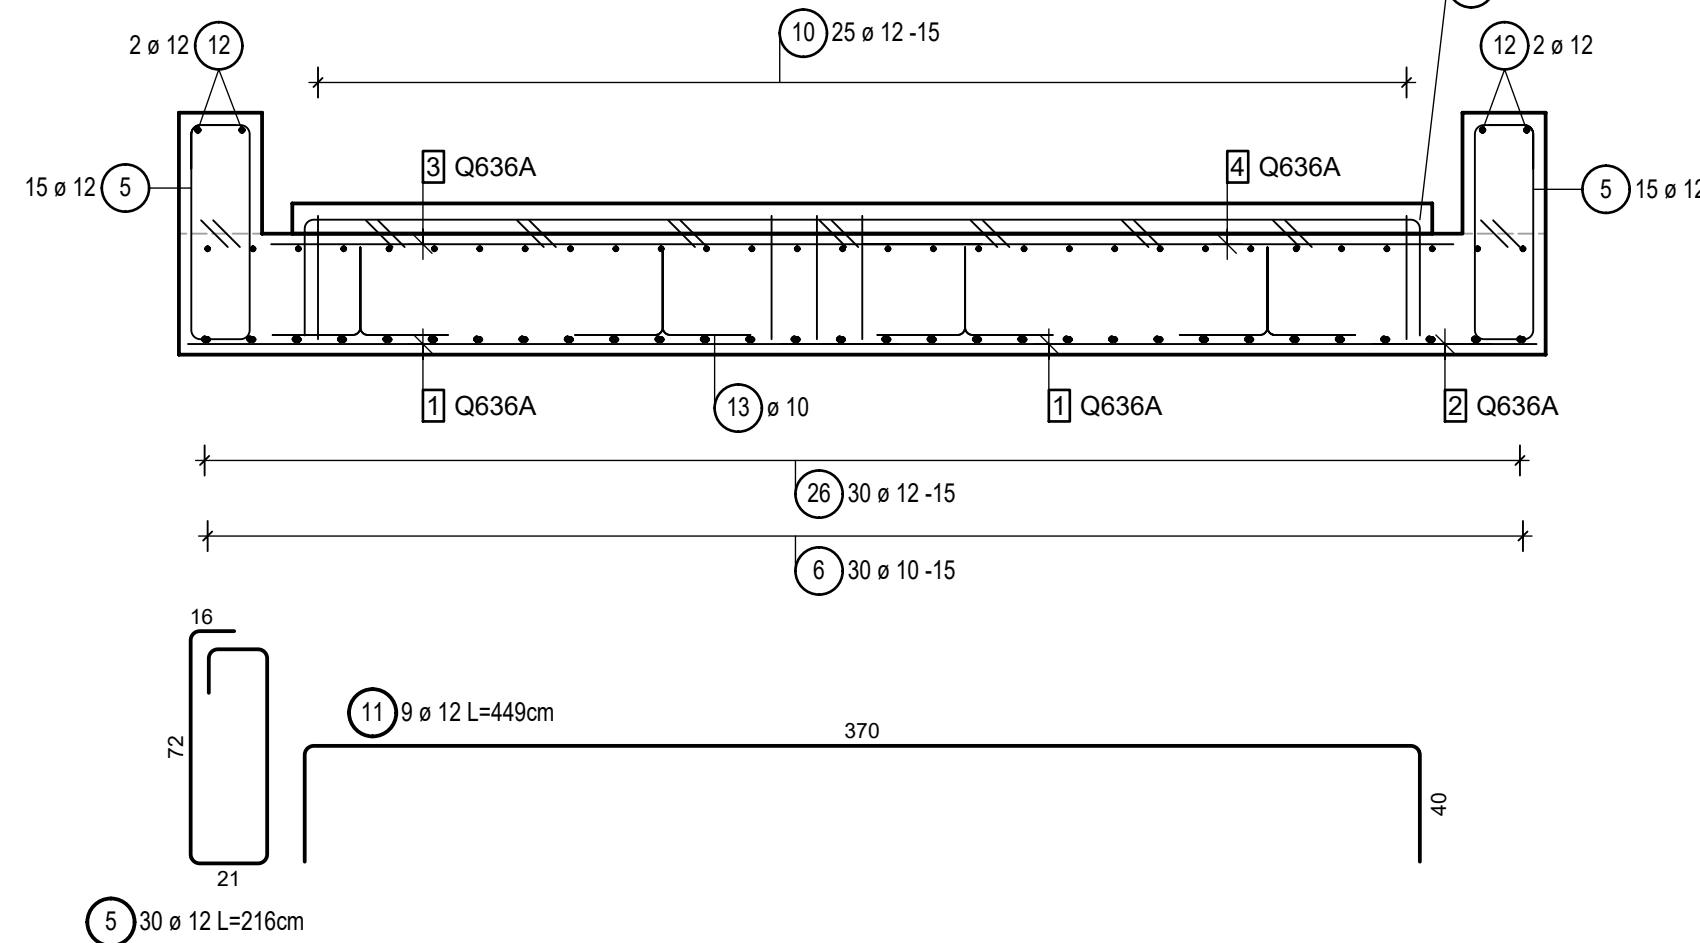


Bewehrung Fundament (FU02.2) Stützen (ST01 ST02 ST03)
Draufsicht

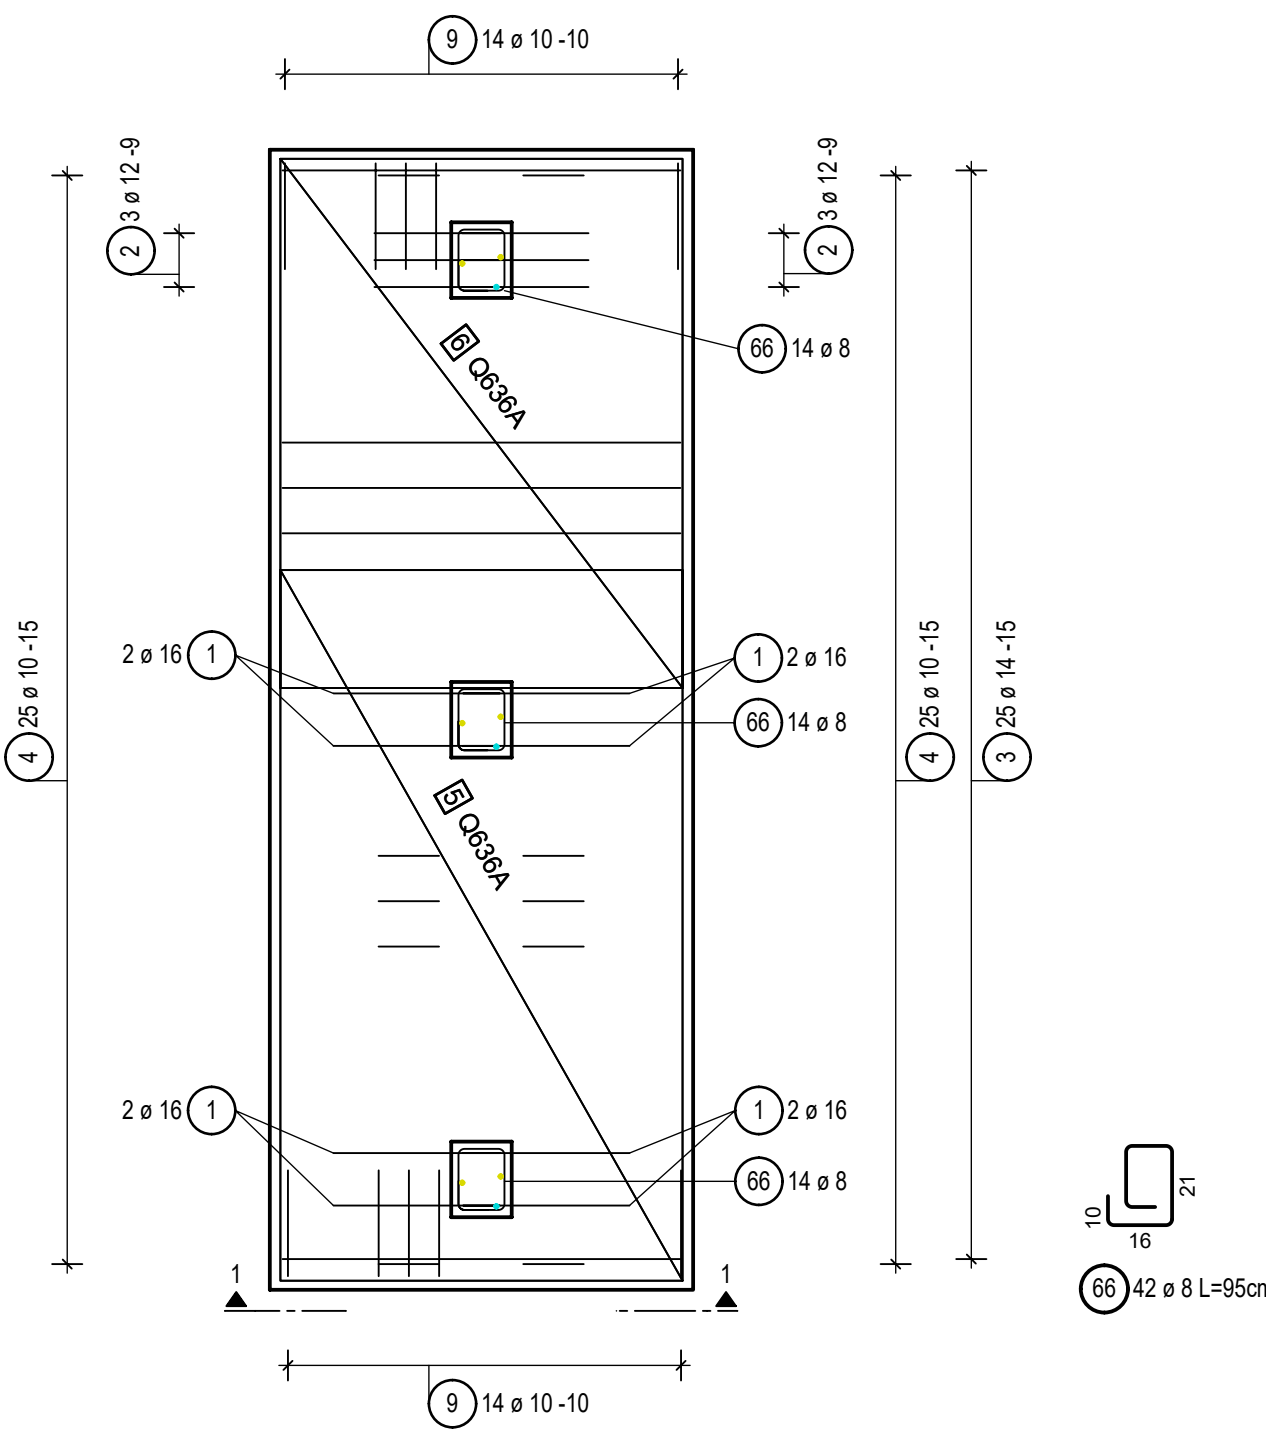

Schnitt 1 - 1

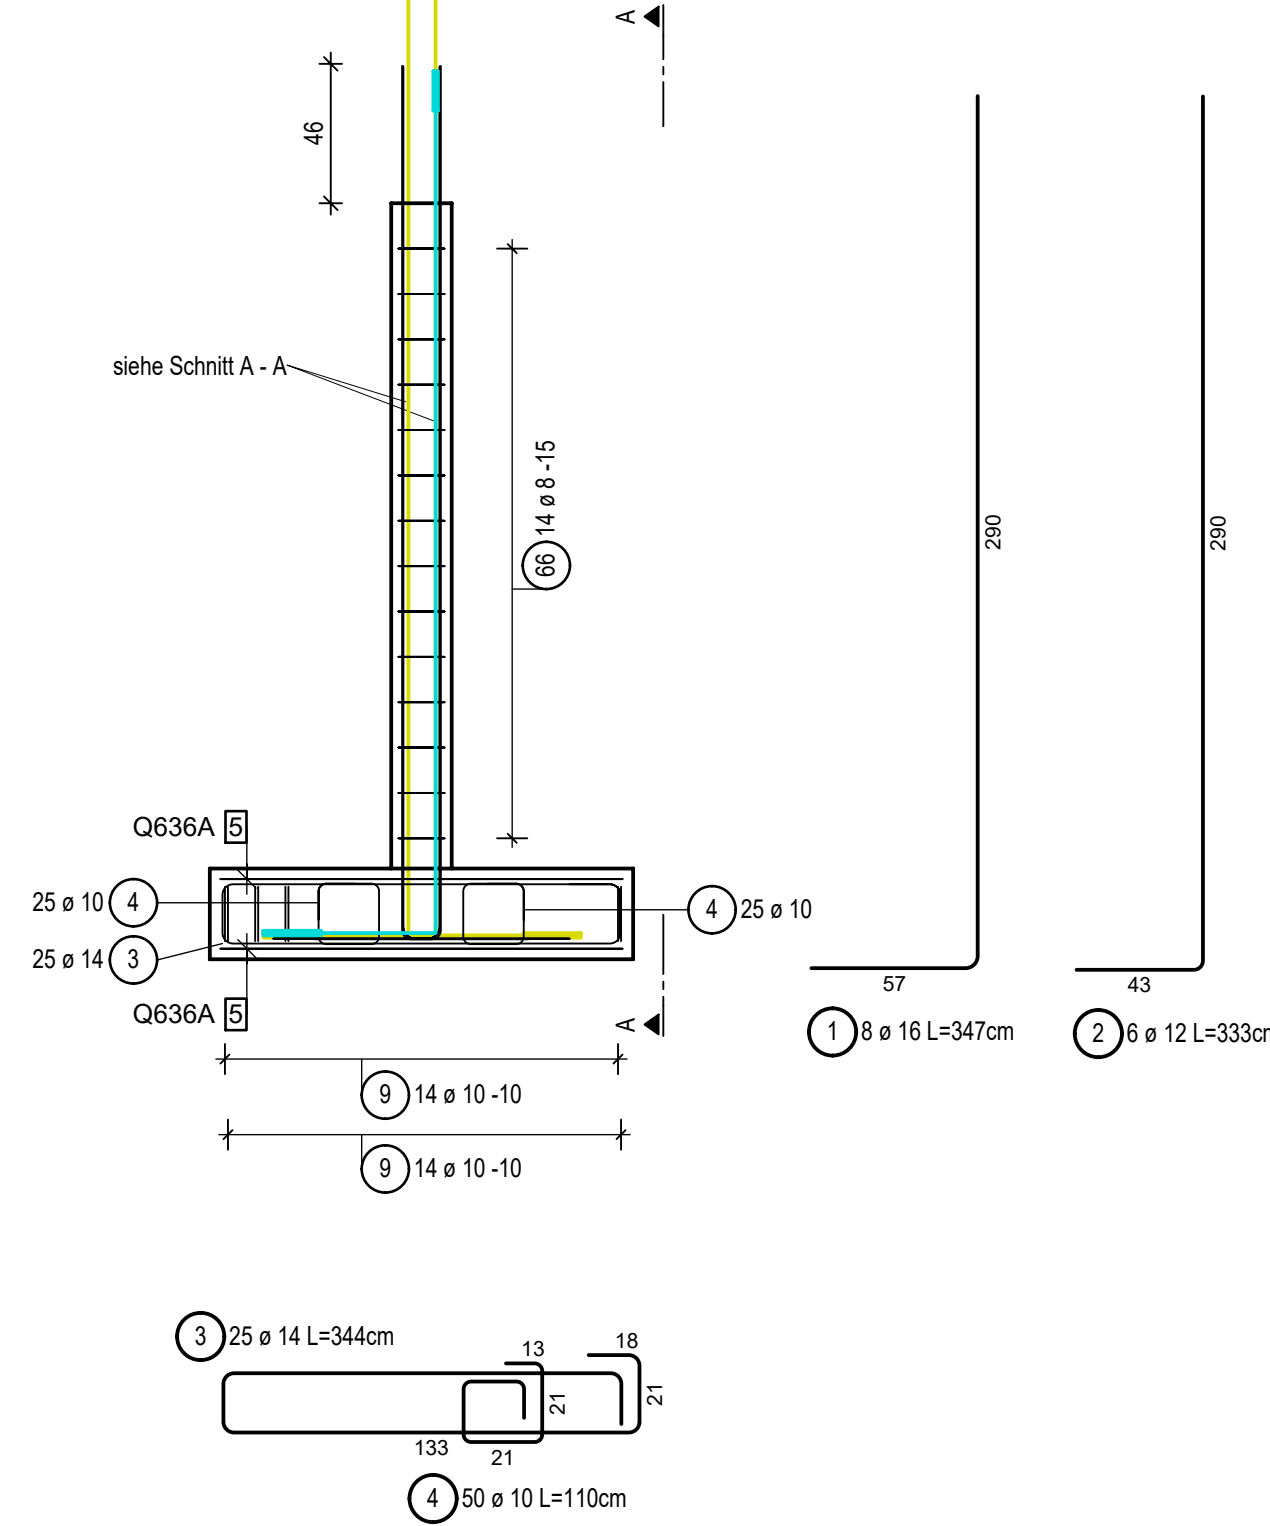

Schnitt A - A

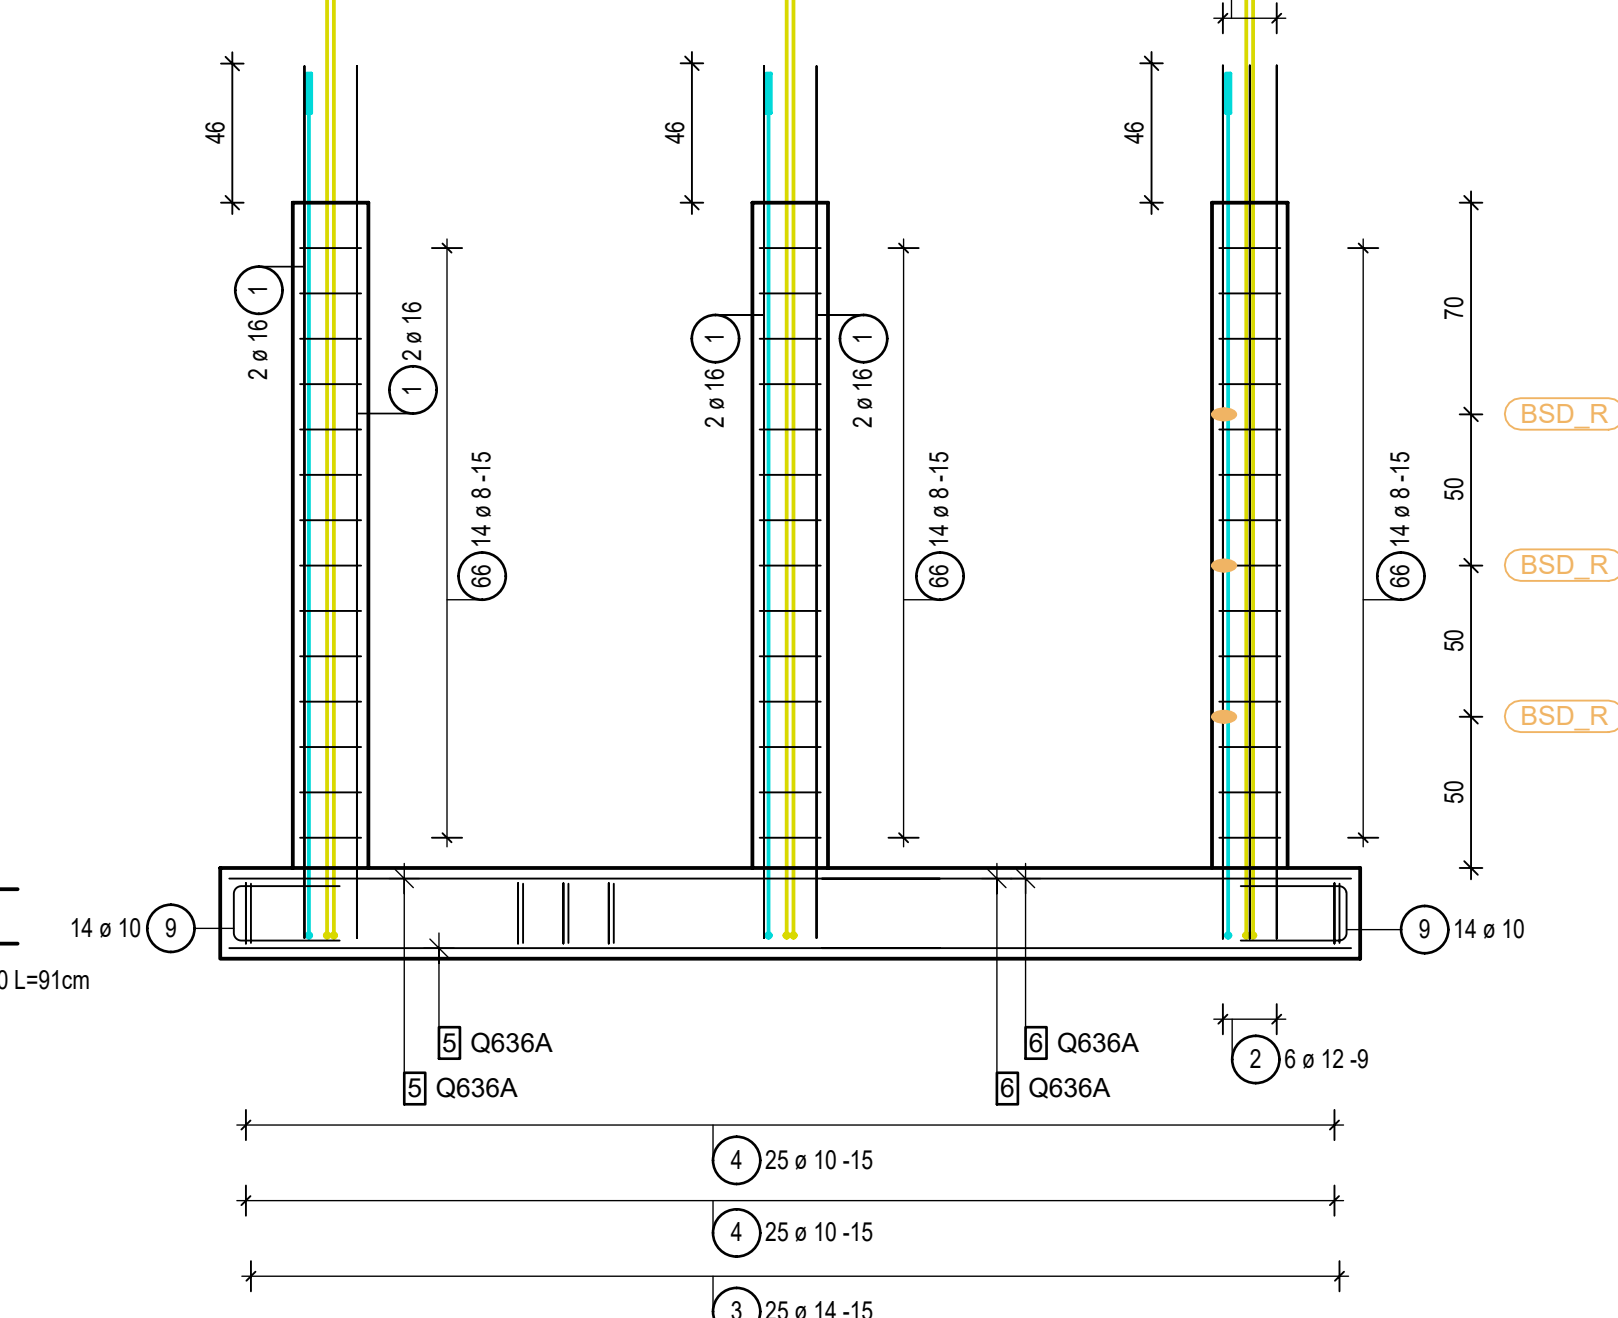

Stabliste - Biegeformen


Pos.	Stück	ø [mm]	Einzel Länge [m]	Bemaßte Biegeform (unmaßstäblich)	Gesamt Länge [m]	Masse [kg]
1	8	16	3.47		27.76	43.86
2	6	12	3.33		19.98	17.74
3	25	14	3.44		86.00	104.06
4	50	10	1.10		55.00	33.94
5	30	12	2.16		64.80	57.54
6	30	10	6.74		202.20	124.76
7	60	10	2.38		142.80	88.11
8	12	10	4.44		53.28	32.87
9	28	10	0.91		25.48	15.72
10	25	12	2.17		54.25	48.17
11	9	12	4.49		40.41	35.88
12	4	12	2.93		11.72	10.41
13	12	10	1.50		18.00	11.11
14	12	12	0.72		8.64	7.67
26	30	12	4.35		130.50	115.88
66	42	8	0.95		39.90	15.76
Gesamtmasse :						763.49

Mattenstahlste

Pos.	Stück	Mattenbez.	Länge [m]	Breite [m]	Gewicht [kg]
1	2	Q636A	2.930	2.350	128.92
2	1	Q636A	2.930	0.540	14.81
3	1	Q636A	2.130	2.350	46.86
4	1	Q636A	2.130	1.960	38.88
5	2	Q636A	1.330	2.350	58.52
6	2	Q636A	1.330	1.750	43.58

Gesamtgewicht: 331.57

Matten- Schneideskizzen

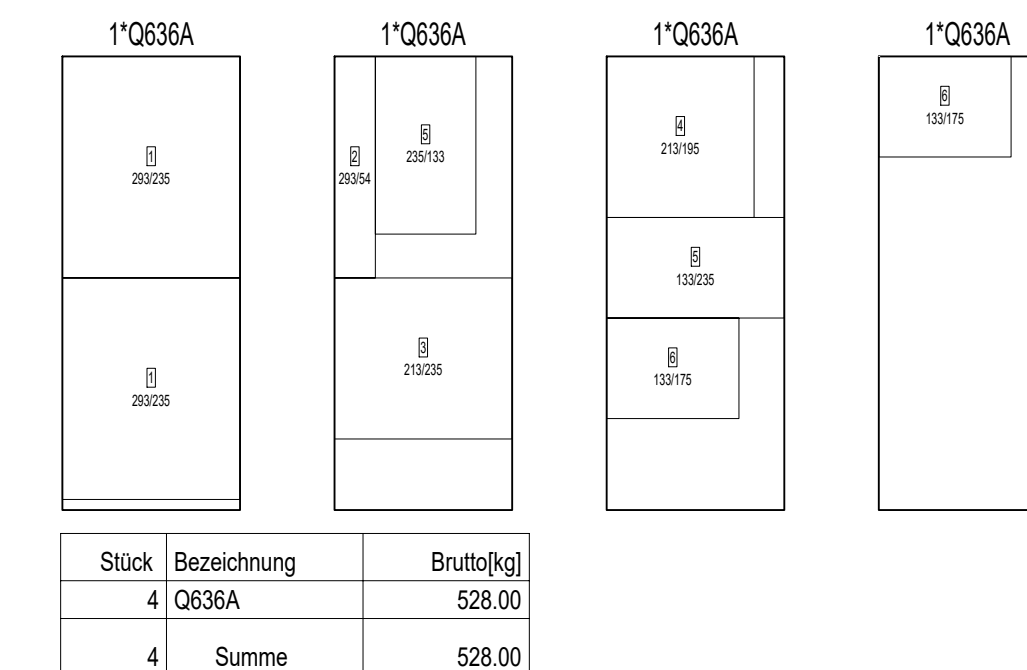

Einbauteile

Pos.	Anzahl [Stk]	Bezeichnung
BSD_R	3	Stahldehnung (Redundanz)
DFOS 42	1	EpiloxSensor 3.0 m.R. UA/K2 C2+0.19m; A+3.50m; C1+0.13m; P1+3.50m
DFOS 43	1	EpiloxSensor 3.0 m.R. UA/K2 C2+0.19m; A+3.50m; C1+0.13m; P1+4.20m
DFOS 44	1	EpiloxSensor 3.0 m.R. UA/K2 C2+0.19m; A+3.50m; C1+0.13m; P1+2.10m
DFOS 45	1	EpiloxSensor 3.0 m.R. UA/K2 C2+0.19m; A+3.50m; C1+0.13m; P1+3.00m
DFOS 46	1	EpiloxSensor 3.0 m.R. UA/K2 C2+0.19m; A+3.50m; C1+0.13m; P1+3.50m
DFOS 47	1	EpiloxSensor 3.0 m.R. UA/K2 C2+0.19m; A+3.50m; C1+0.13m; P1+3.75m
DFOS 48	1	EpiloxSensor 1.0 o.R. UA/K2 C2+0.19m; A+3.10m; C1+0.13m; P1+3.35m
DFOS 49	1	EpiloxSensor 1.0 o.R. UA/K2 C2+0.19m; A+3.10m; C1+0.13m; P1+3.35m
DFOS 50	1	EpiloxSensor 1.0 o.R. UA/K2 C2+0.19m; A+3.10m; C1+0.13m; P1+3.75m
E006	4	PVC-Rohr DN100, l=400mm
E009	4	Montagerohr, KG-Rohr DN150, l=400mm
ES001	1	Großflächengleitfolie Typ RUKK 3,77m x 1,40m

siehe Schalplan

BAUSTOFFANGABEN (Planspezifisch)

Bestelle	Expositionsklassen	Stütze	Stütze	Stütze	Stütze
Fundamente (FU02.1) (FU02.2)	XC2	C30/37			3.5cm
Stützen (ST01) (ST02) (ST03)	XC4	C50/60			2.0cm
Bereiche mit höherer Betonfestigkeiten beachten					
Betonstahl : BSt 500 MB) BSt 500 SB)					
Standardklasse : 1,0/ 1,0 cm					
f					
e					
d					
c					
b	12.09.2023	Collin	Sensorik		
a	11.07.2023	Graf	Freigabe		
INDEX	DATUM	GEZ.			

Werkplanung

Bauherr:	Intern	gezeichnet:	Collin
Datum:	12.09.2023	Unterschrift:	
Darstellung:	IDA-KI Errichtung einer 3-Feld-Brücke	Plan-Nr.	1 : 25
Planbezeichnung	Bewehrungsplan Unterbauten Achse (20)	Planbezeichnung	BP-UB20