



Bewehrungsplan Unterbauten Achse 30


Schalung
Draufsicht

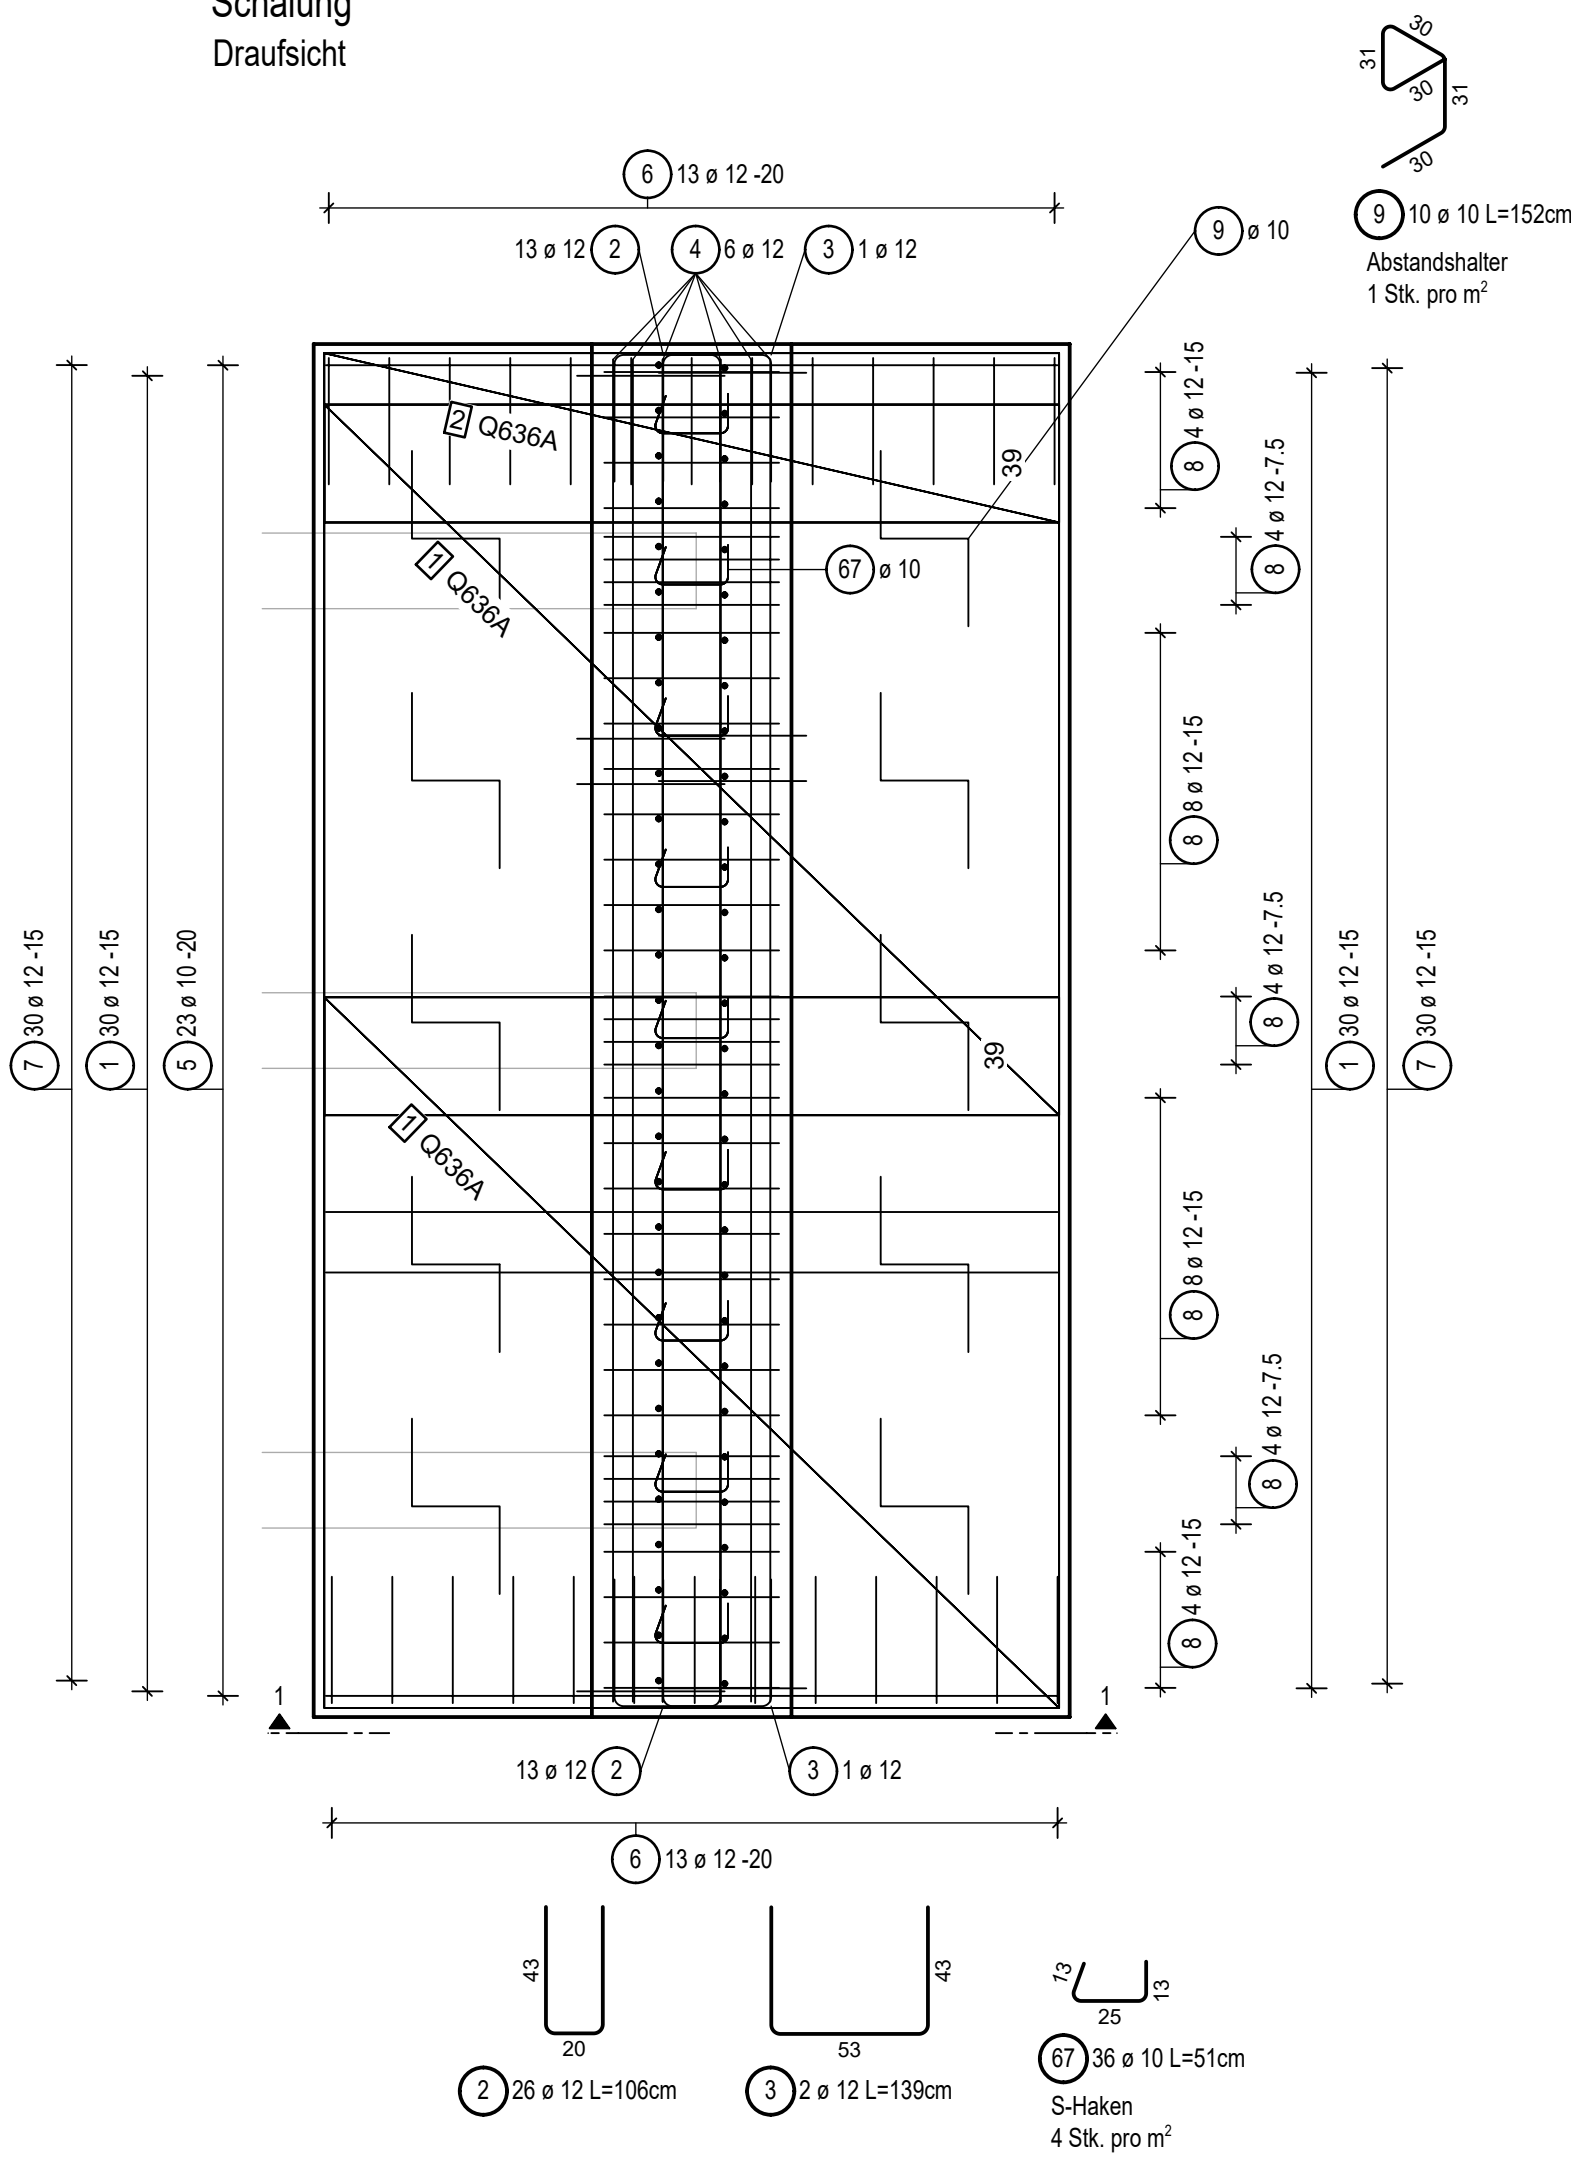


Schnitt 1 - 1

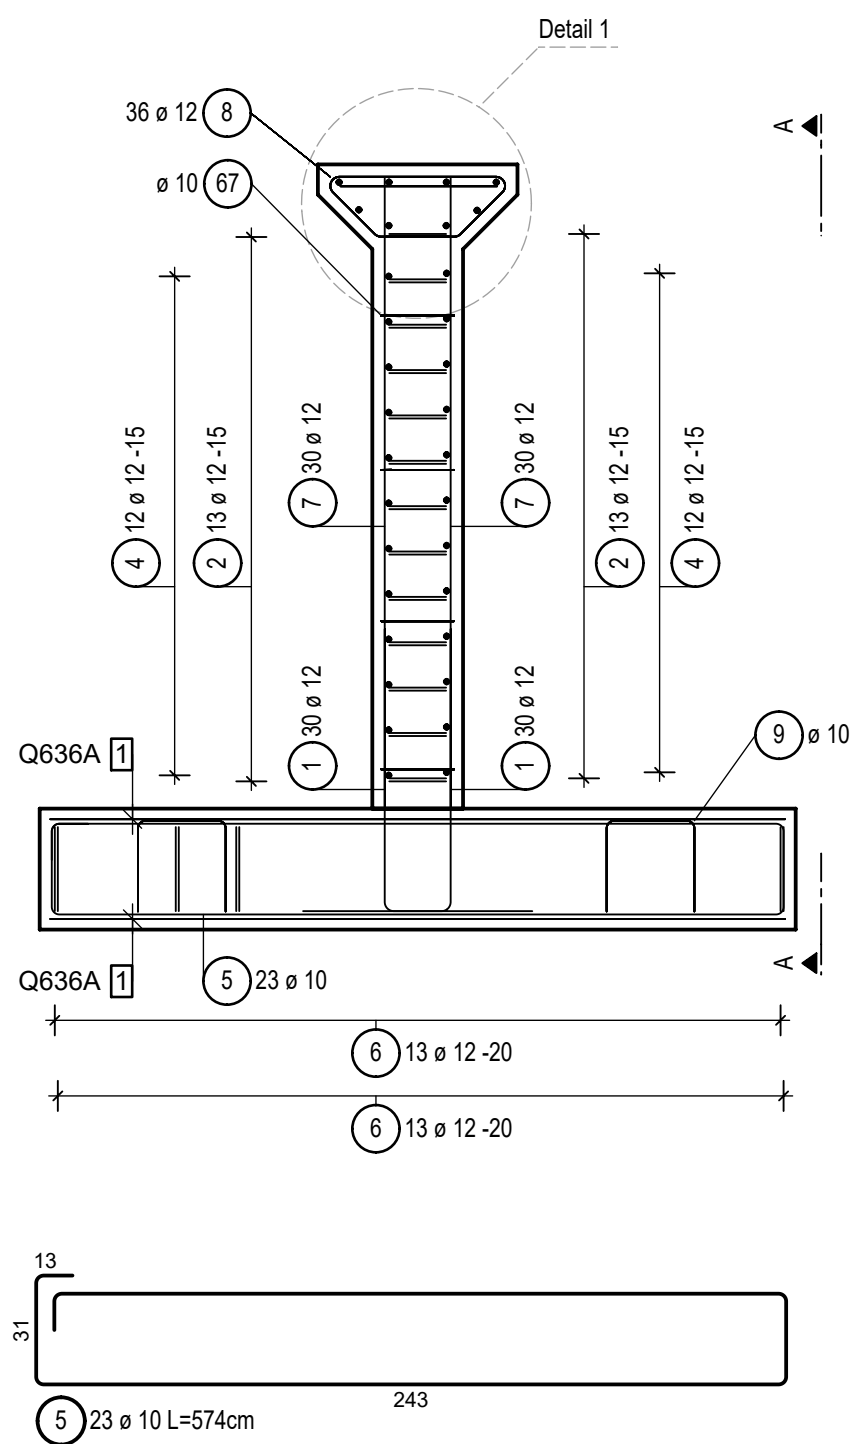

Detail 1
M1:10

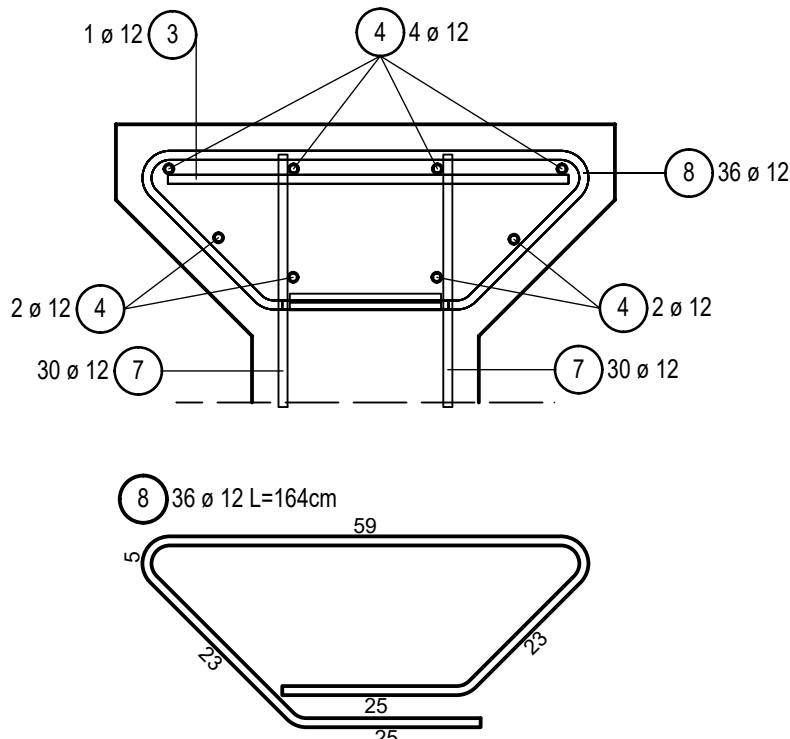

Schnitt A - A

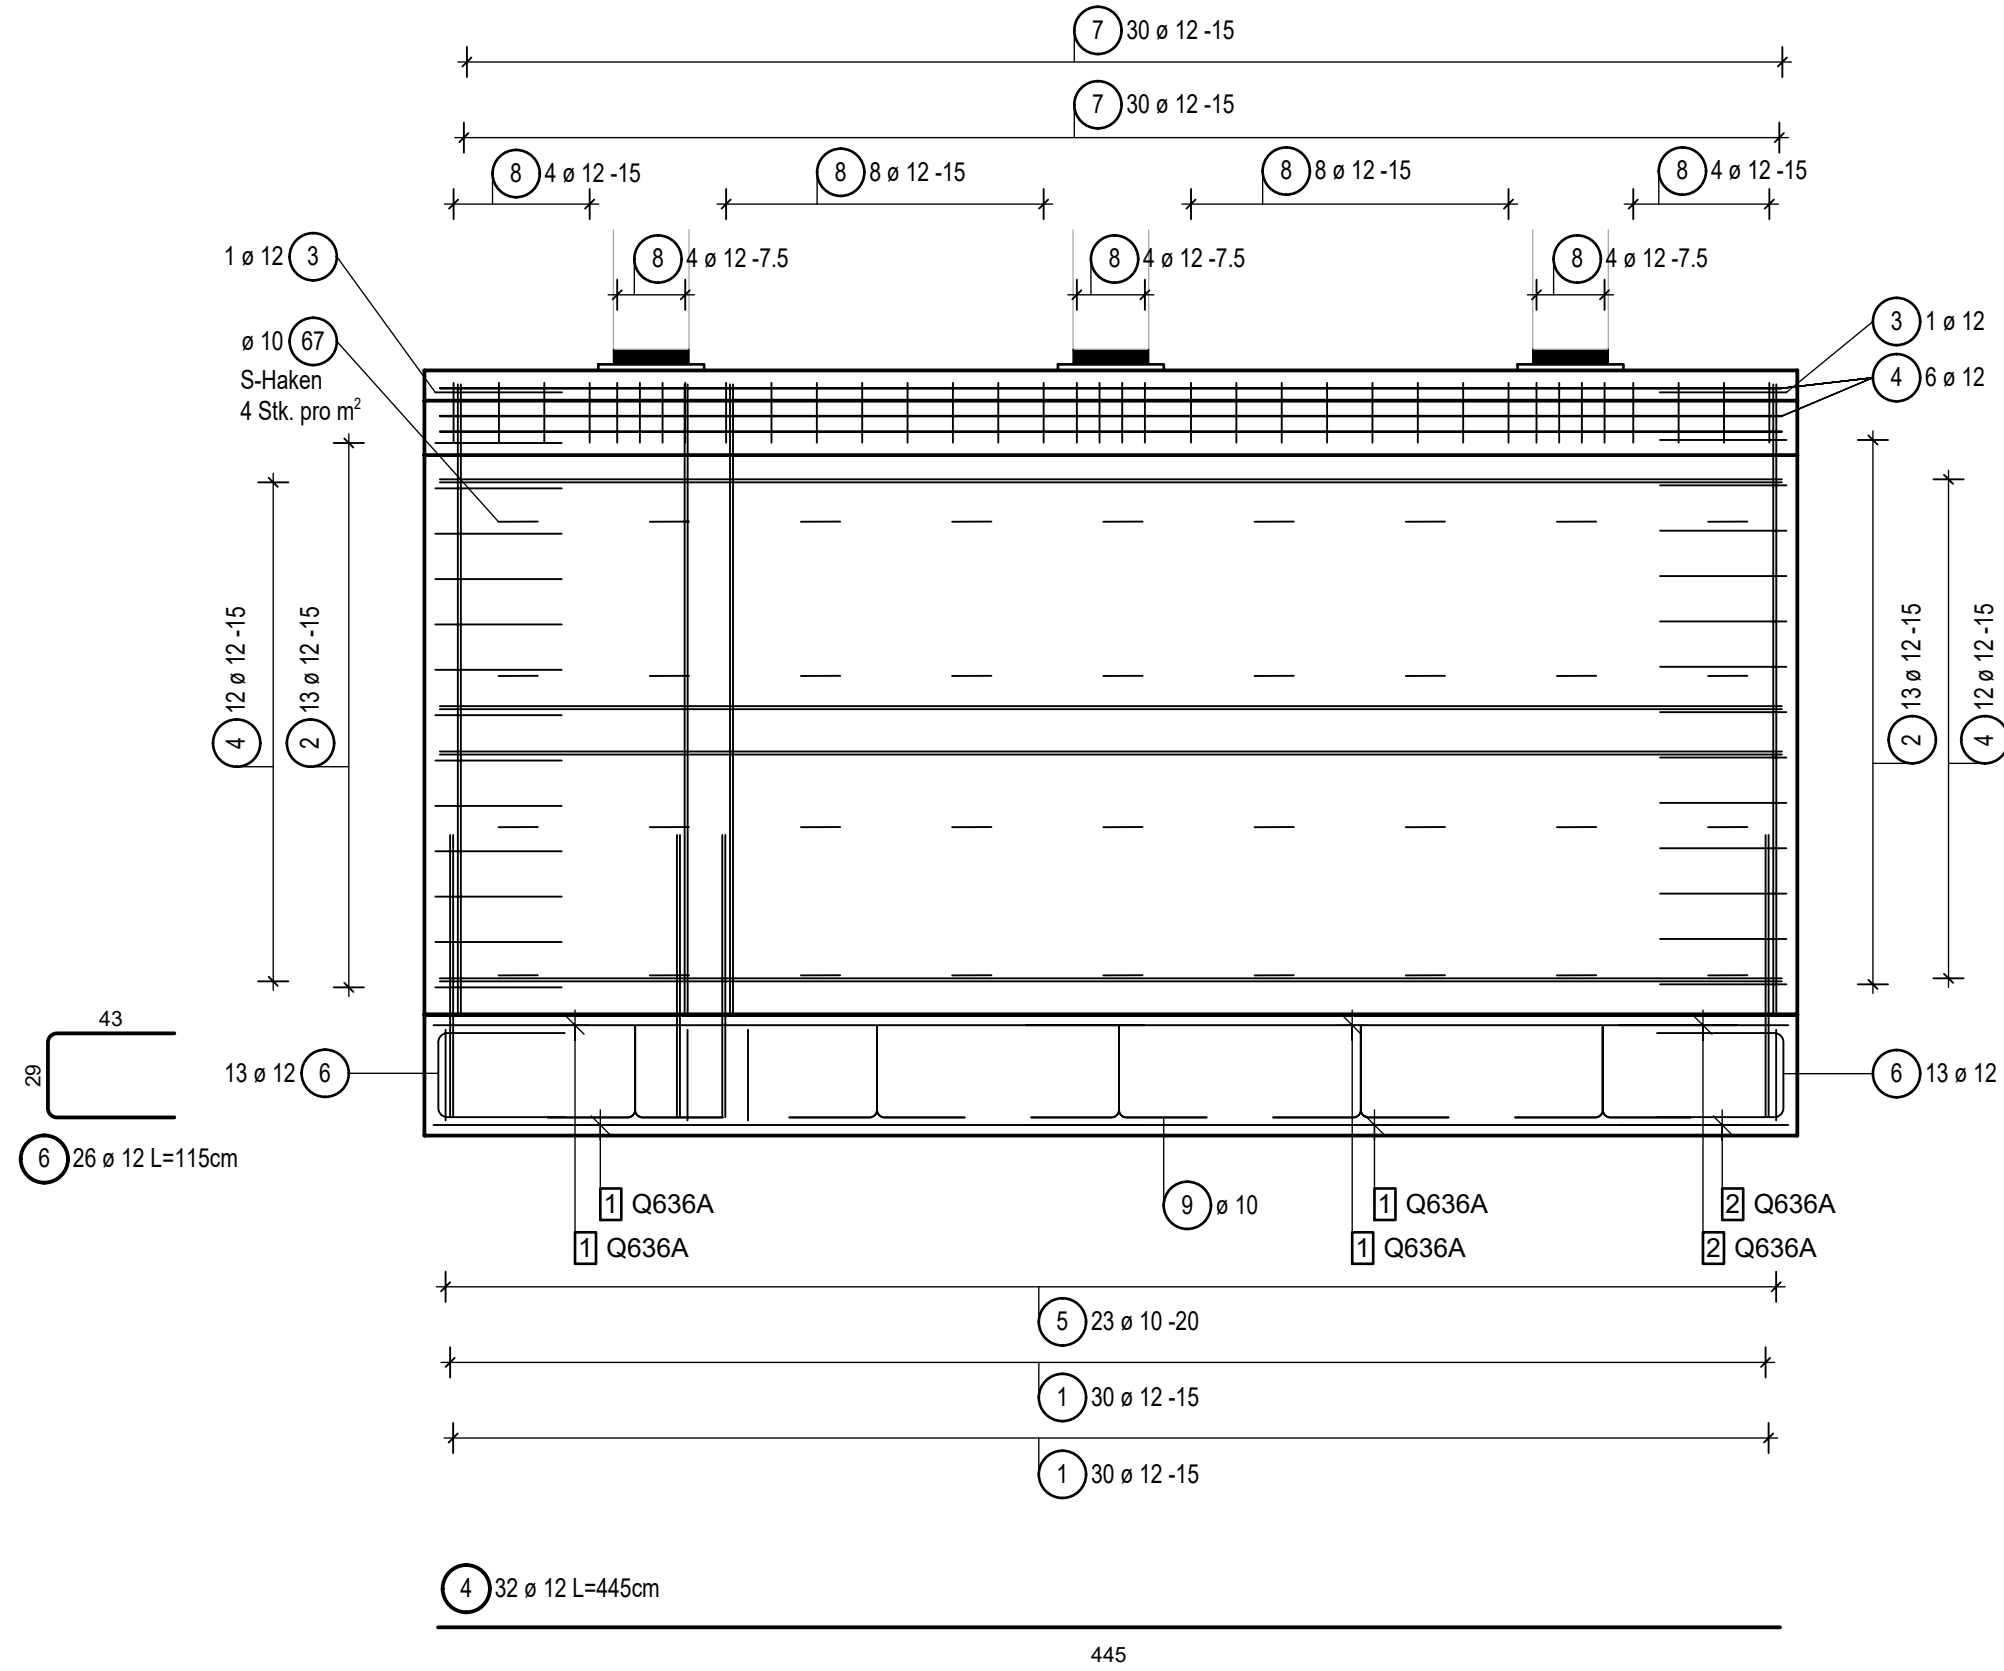


Mattenstahlliste

Pos.	Stück	Mattenbez.	Länge [m]	Breite [m]	Gewicht [kg]
1	4	Q636A	2.430	2.350	213.84
2	2	Q636A	2.430	0.560	25.48

Gesamtgewicht: 239.32

Matten- Schneideskizze

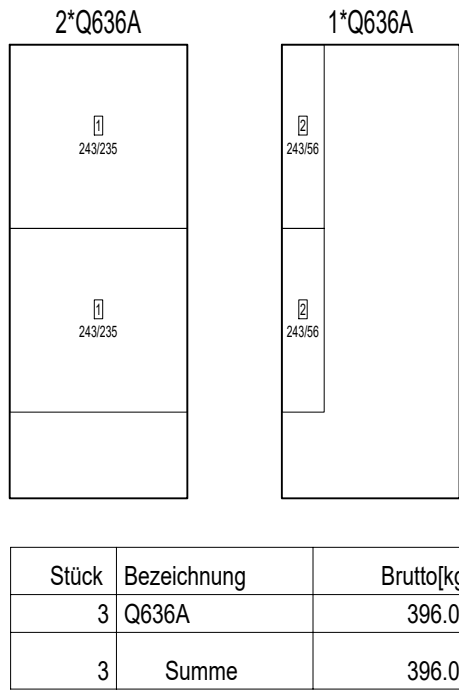

Stabliste - Biegeformen

Pos.	Stck	ø [mm]	Einzel Länge [m]	Bemaßte Biegeform (unmaßstäblich)	Gesamt Länge [m]	Masse [kg]
1	60	12	1.45		87.00	77.26
2	26	12	1.06		27.56	24.47
3	2	12	1.39		2.78	2.47
4	32	12	4.45		142.40	126.45
5	23	10	5.74		132.02	81.46
6	26	12	1.15		29.90	26.55
7	60	12	2.09		125.40	111.36
8	36	12	1.64		59.04	52.43
9	10	10	1.52		15.20	9.38
67	36	10	0.51		18.36	11.33

Gesamtmasse : 523.15

Zu klären:
Pos.8 ausreichend im Auflagerbereichbereich
der Träger Feld 3?
siehe Statik

BAUSTOFFANGABEN (Planspezifisch)

Bauteile	Expositionsklassen	Beton	ω _c	min c	nom c
Fundament (FU03)	XC2	C30/37			3,5cm
Pfeiler (PF01)	XC4	C30/37			4,0cm
Bereiche mit höheren Betonfestigkeiten beachten					
Betonstahl : BSt 500 M(B) Standardfase: 1,0/ 1,0 cm					
BSt 500 S(B)					
f					
e					
d					
c					
b					
a	11.07.2023	Graf	Freigabe		
INDEX	DATUM	GEZ.			

Werkplanung

Bauherr:
Intern

Bauvorhaben:

IDA-KI
Errichtung einer 3-Feld-Brücke

Darstellung:

Bewehrungsplan Unterbauten Achse 30

Planung:

Hentschke

Betonfertigteilterwerk Bautzen

Hentschke Bau GmbH

Hoyerswerdaer Straße 42

02625 Bautzen

Tel.: 03591 6703-

Fax: 03591 6703-42

Projekt-Nr.: XXXX-XX

50 - 999 - 035

gezeichnet:

Graf

Datum:

06.07.2023

Unterschrift:

Maßstab:

1 : 25

Plan-Nr.

Planbezeichnung BP-UB30

a