




Schalung
Draufsicht

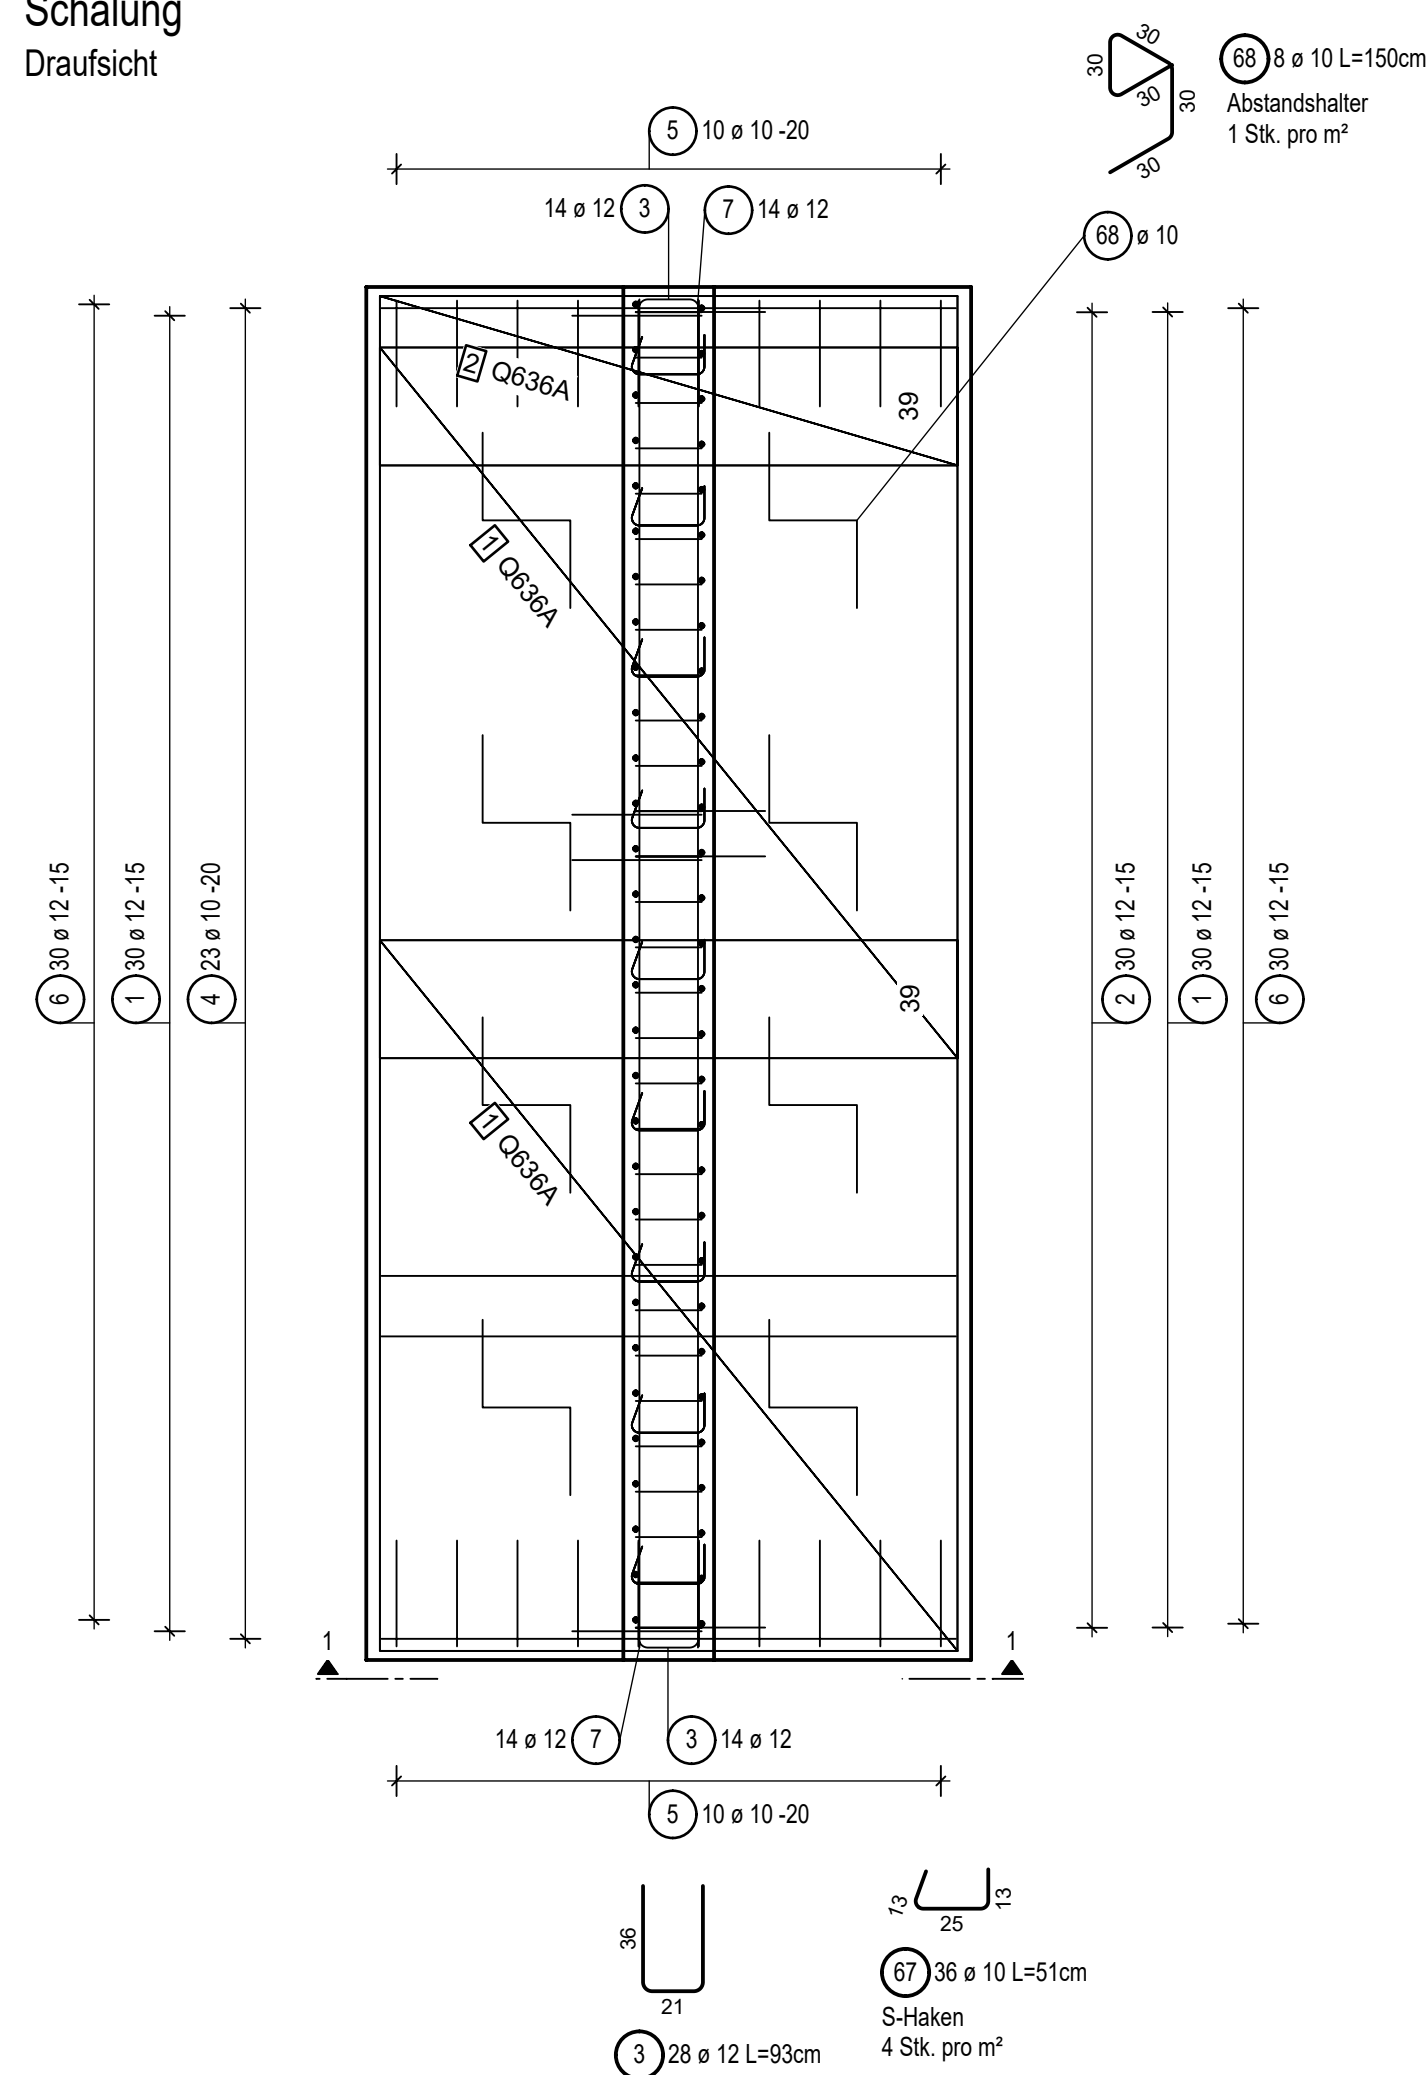

Schnitt 1 - 1

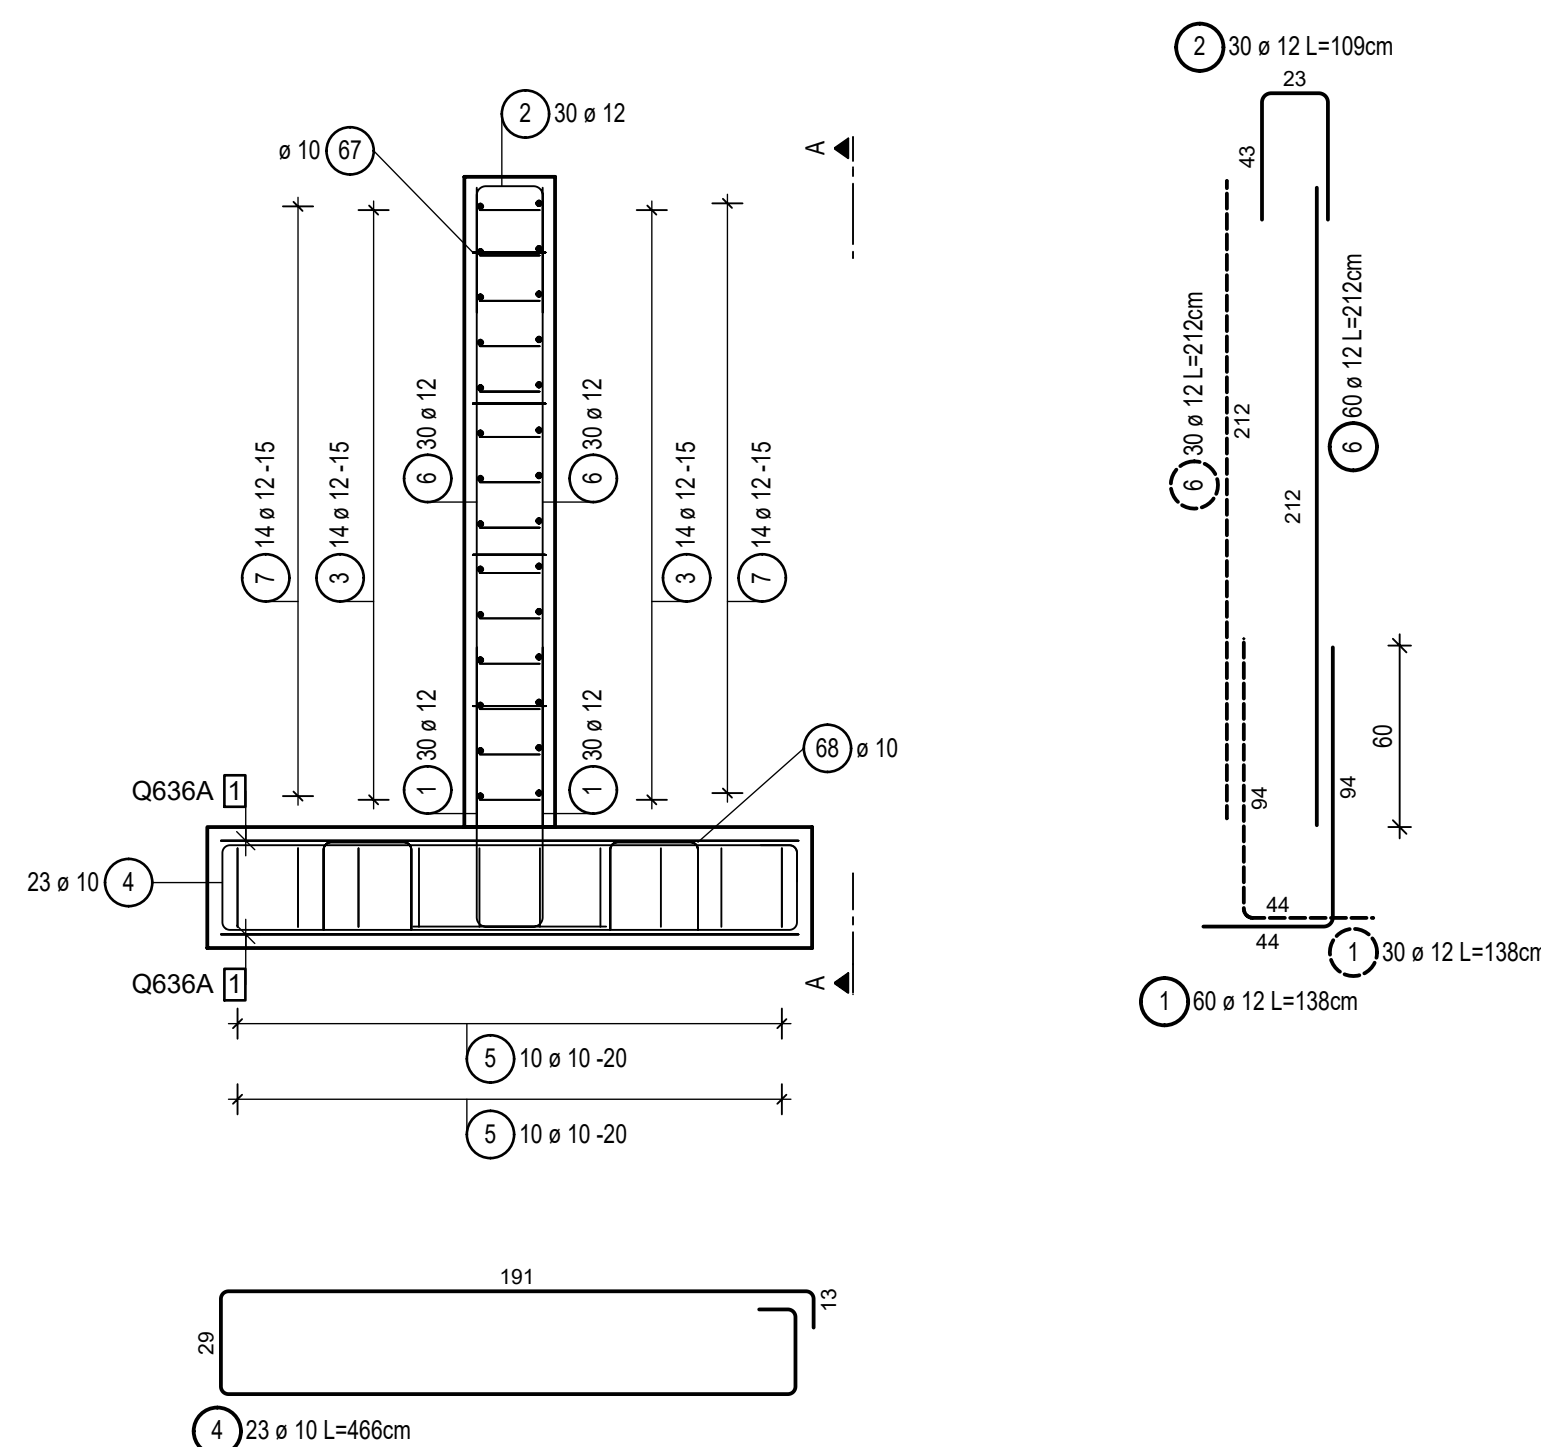

Schnitt A - A

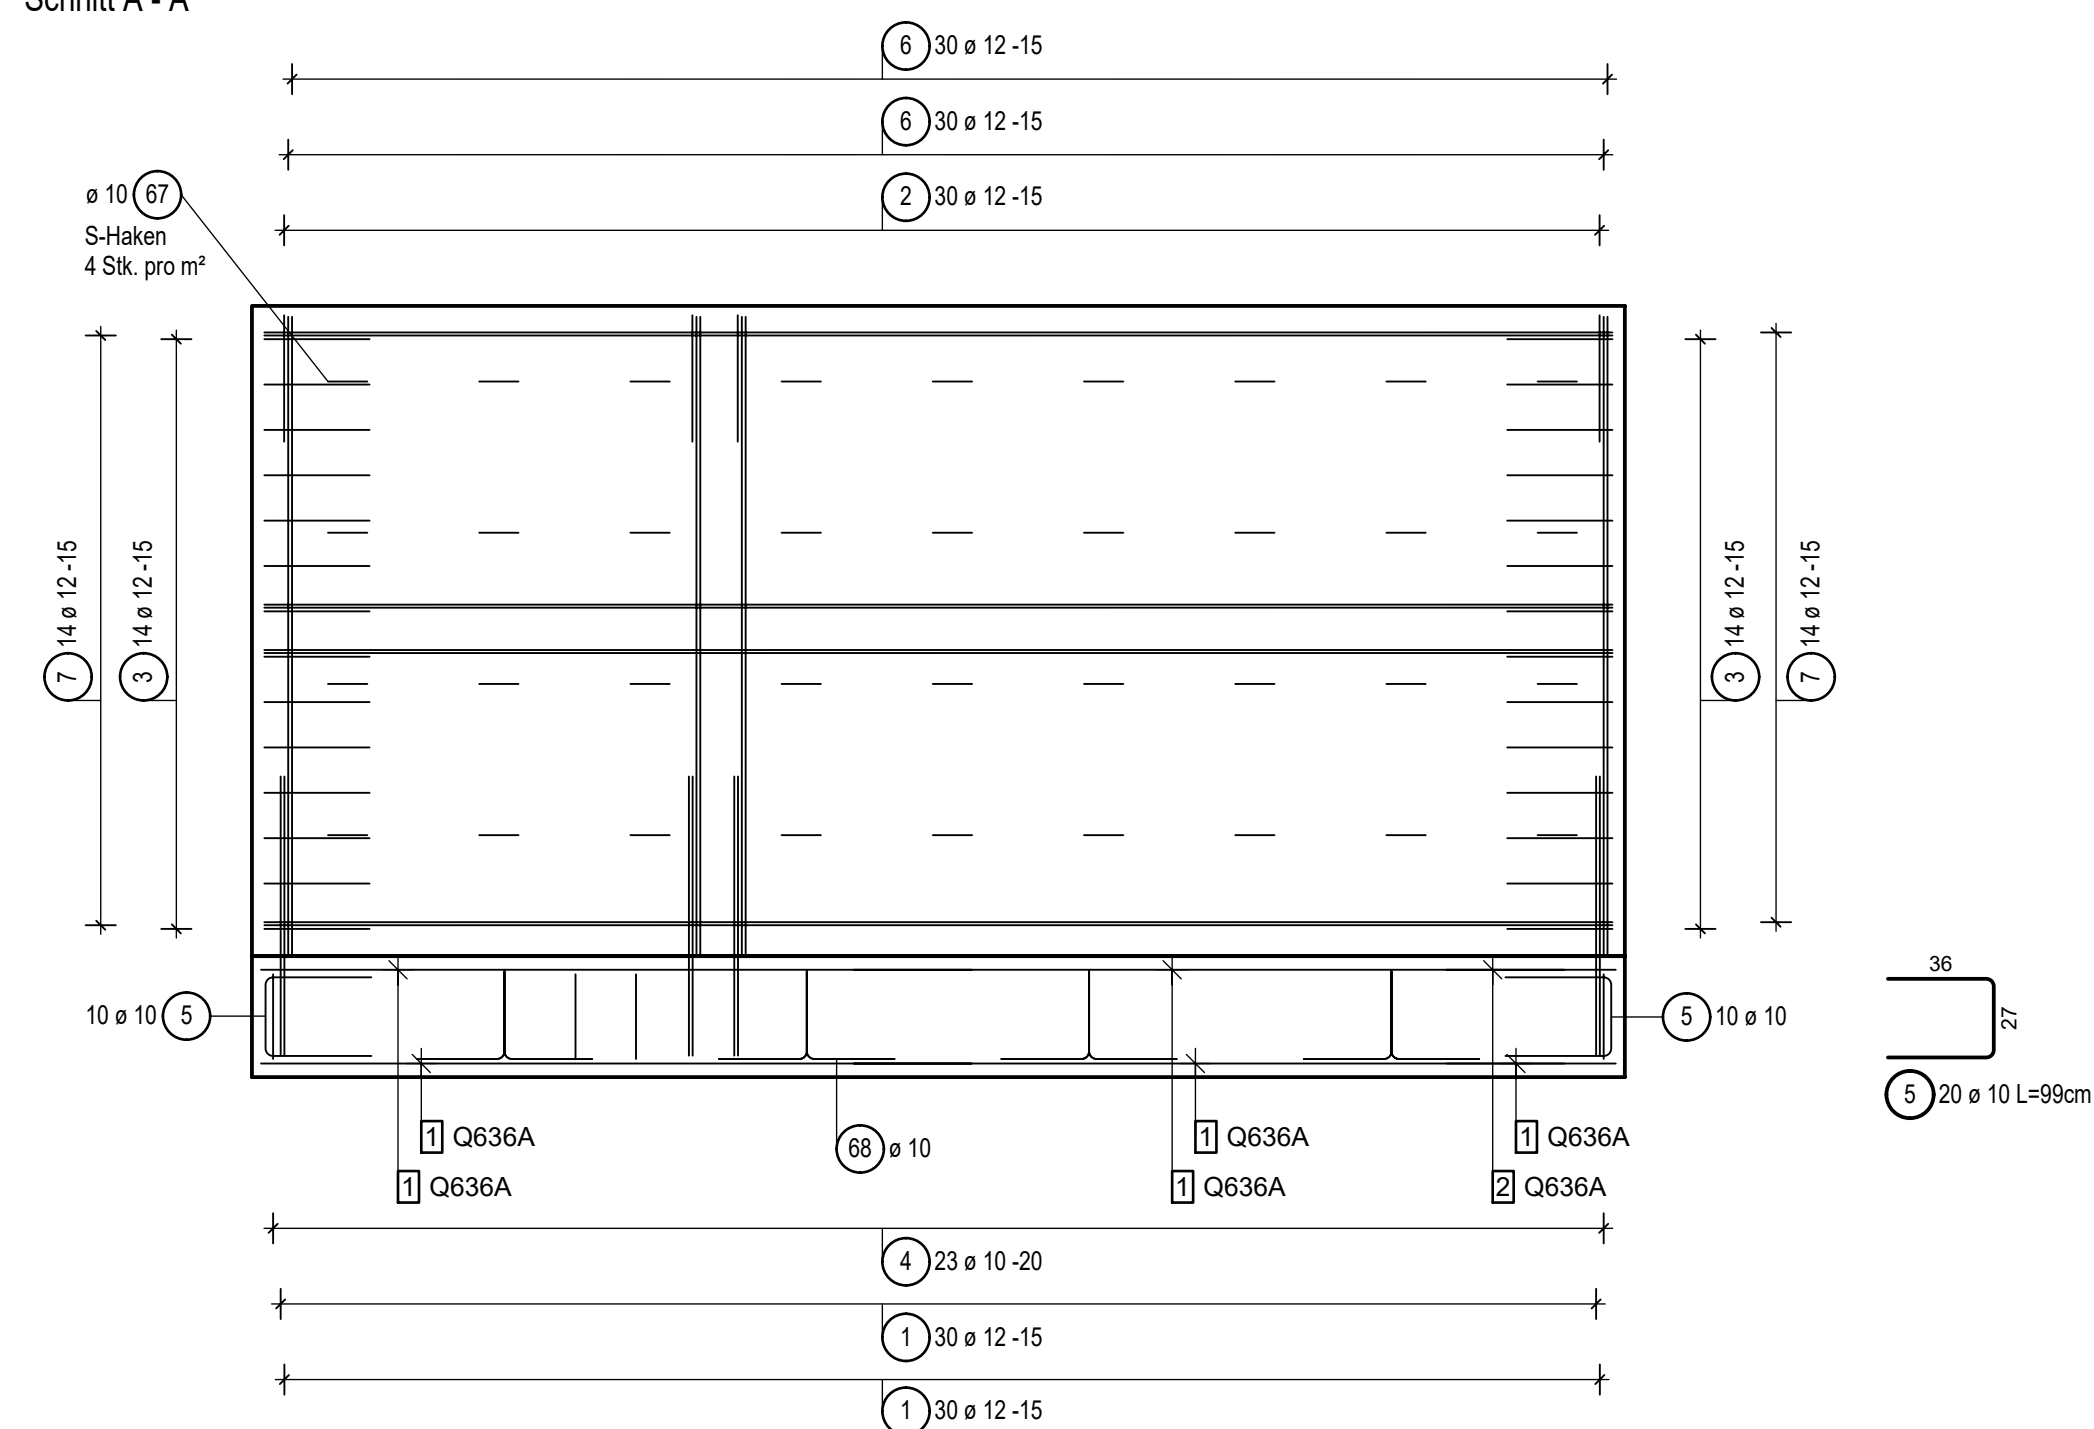

Pos.	Stück	Mattenbez.	Länge [m]	Breite [m]	Gewicht [kg]
1	4	Q636A	1.910	2.350	168.08
2	2	Q636A	1.910	0.560	20.03

Gesamtgewicht: 188.11

Pos.	Stck	ø [mm]	Einzel Länge [m]	Bemaßte Biegeform (unmaßstäblich)	Gesamt Länge [m]	Masse [kg]
1	60	12	1.38		82.80	73.53
2	30	12	1.09		32.70	29.04
3	28	12	0.93		26.04	23.12
4	23	10	4.66		107.18	66.13
5	20	10	0.99		19.80	12.22
6	60	12	2.12		127.20	112.95
7	28	12	4.47		125.16	111.14
67	36	10	0.51		18.36	11.33
68	8	10	1.50		12.00	7.40

Gesamtmasse : 446.86

BAUSTOFFANGABEN (Planspezifisch)						
Bauteile	Expositionsklassen		Beton	Δd	min c	nom c
Fundament (FU04)	XC2		C30/37			4,5cm
Pfeiler (PF02)	XC4		C30/37			3,5cm
Bereiche mit höheren Betonfestigkeiten beachten						
Betonstahl : BSt 500 M(B) BSt 500 S(B)		Standardfase: 1,0/ 1,0 cm				
f						
e						
d						
c						
b						
a	11.07.2023	Graf	Freigabe			
INDEX	DATUM	GEZ.				

Werkplanung		Planung: Hentschke Betonfertigteilterwerk Bautzen Hentschke Bau GmbH Hoyerswerdaer Straße 42 02625 Bautzen Tel.: 03591 6703- Fax: 03591 6703-42	
		Projekt-Nr.: XXXX-XX 50 - 999 - 035	
Bauherr: Intern		gezeichnet: Graf	
Bauvorhaben: IDA-KI Errichtung einer 3-Feld-Brücke		Datum: 06.07.2023	
		Unterschrift:	
Darstellung:		Maßstab:	1 : 50
Bewehrungsplan Unterbauten Achse (40)		Plan-Nr.	Planbezeichnung BP-UB40
		a	