



Spannbeton - Brückenträger FT2.1

Schalung

Draufsicht

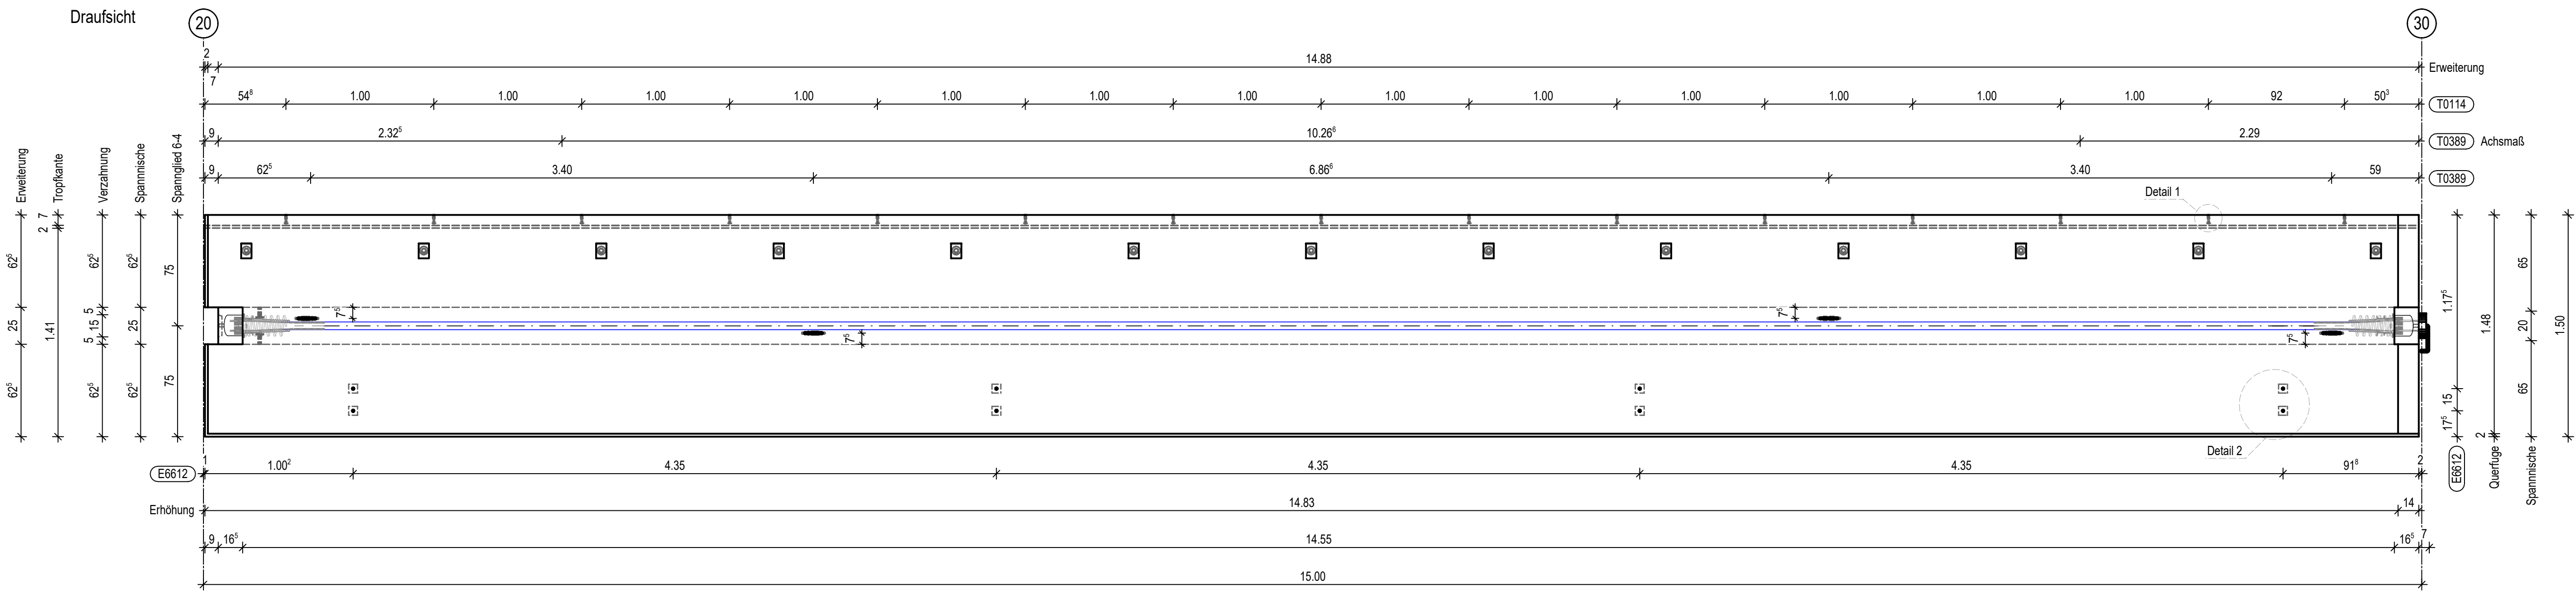


Längsschnitt

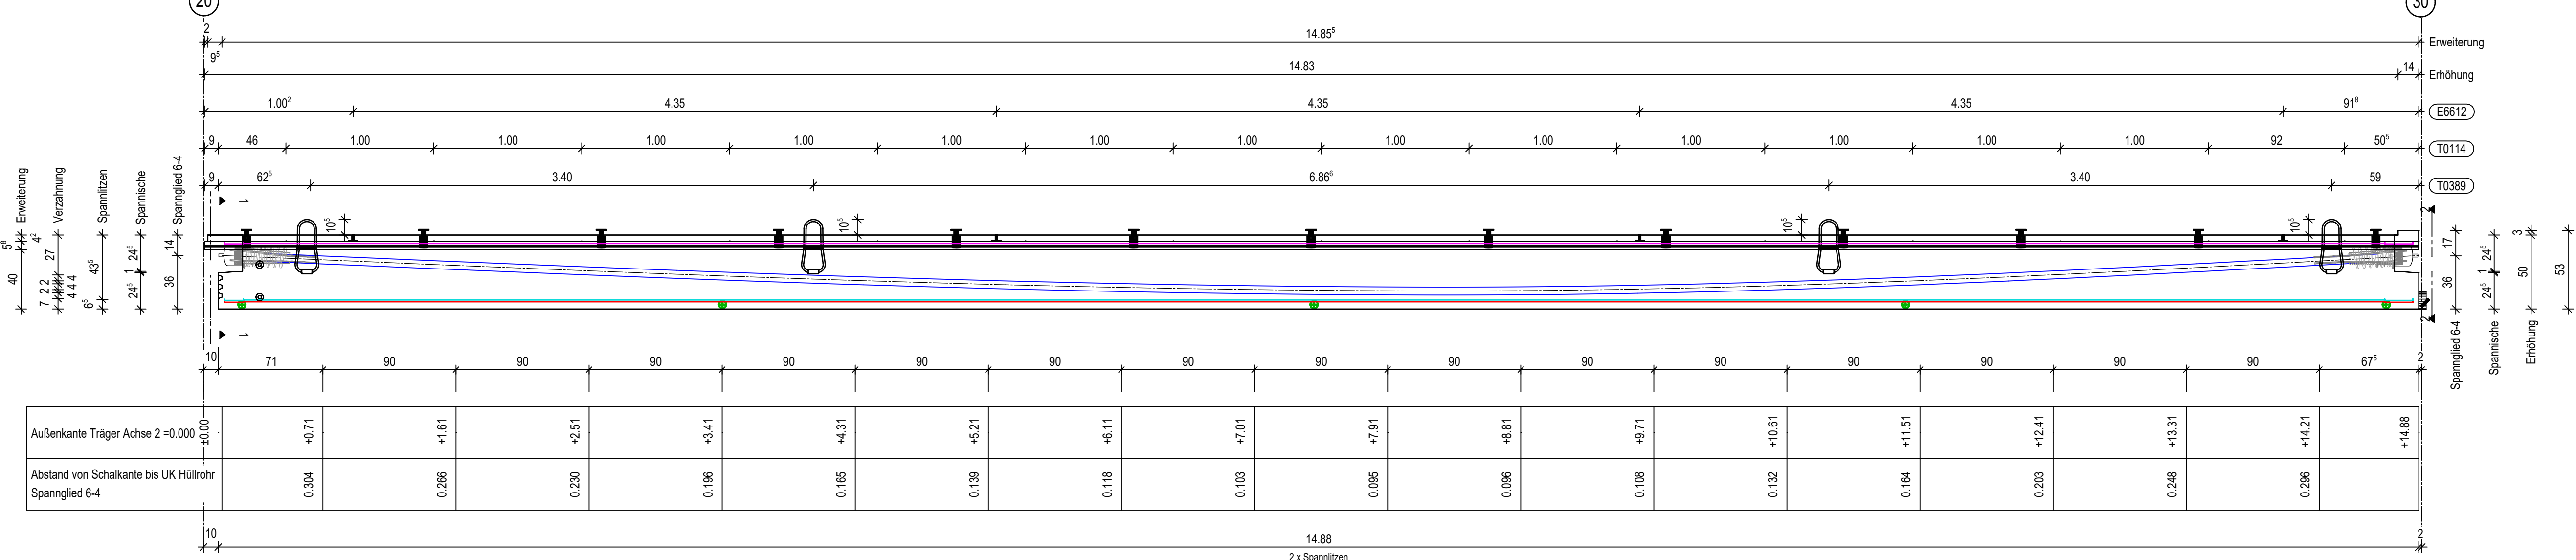


Bewehrung

Draufsicht

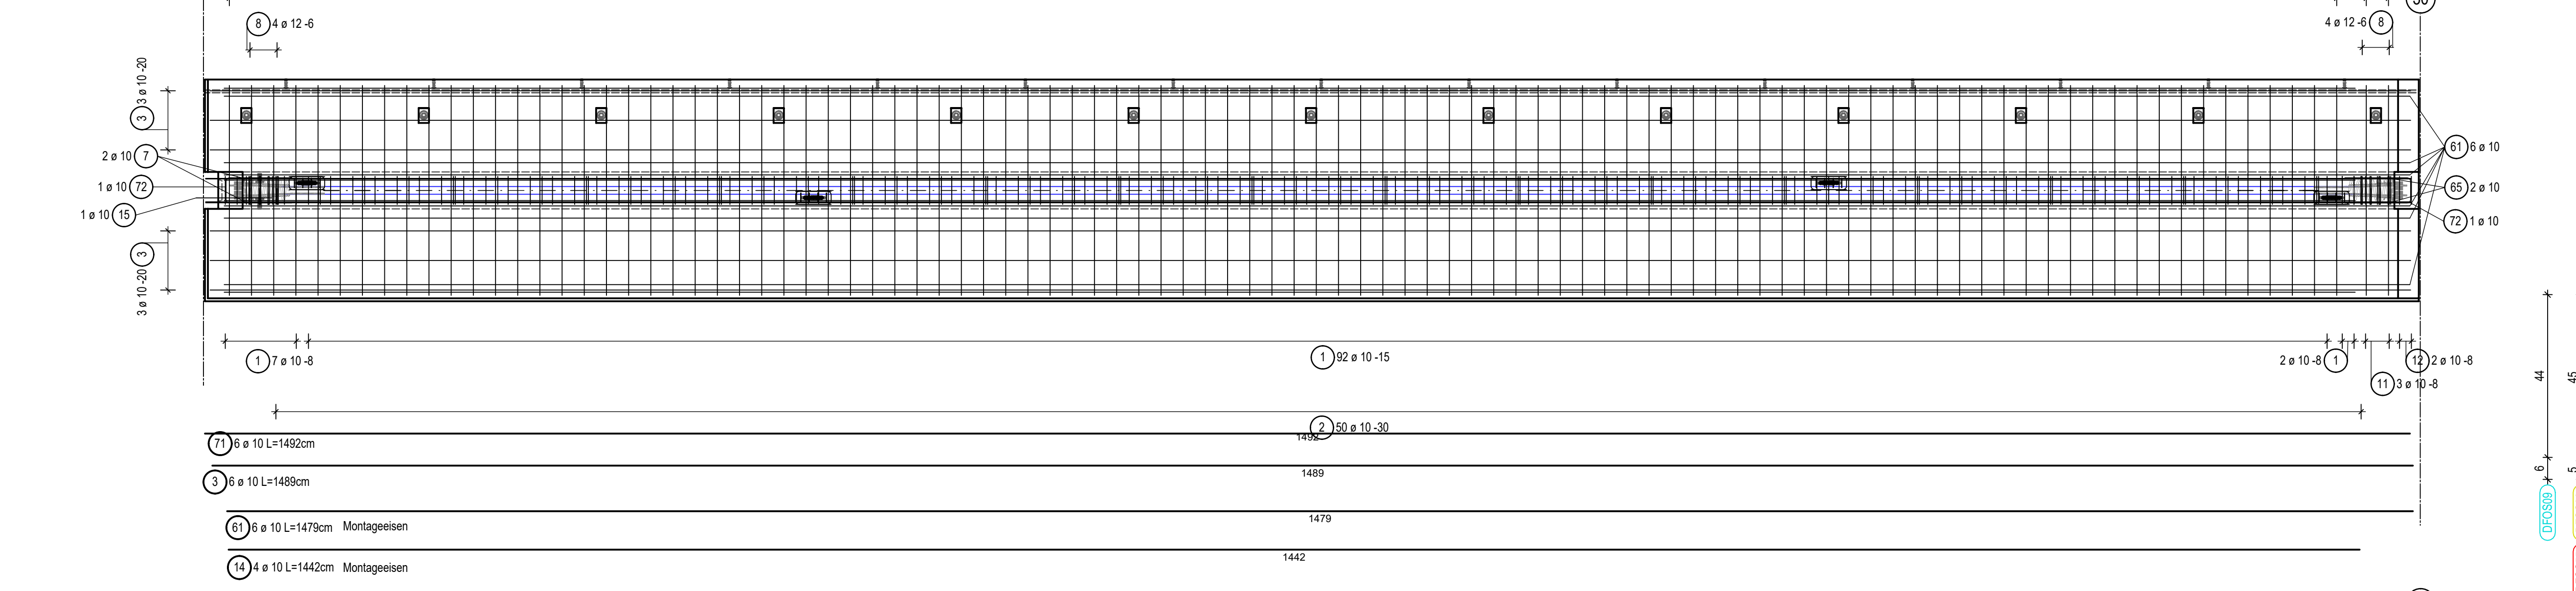


Längsschnitt

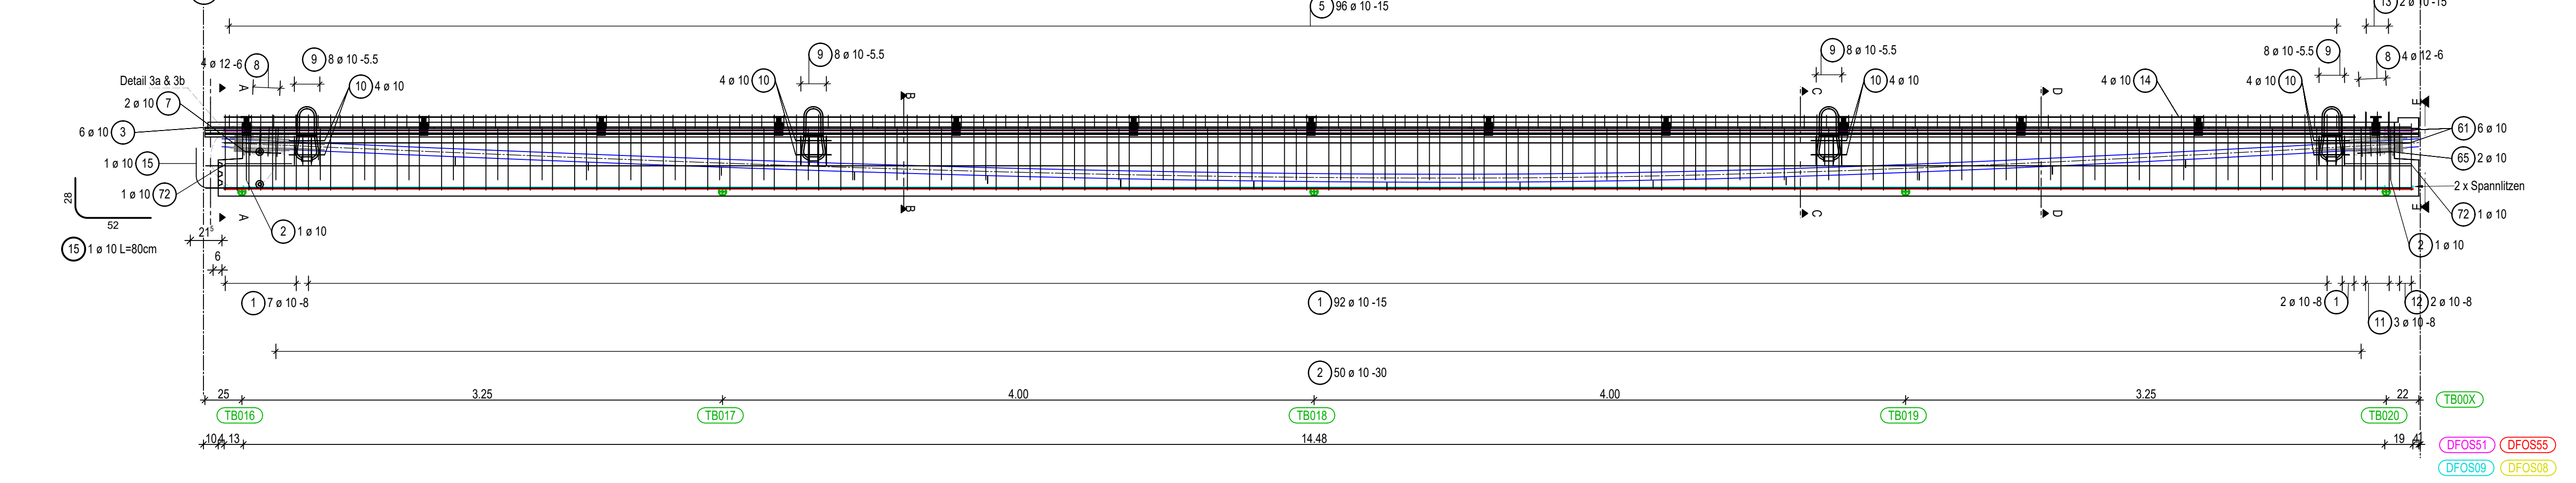


Schnitt A - A

Zulagebewehrung Ankerkörper

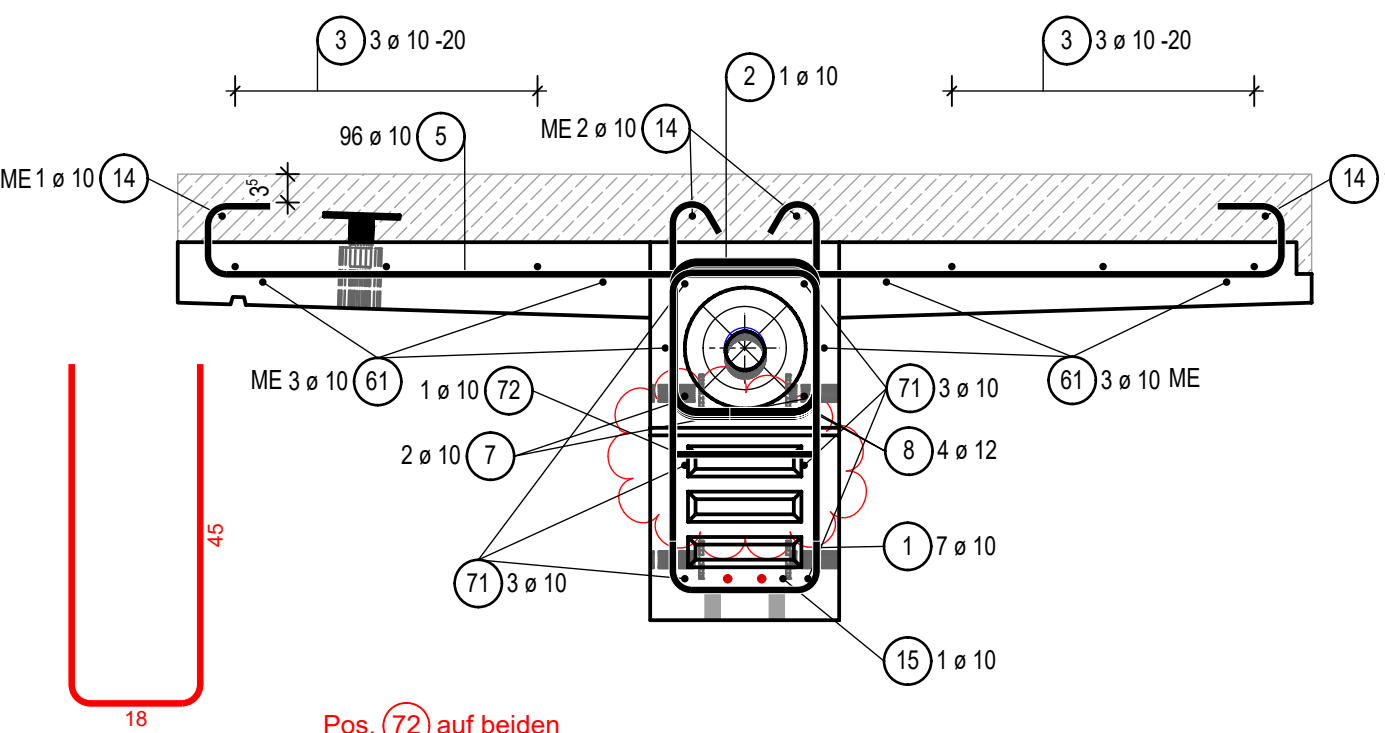


Detail 3a

Zulagebewehrung Wendel

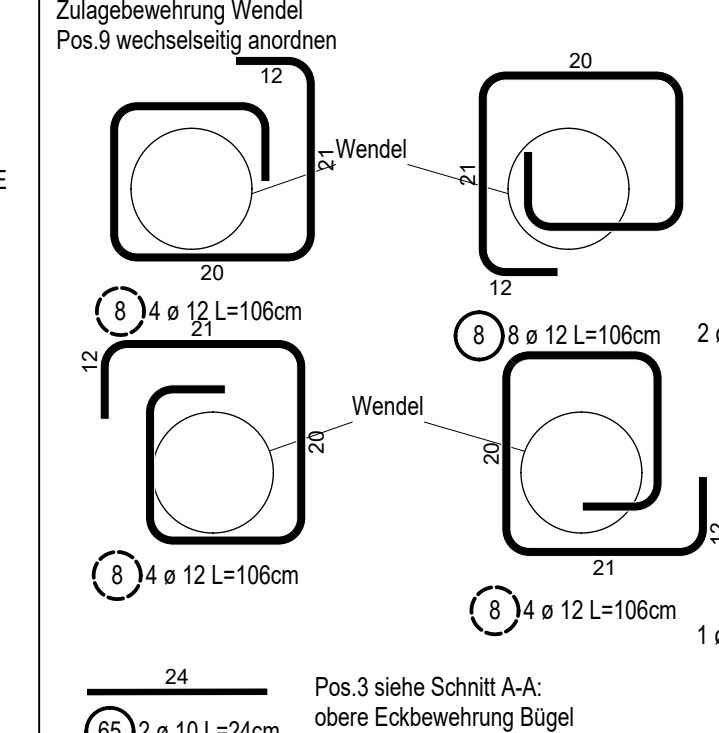



Detail 3b

Bewehrung UHFB-Verbindung

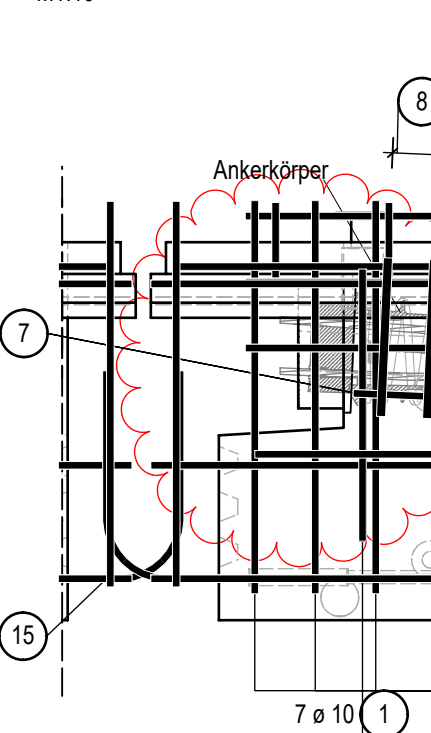


Schnitt B - B

Reinigungschnitt

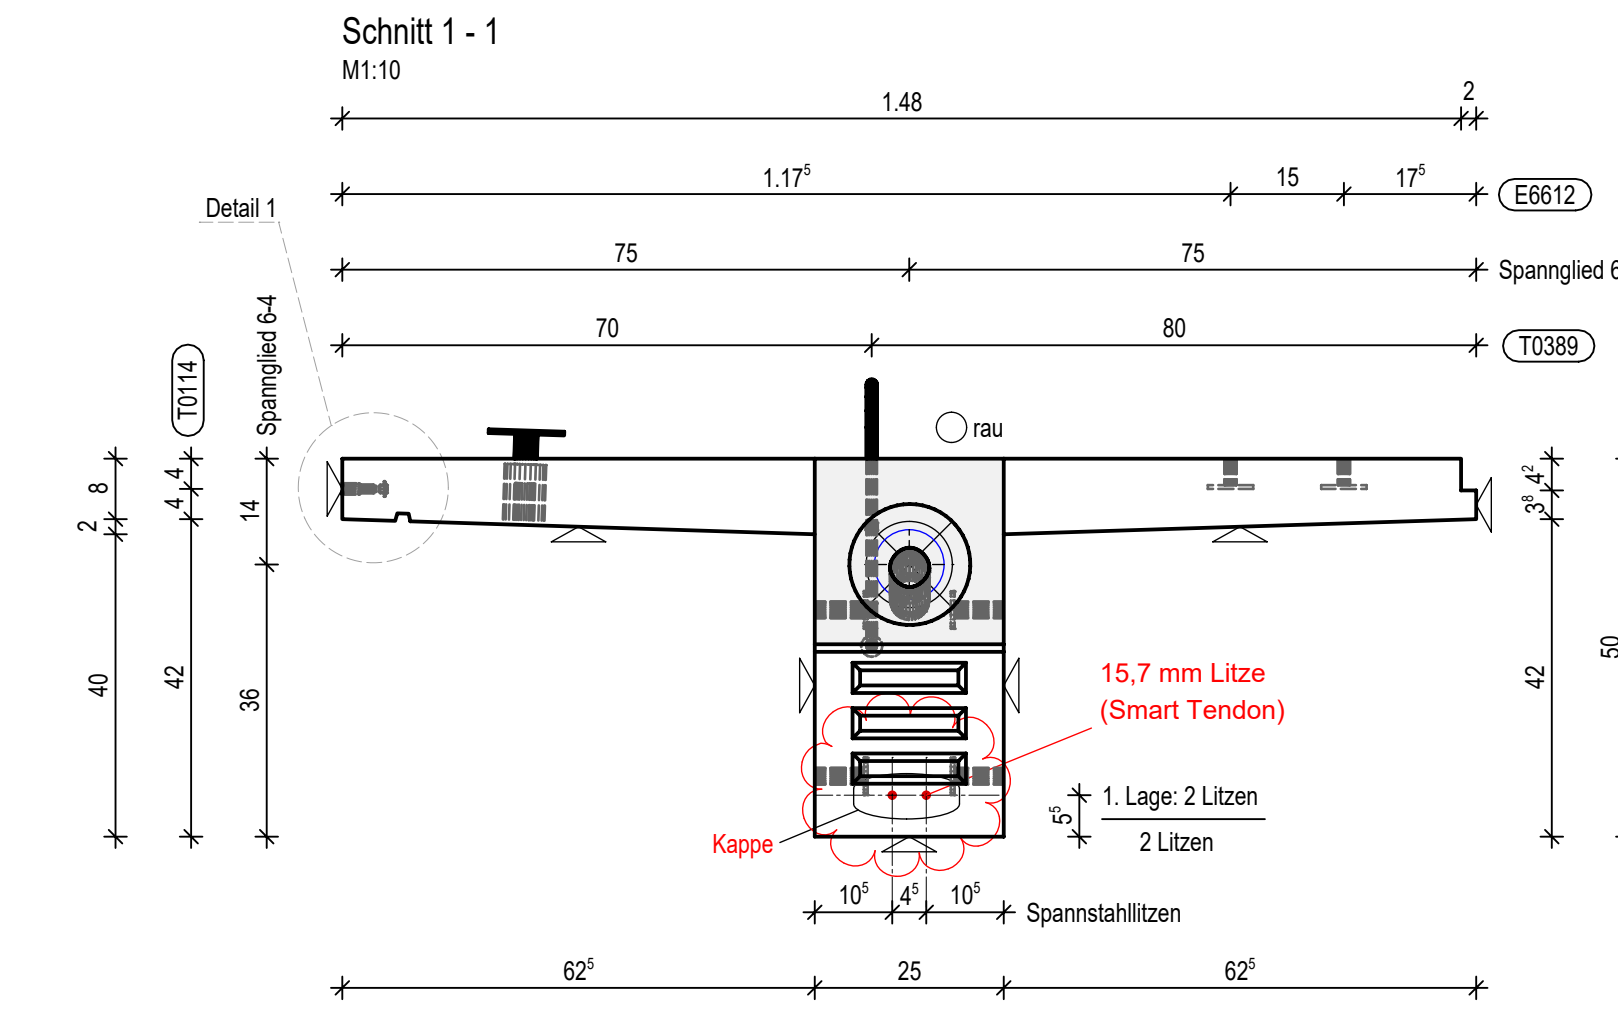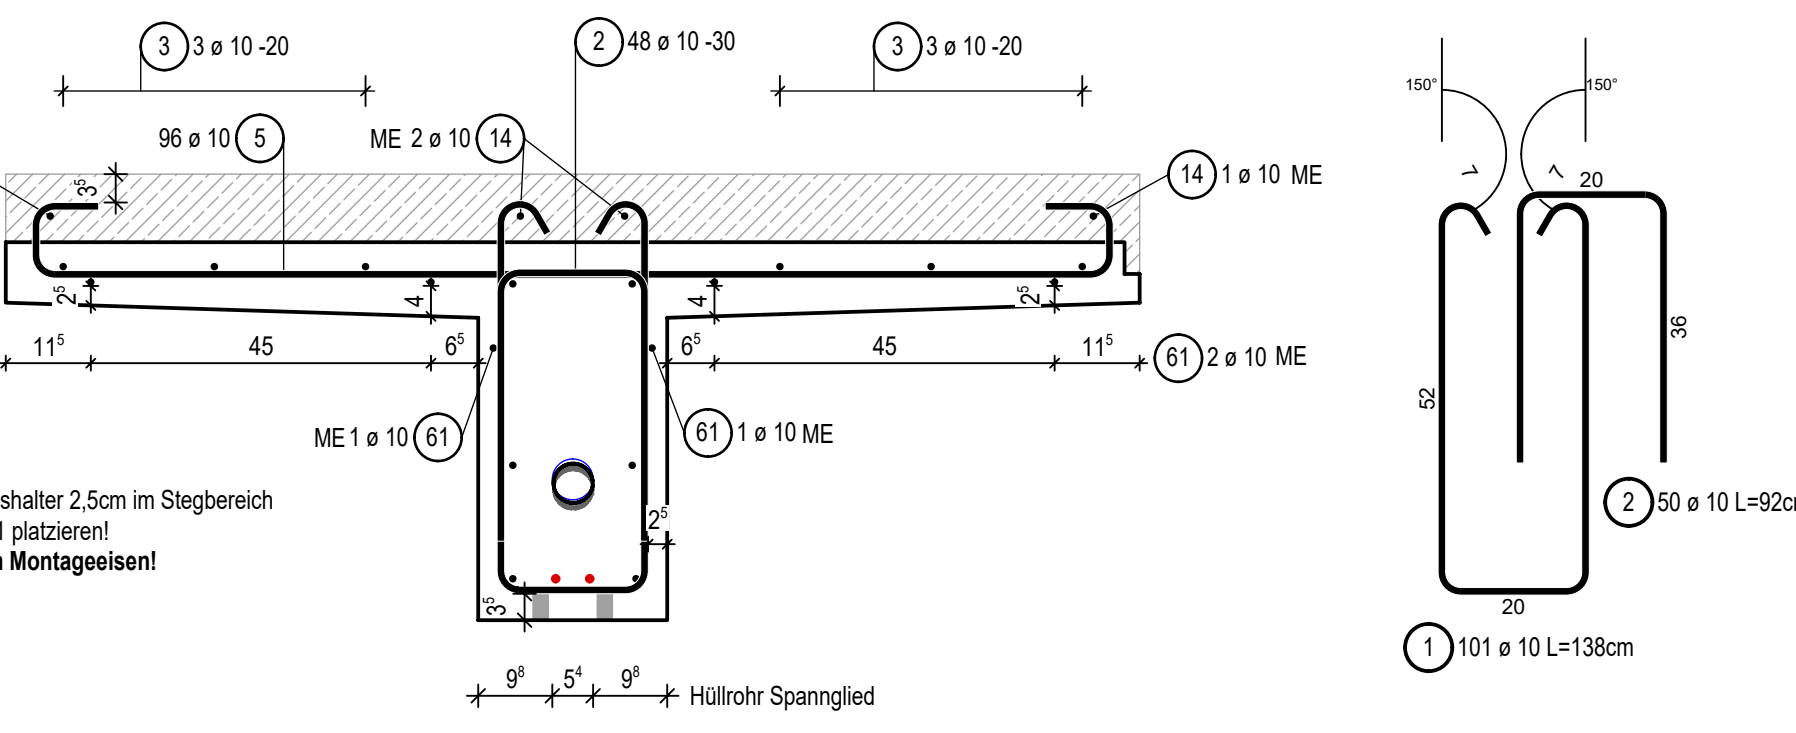


Querschnitt

Verzahnung + Spannische

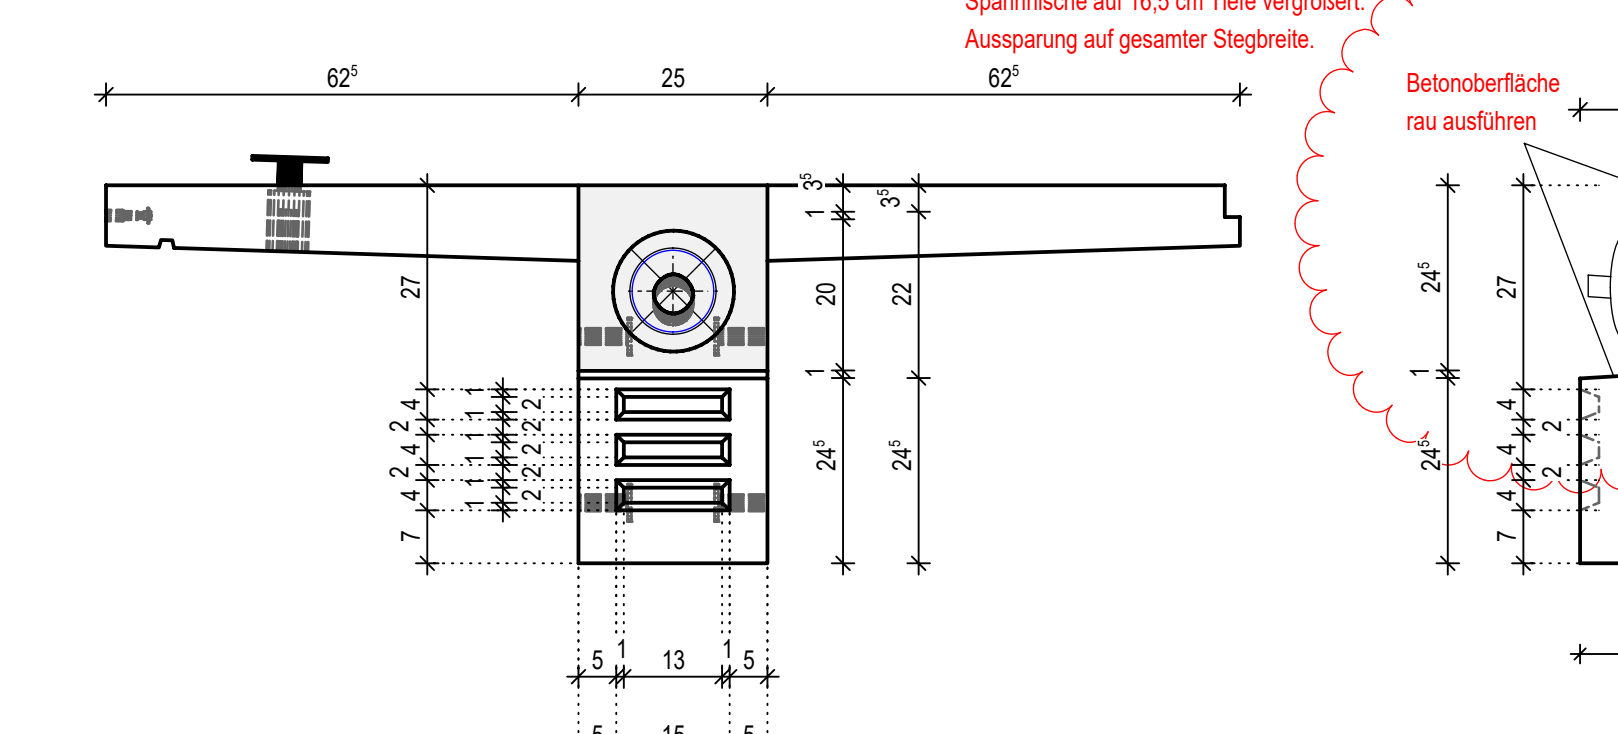


Schnitt 2 - 2

M1:10

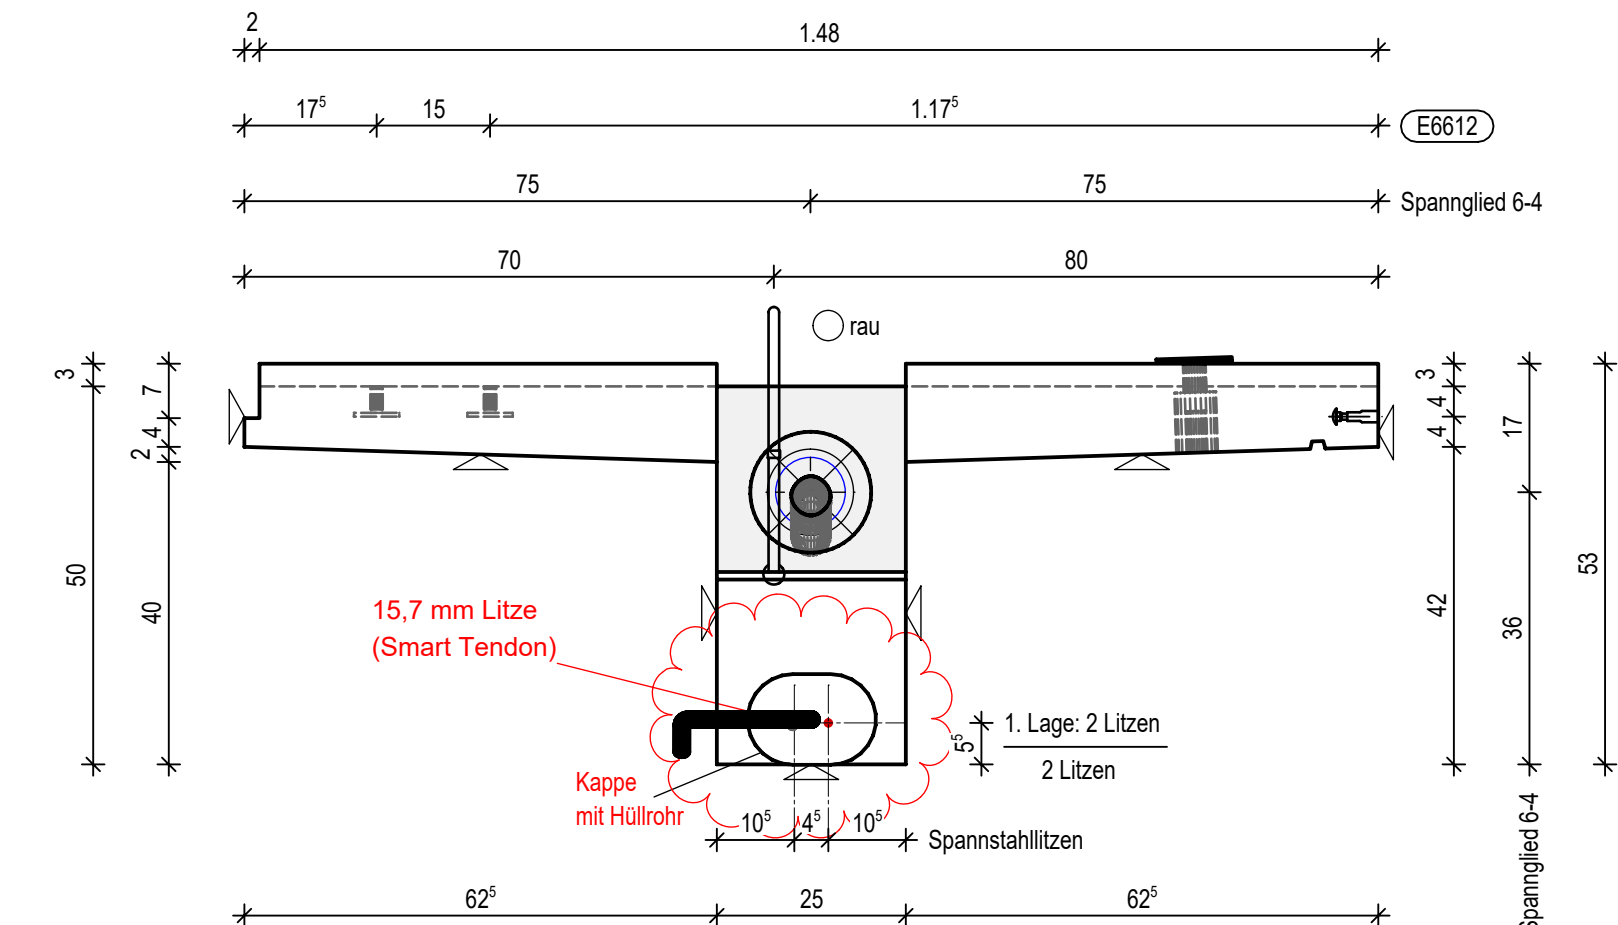


Schnitt E - E

Bewehrung UHFB-Verbindung und Lage Sensoren

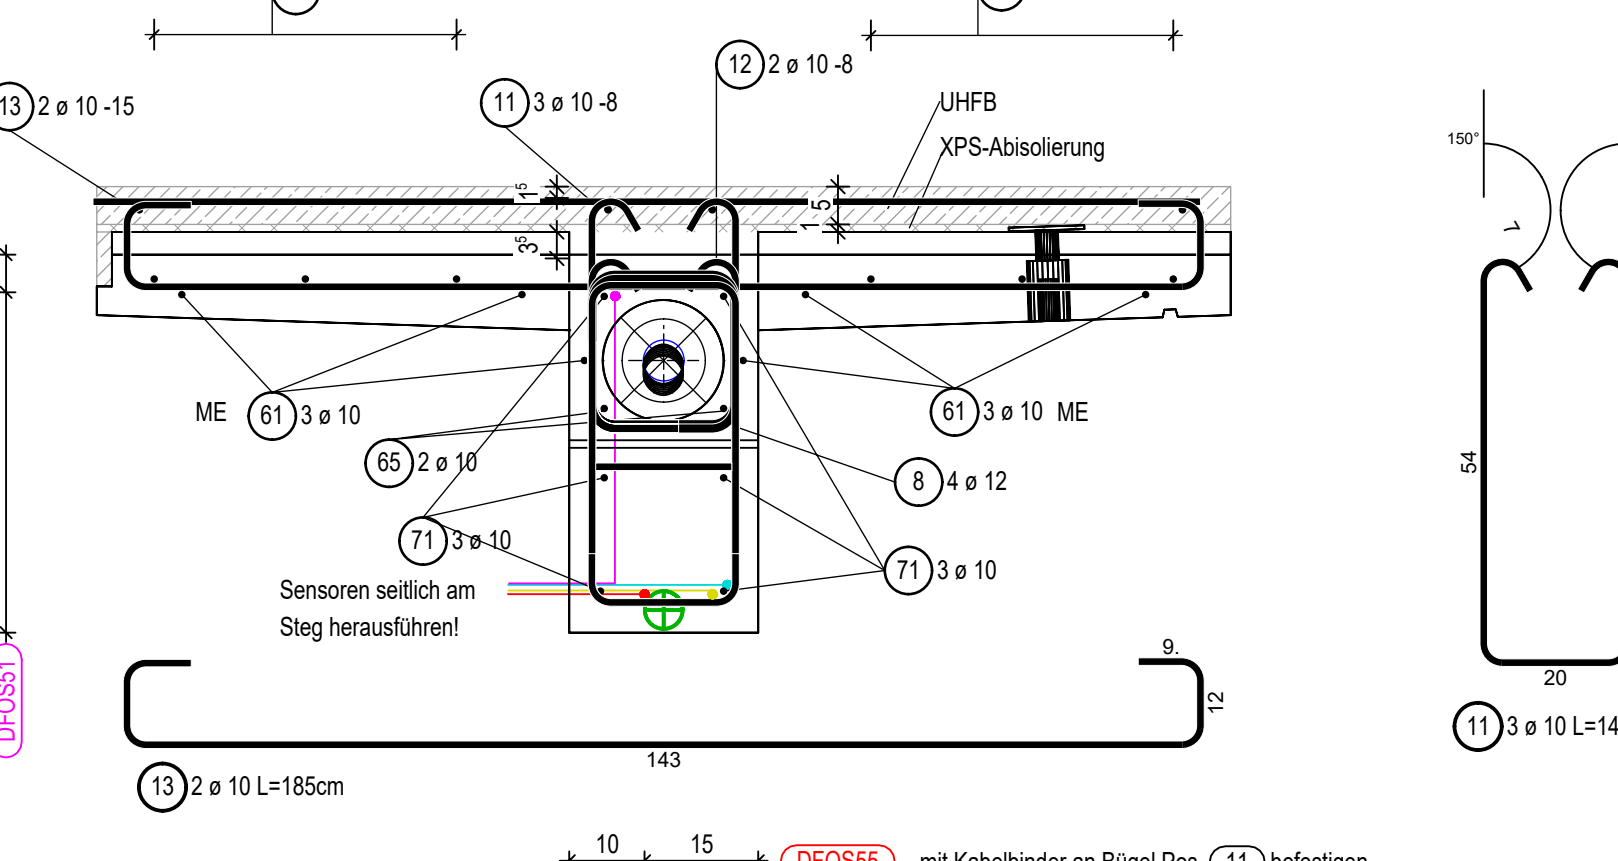


Schnitt C - C

Darstellung Zusatzbewehrung DAHS

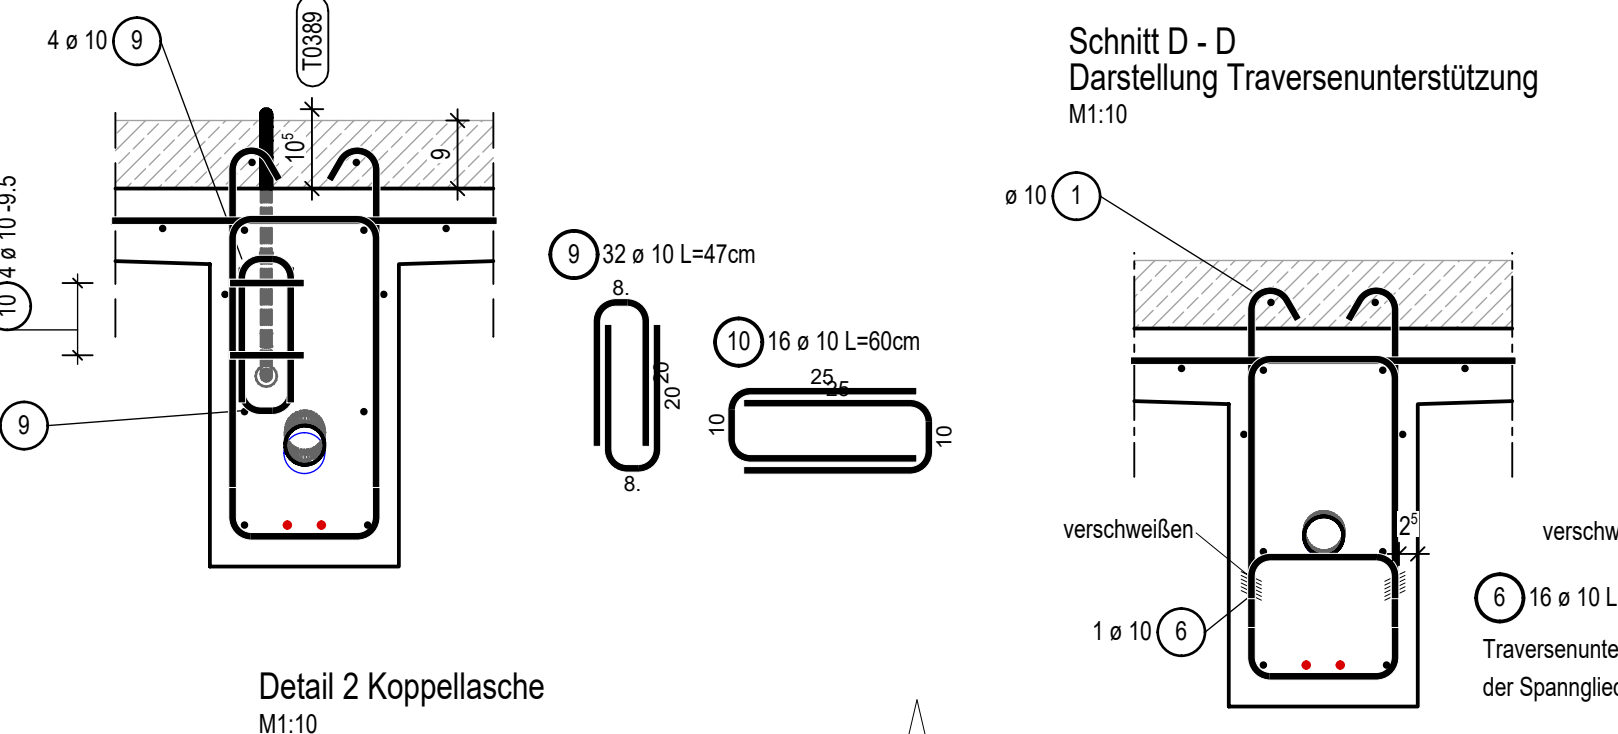




Schnitt D - D

Darstellung Traversenunterstützung

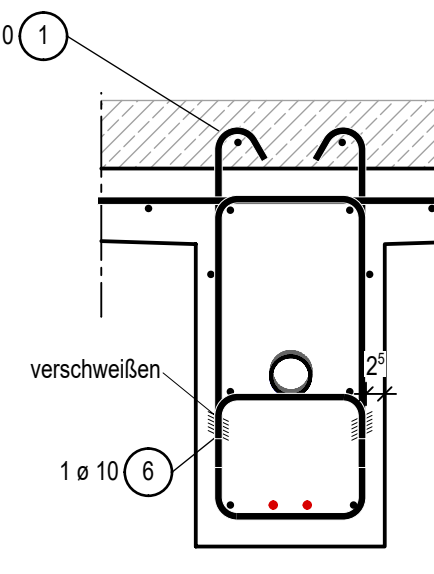

Stabliste

Pos.	Stück	Ø	Einzel	Gesamt	Masse
		[mm]	Länge	Länge	[kg]
1	101	10	1.38	139.38	86.00
2	50	10	0.92	46.00	28.38
3	6	10	14.89	89.34	55.12
4	96	10	1.81	173.76	107.21
5	16	10	0.32	5.12	3.16
6	2	10	0.25	0.50	0.31
7	2	10	1.26	2.52	1.55
8	6	12	1.06	6.48	7.53
9	32	10	0.47	15.04	9.28
10	16	10	0.60	9.60	5.92
11	3	10	1.42	4.26	2.63
12	2	10	1.26	2.52	1.55
13	2	10	1.65	3.30	2.09
14	4	10	14.42	57.68	35.59
15	1	10	0.80	0.80	0.49
16	6	10	14.79	88.74	54.75
65	2	10	0.24	0.48	0.30
71	6	10	14.92	89.52	55.23
72	2	10	1.09	2.18	1.35

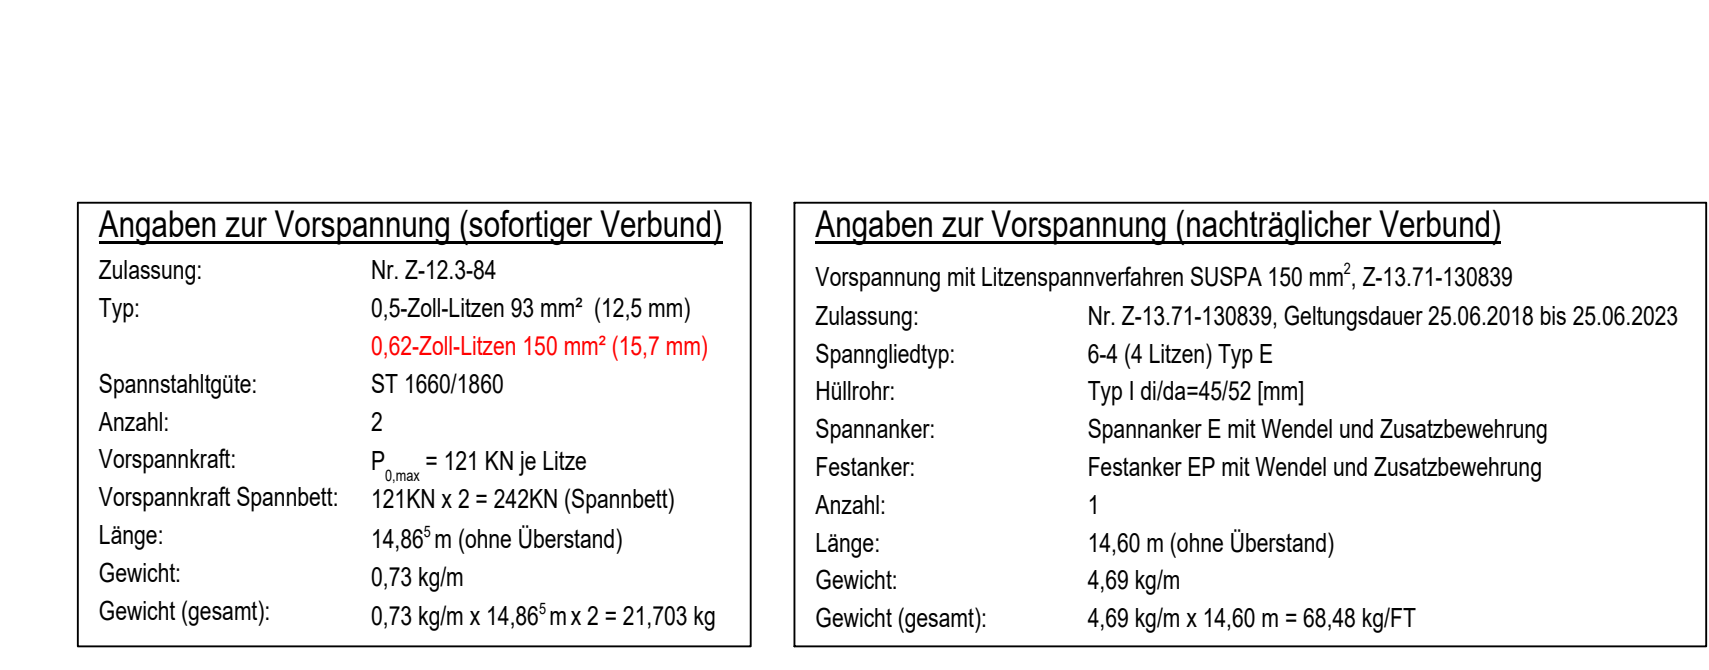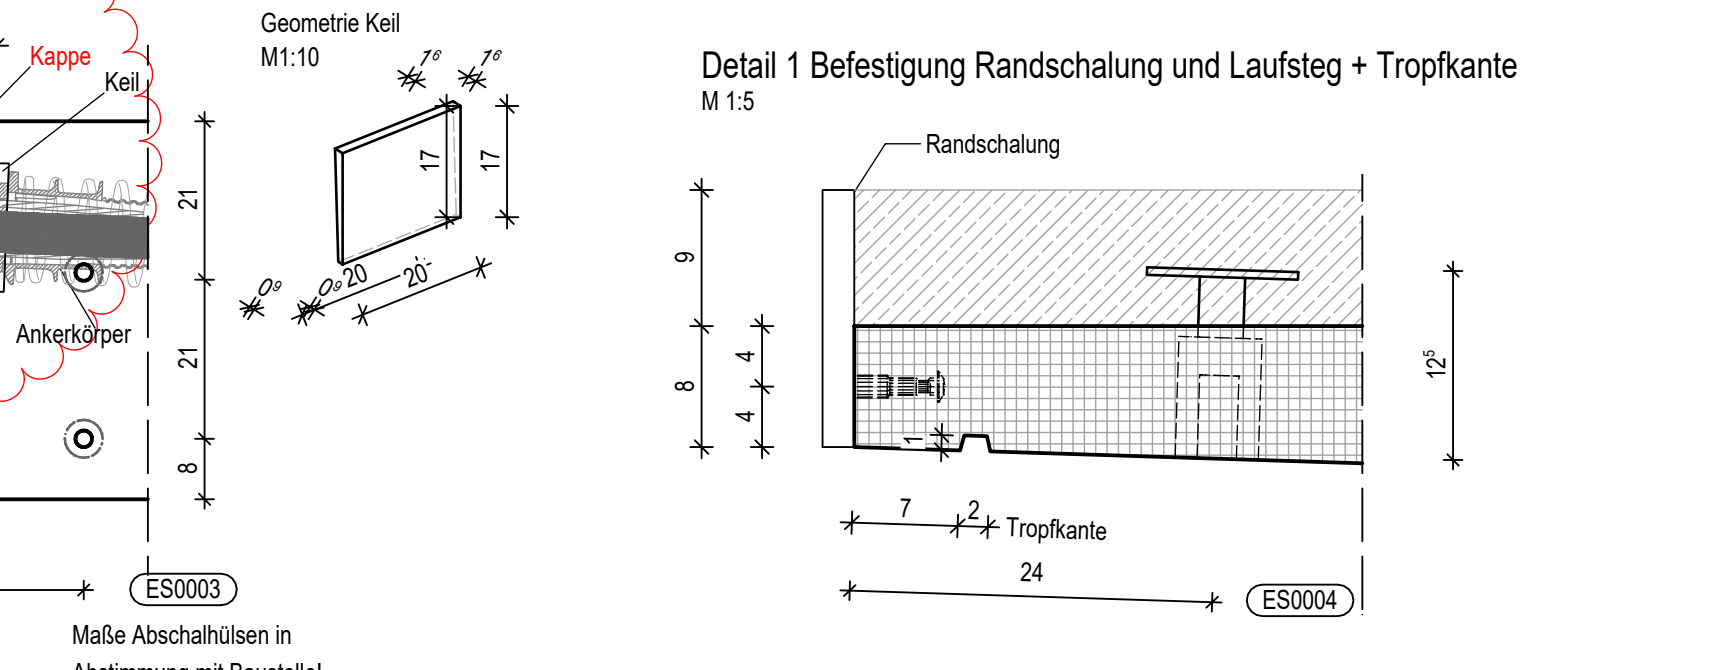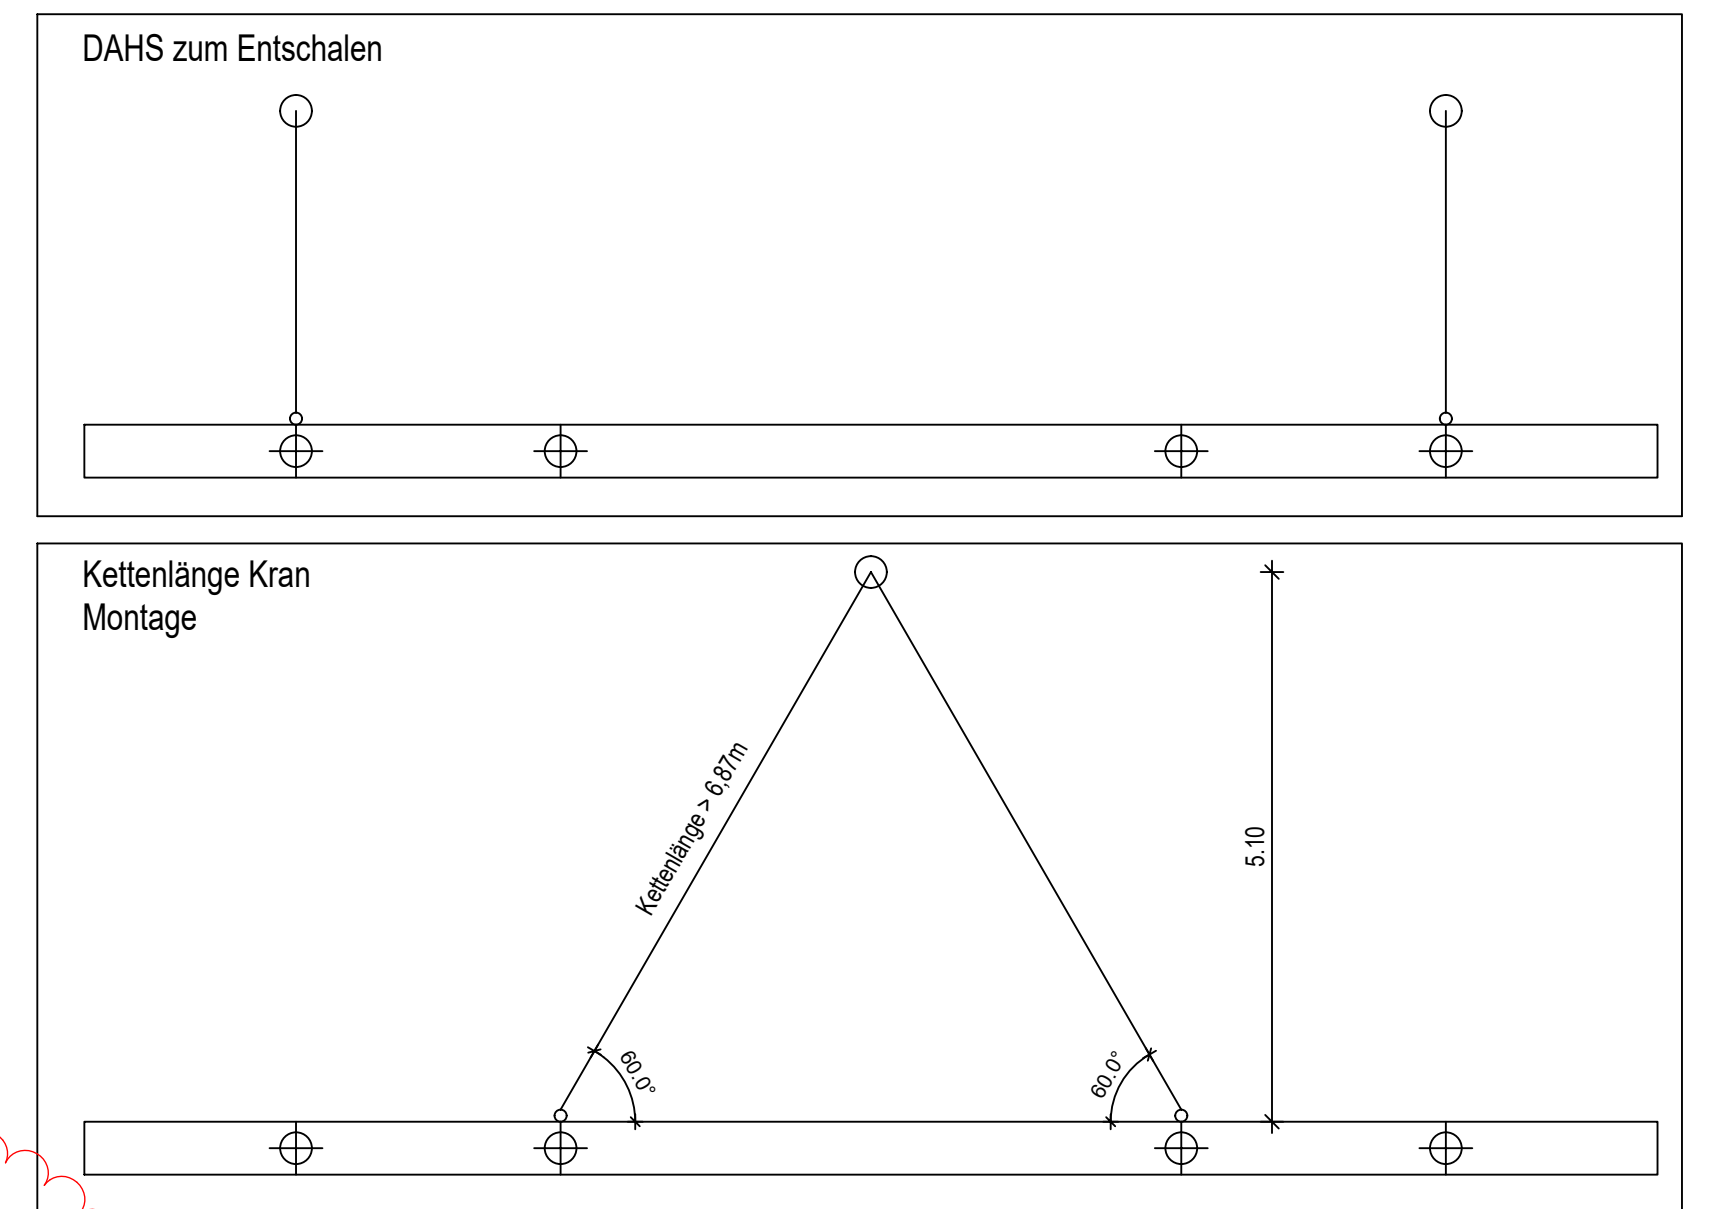

Pos.	Anzahl	Bezeichnung
1	1	Epoxi-Sensoren 3.0 m R. BDO C2=0.19m; A=14.48m; C1=0.13m; P1=3.68m
2	1	Epoxi-Sensoren 1.0 m R. BDO C2=0.19m; A=14.48m; C1=0.13m; P1=3.68m
3	1	3D Sensor A=15.30m; P1=3.68m
4	1	Soltes Temperatur BRÜSENS; A=14.70m; P1=2.80m
5	1	Kobold M16 - Gewindestange mit M16 Schrauben
6	8	Kobold M16 - Gewindestange mit M16 Schrauben
7	4	ES0003 Abschaltheile DW15, Profillänge 75 mm, Spezialkunststoff, inkl. Nagelstopfen
8	13	ES0004 Betonmax Kobold B 15-FB
9	15	Schraubenanker RD12 60mm
10	4	Drahtseilbeschläufe 5.2 verz.
11	5	Thermosensor Typ K, TB016 - TB020

