


Spannbeton - Brückenträger FT2.3


Schalung

Draufsicht

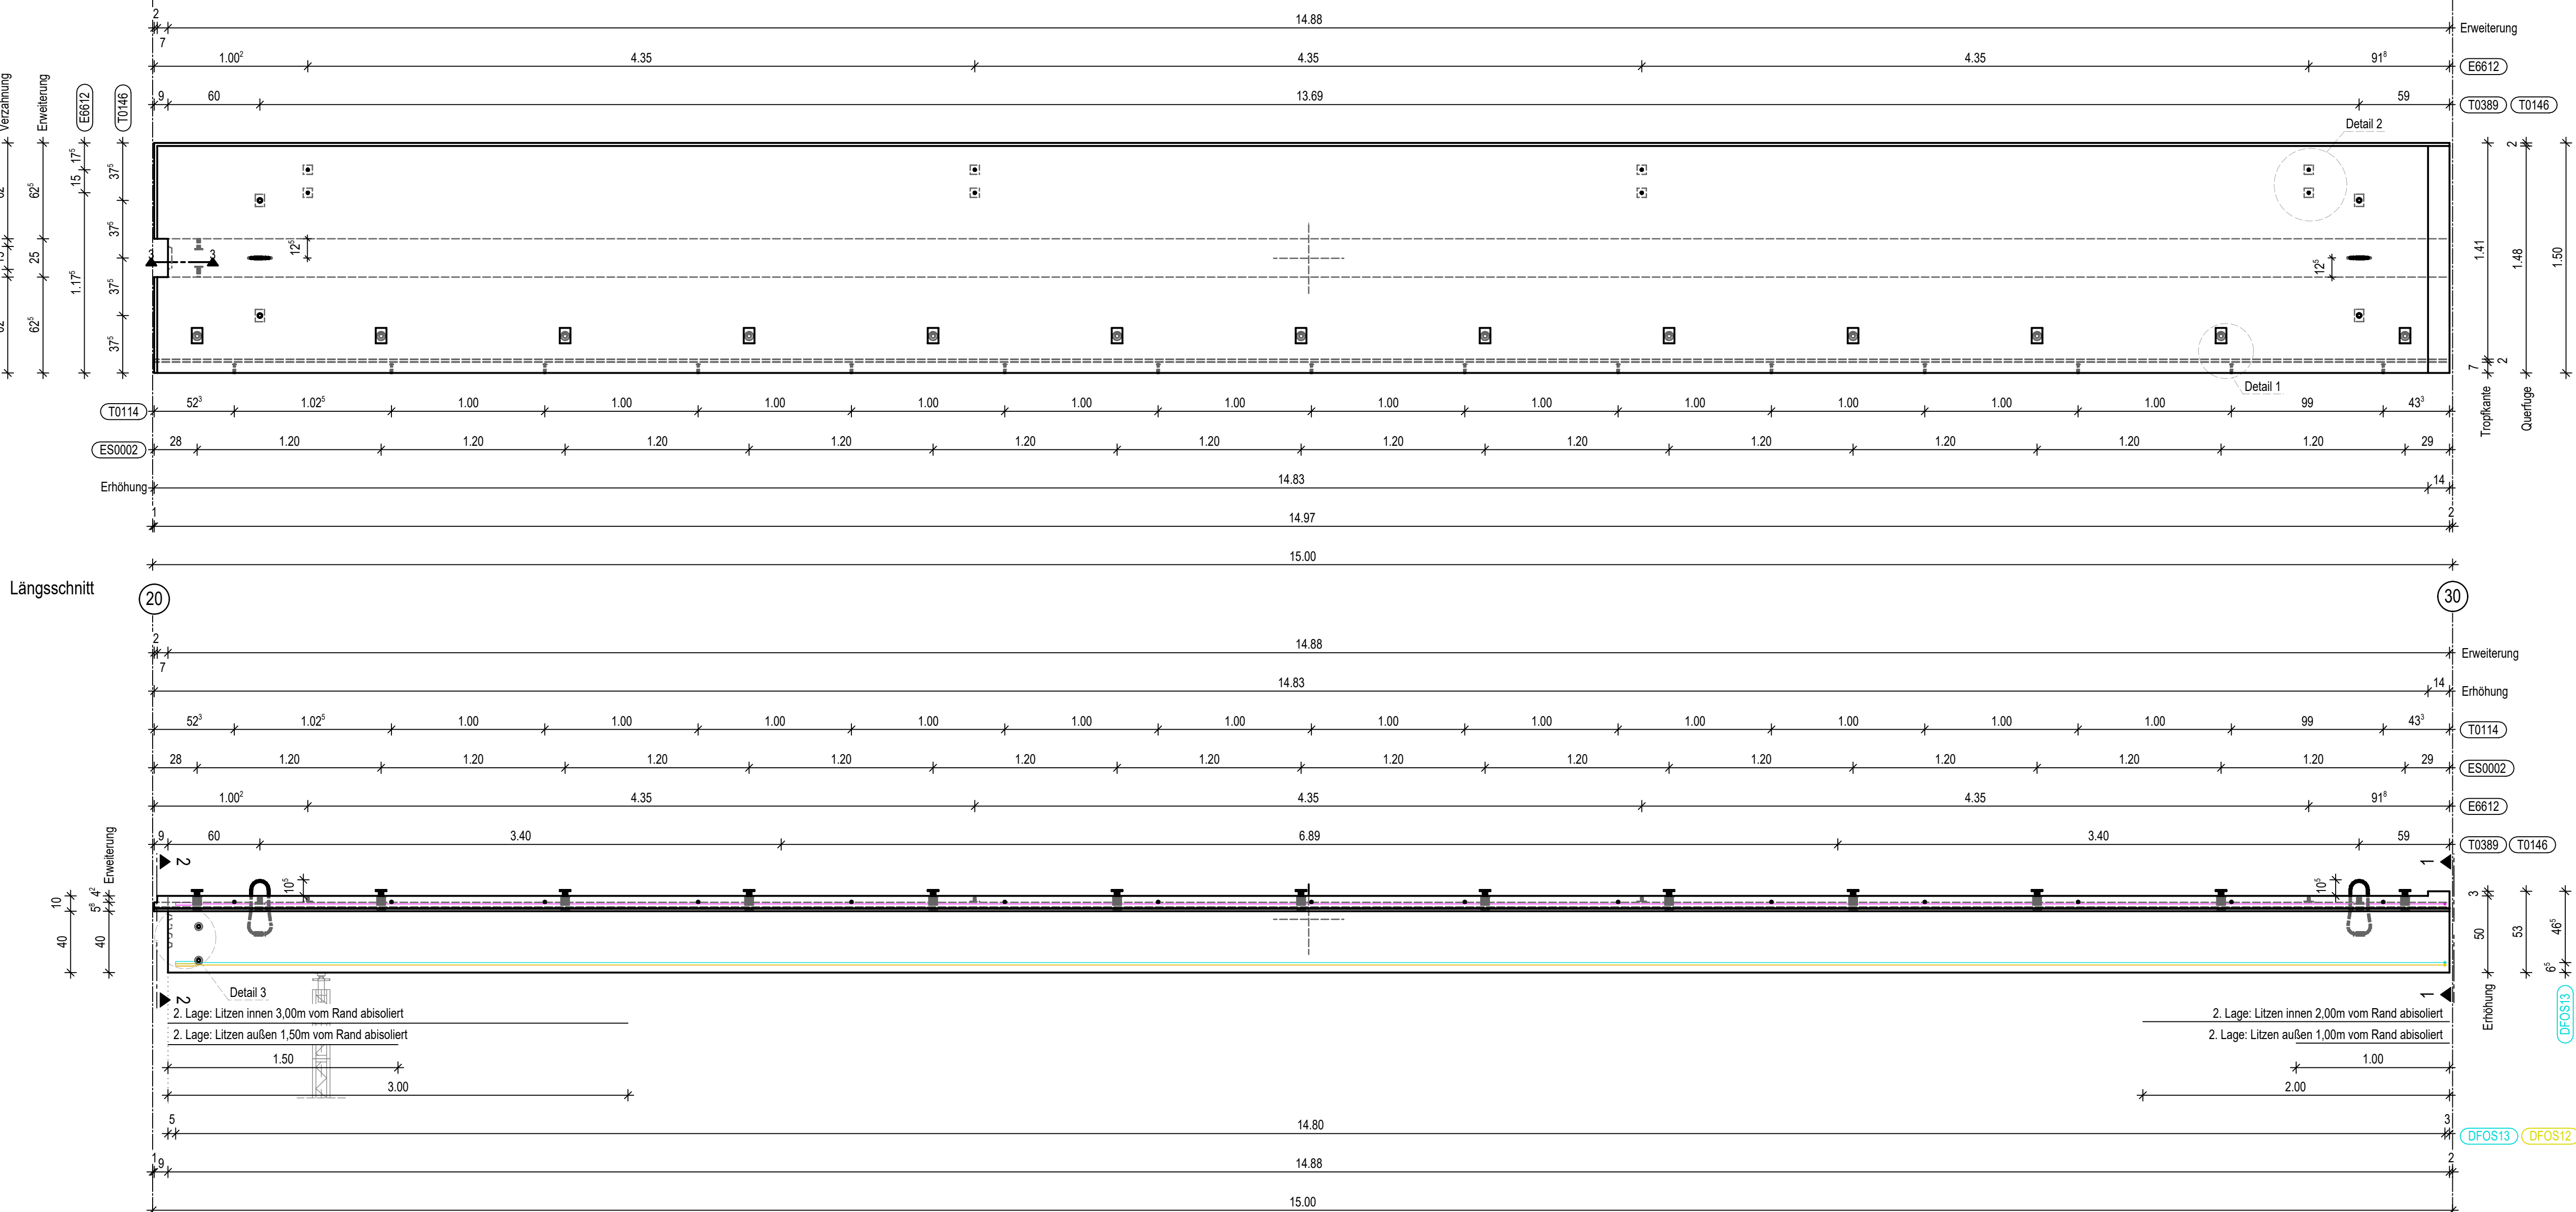


Bewehrung

Draufsicht

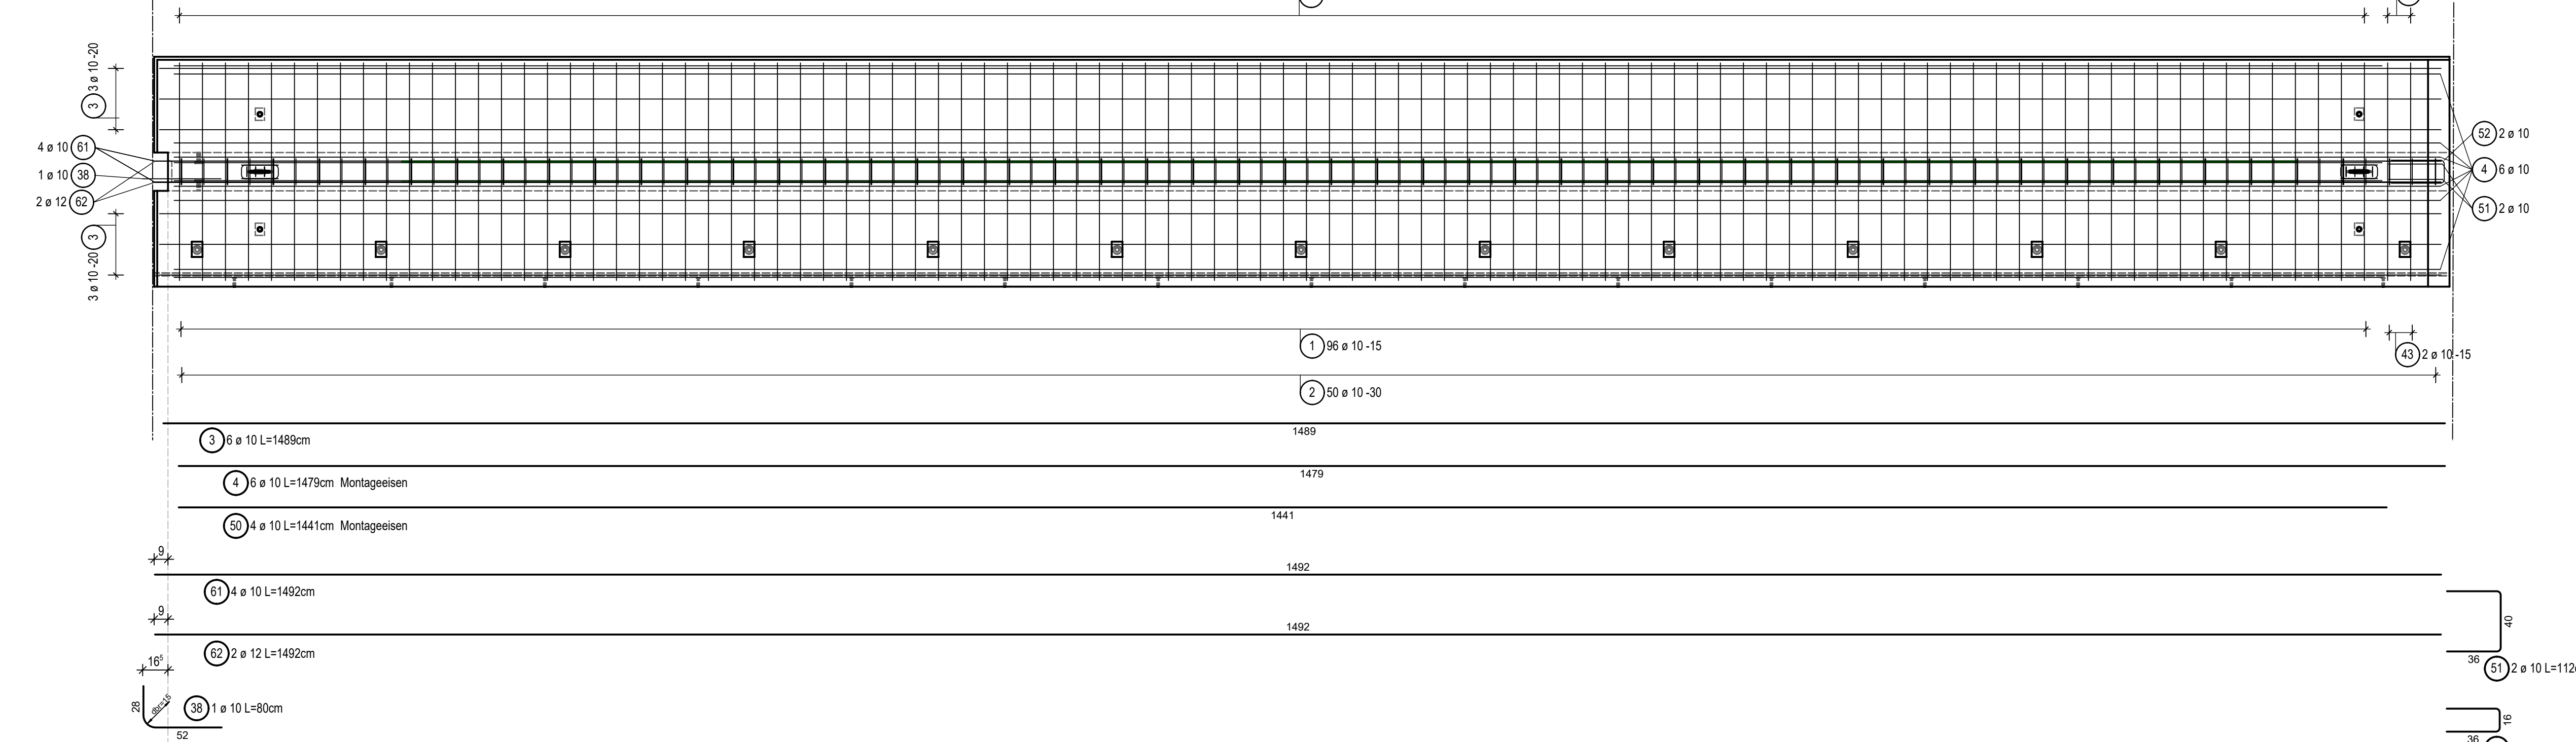

Längsschnitt

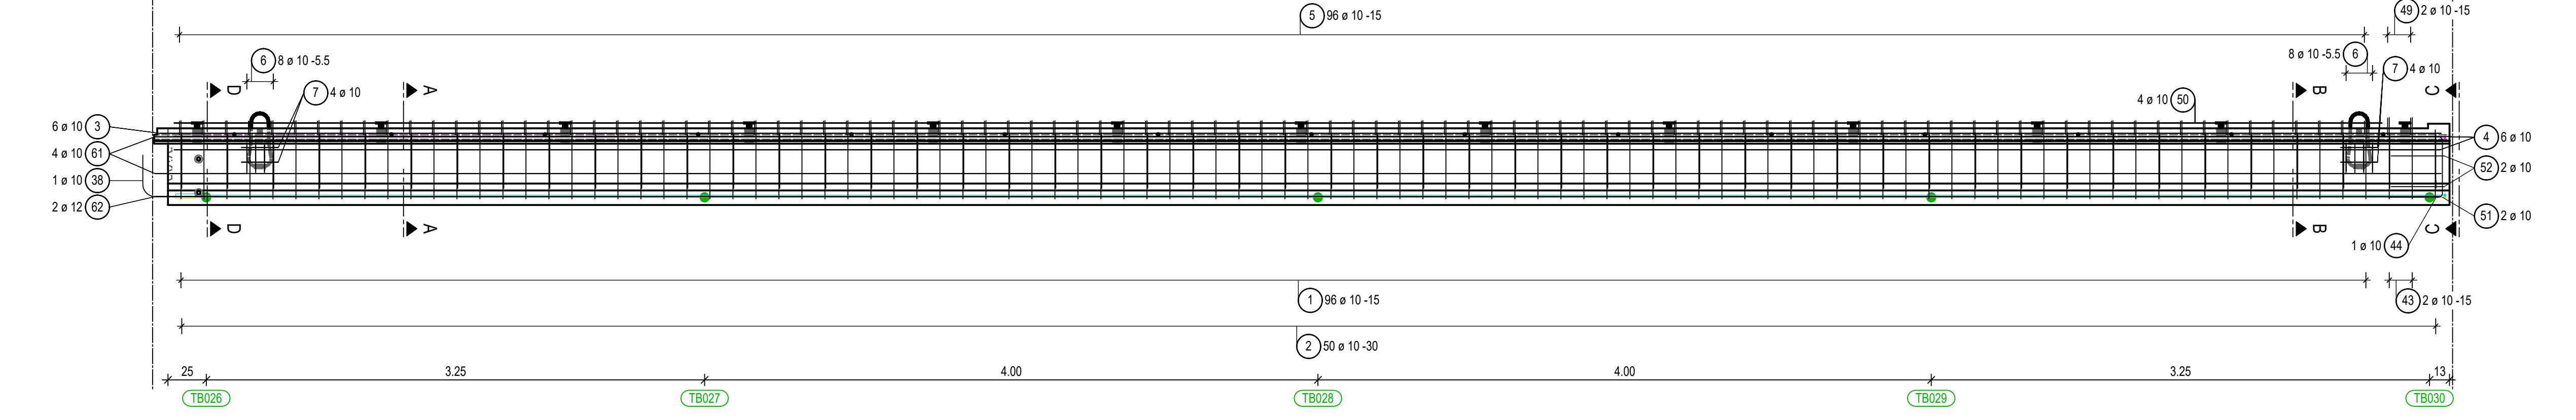

Schnitt B - B

Lage Sensoren

M1:10

Sensoren seitlich am

Steg herausführen!

mit Kabelbinder an Bügel Pos.5 befestigen

an Pos.62 anheben

mit Kabelbinder an Bügel Pos.1 befestigen

an Pos.62 anheben

mit Kabelbinder an Bügel Pos.1 befestigen

an Pos.62 anheben

mit Kabelbinder an Bügel Pos.1 befestigen

an Pos.62 anheben

mit Kabelbinder an Bügel Pos.1 befestigen

an Pos.62 anheben

mit Kabelbinder an Bügel Pos.1 befestigen

an Pos.62 anheben

Schnitt C - C

Bewehrung UHFB-Verbindung

M1:10

Sensoren seitlich am

Steg herausführen!

mit Kabelbinder an Bügel Pos.5 befestigen

an Pos.62 anheben

mit Kabelbinder an Bügel Pos.1 befestigen

an Pos.62 anheben

mit Kabelbinder an Bügel Pos.1 befestigen

an Pos.62 anheben

mit Kabelbinder an Bügel Pos.1 befestigen

an Pos.62 anheben

mit Kabelbinder an Bügel Pos.1 befestigen

an Pos.62 anheben

mit Kabelbinder an Bügel Pos.1 befestigen

an Pos.62 anheben

Schnitt D - D

Darstellung Zusatzbewehrung DAHS + Lage Pos.38

M1:10

Sensoren seitlich am

Steg herausführen!

mit Kabelbinder an Bügel Pos.5 befestigen

an Pos.62 anheben

mit Kabelbinder an Bügel Pos.1 befestigen

an Pos.62 anheben

mit Kabelbinder an Bügel Pos.1 befestigen

an Pos.62 anheben

mit Kabelbinder an Bügel Pos.1 befestigen

an Pos.62 anheben

mit Kabelbinder an Bügel Pos.1 befestigen


an Pos.62 anheben

mit Kabelbinder an Bügel Pos.1 befestigen

an Pos.62 anheben


Detail 1 Befestigung Randschalung und Laufsteg + Tropfkante

M 1:5

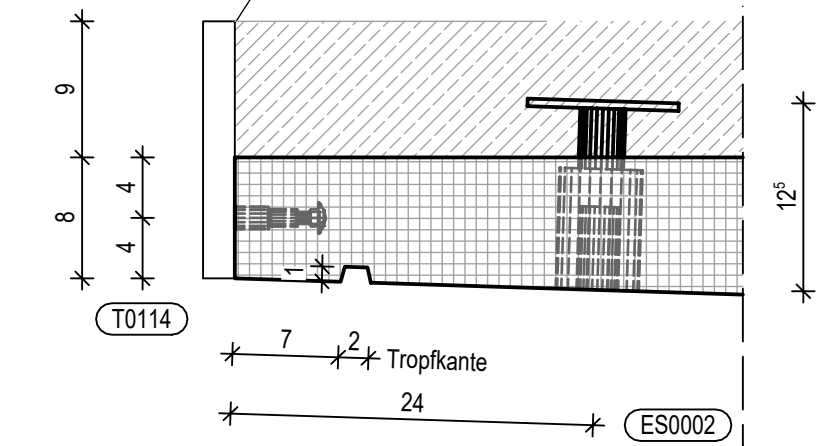


Detail 2 Koppellasche

M1:10

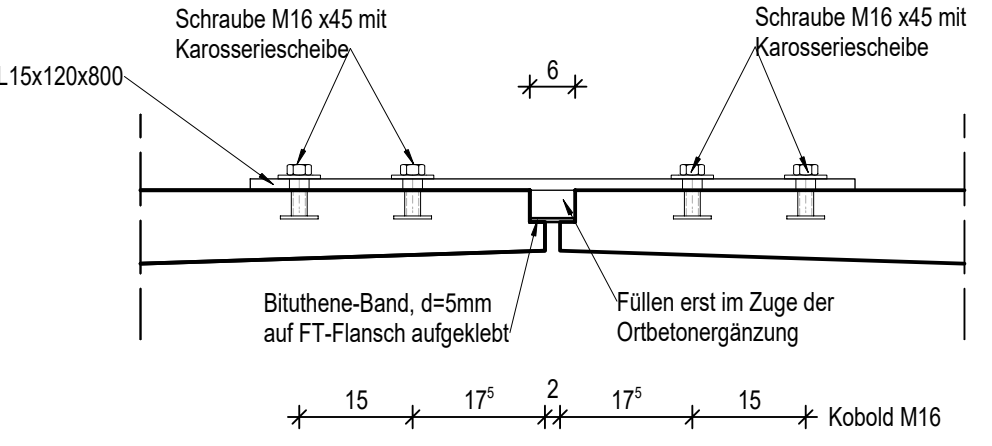


Draufsicht

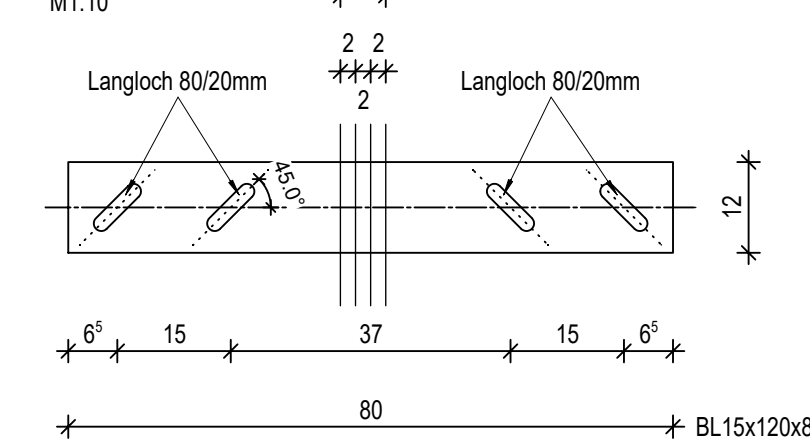


Ansicht 1 - 1

M1:10

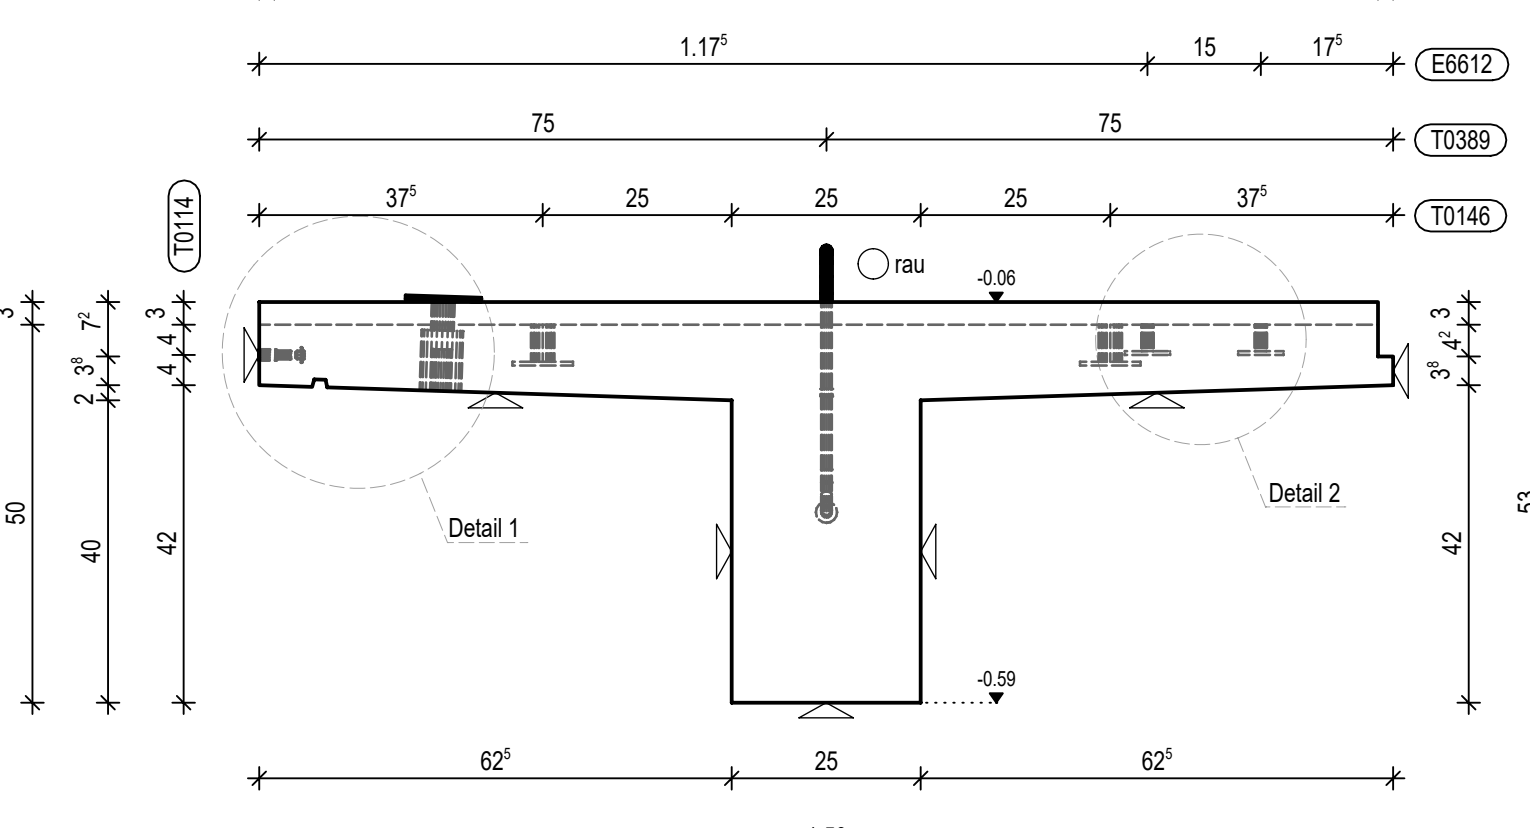


Ansicht 2 - 2

M1:10

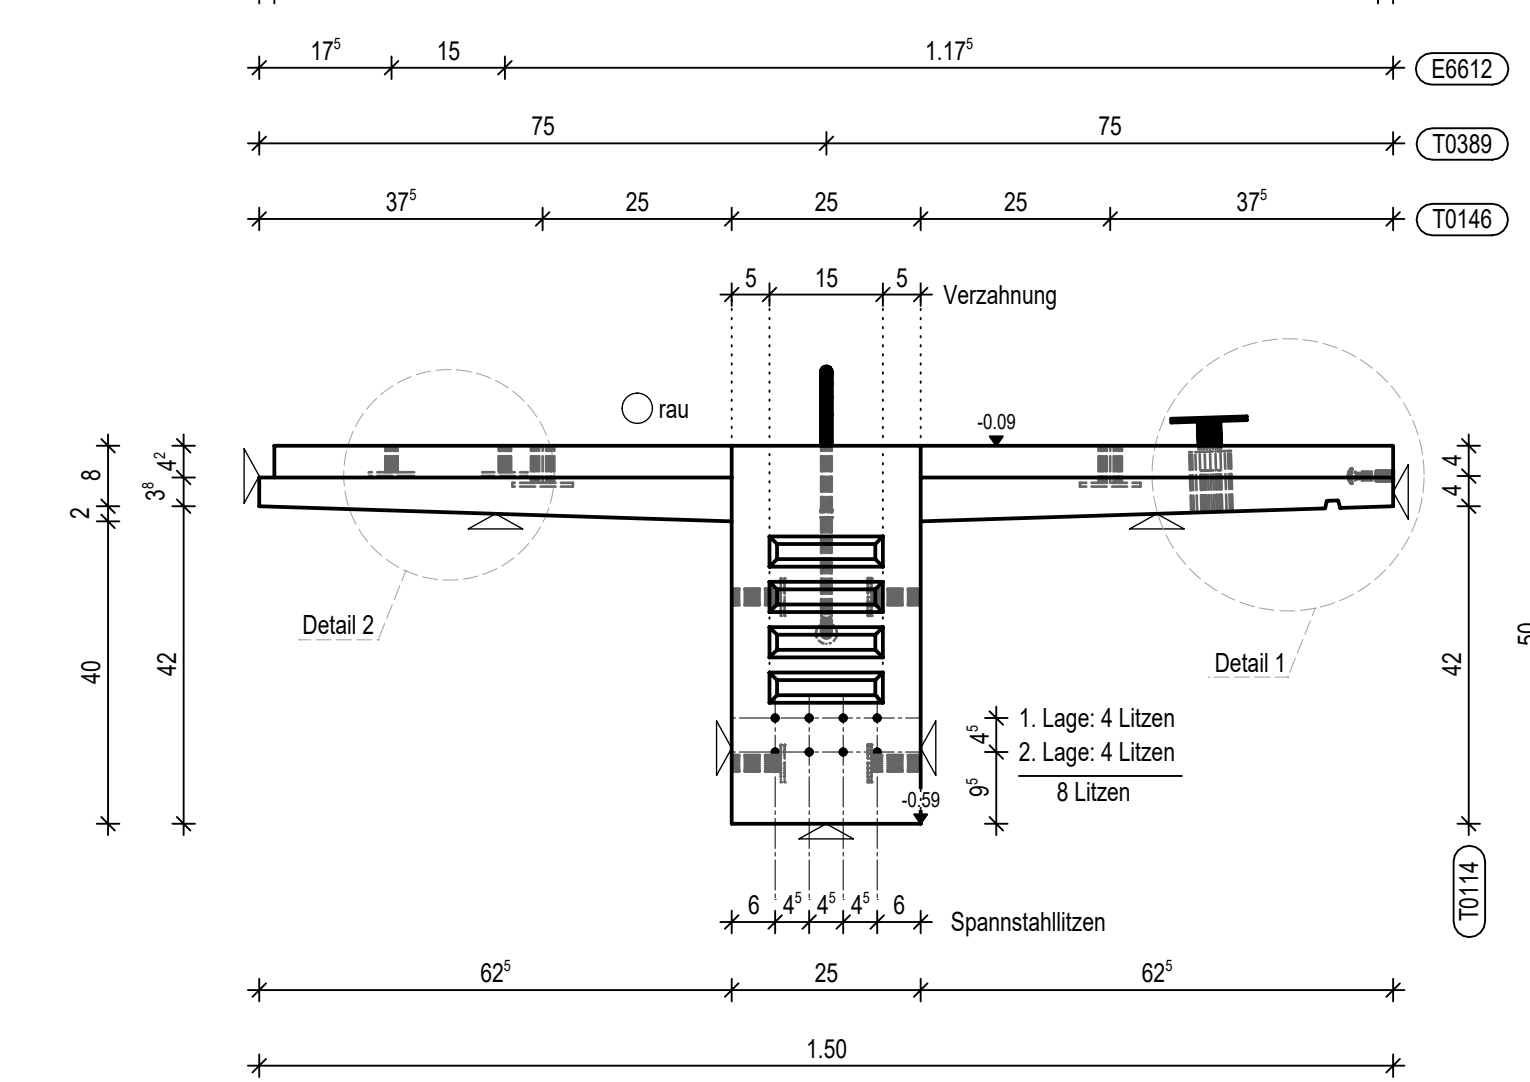

Schnitt A - A


M1:10

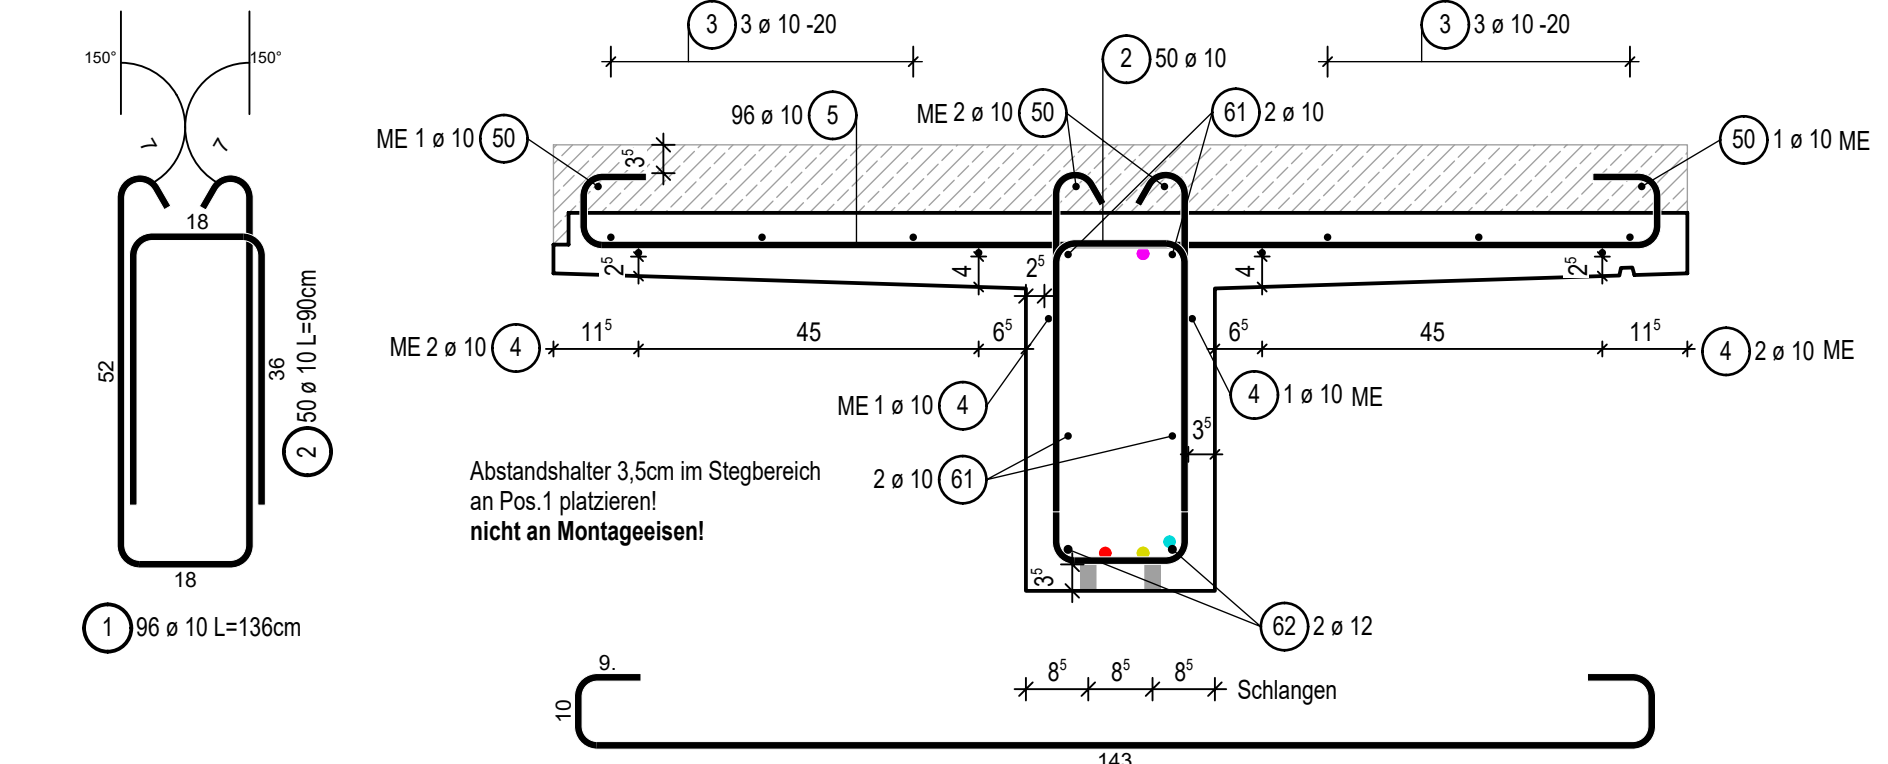


Stabliste

Pos.	Stück	Ø	Einzel Länge	Gesamt Länge	Masse
1	96	10	1.36	130.56	80.56
2	50	10	0.90	45.00	27.77
3	6	10	14.89	89.34	55.12
4	6	10	14.79	88.74	54.75
5	96	10	1.81	173.76	107.21
6	16	10	0.47	7.52	4.64
7	8	10	0.60	4.80	2.96
8	1	10	0.80	0.80	0.49
9	43	2	1.40	2.80	1.73
44	1	10	1.24	1.24	0.77
45	2	10	1.85	3.70	2.28
46	4	10	14.41	57.64	35.56
51	2	10	1.12	2.24	1.36
52	2	10	0.87	1.74	1.07
61	4	10	14.92	59.68	36.82
62	2	12	14.92	29.84	26.50

DAHS zum Entschalen

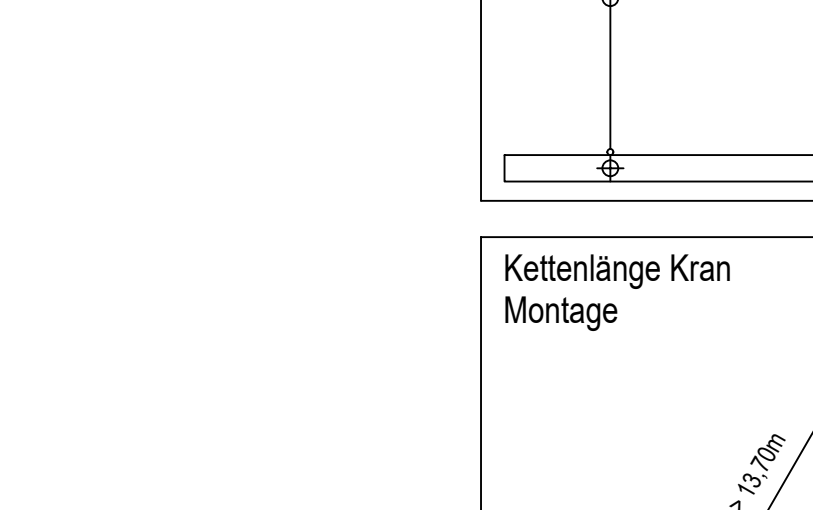


Kettenlänge Kran

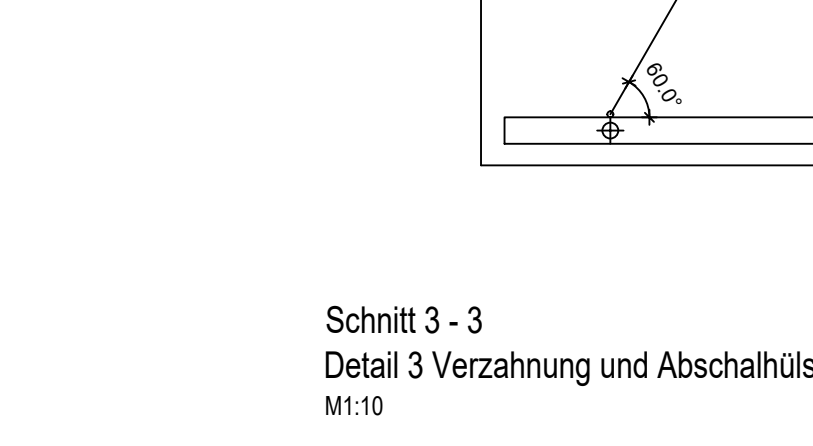

Schnitt 3 - 3


Detail 3 Verzahnung und Abschalhülsen

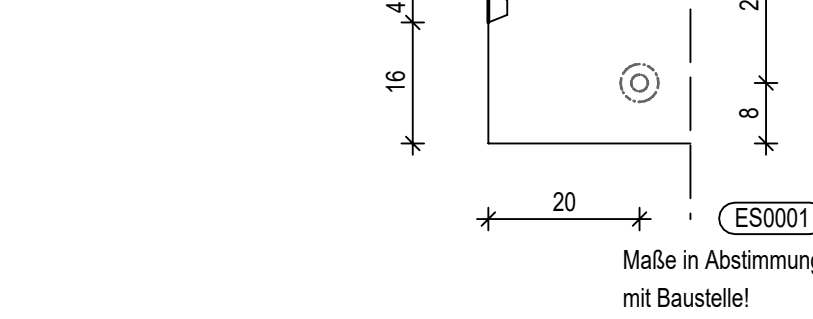

Angaben zur Vorspannung (sofortiger Verbund)

Zulassung:	Nr. 2-12.3-84
Typ:	0,5-Zahl-Litzen 83 mm ² (12,5 mm)
Spannstahlgüte:	ST 1660/1860
Anzahl:	8
Vorspannkraft:	P ₁₀₀ = 121 kN je Litze
Vorspannkraft Spannbett:	121 kN x 8 = 968 kN (Spannbett)
Länge:	14,89 m (ohne Überstand)
Gewicht:	0,73 kg/m
Gewicht (gesamt):	0,73 kg/m x 14,89 m x 8 = 86,958 kg
Umspannleistung:	10m, cube = 25,2 MPa

Längen DFOS

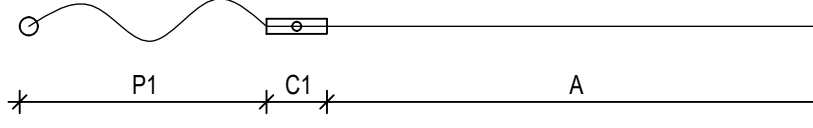

Einbauteile

Pos.	Anzahl	Bezeichnung
DFOS12	1	EpiloxSensor 3,0 m R. BDM C2+0,19m; A=14,48m; C1+0,13m; P1+2,64m
DFOS13	1	EpiloxSensor 1,0 m R. BDM C2+0,19m; A=14,48m; C1+0,13m; P1+2,64m
DFOS53	1	3D Sensor C2+0,19m; A=14,88m; C1+0,13m; P1+2,64m
DFOS57	1	Solllos Temperatur BRUSENS C2+0,19m; A=14,48m; C1+0,13m; P1+2,64m
E6612	8	Kobold M16 + Gewindestange mit M16 Schrauben
ES0001	4	Abschalhülse D&W 15 mm L = 70mm
ES0002	13	Betomax Kobold B 15-FB
T0114	15	Schraubenanker RD12 60mm
T0146	4	Flachstahlanker RD24 54mm
T0389	2	Drahtseilbeschläufe 5,2 verz.
TB00X	5	Thermosensor Typ K, TB028 - TB030

Schalungszeichen:	1	2	
-------------------	---	---	---	---	---	---	---	---	---	----	----	-----	-----	