Schal- und Bewehrungsplan Endquerträger Feld 3 Achse 40

Schalung

Draufsicht

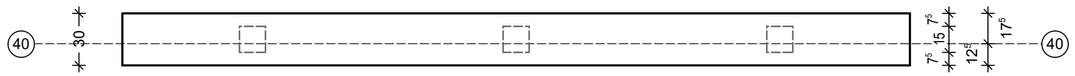

Ansicht

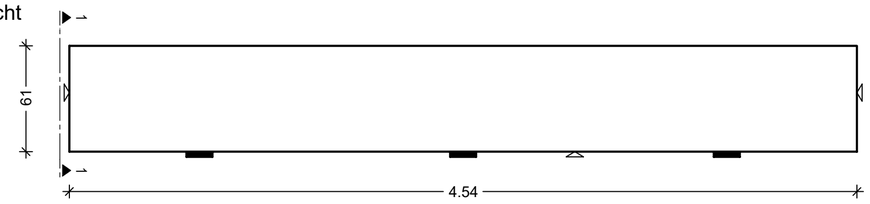

Bewehrung

Draufsicht

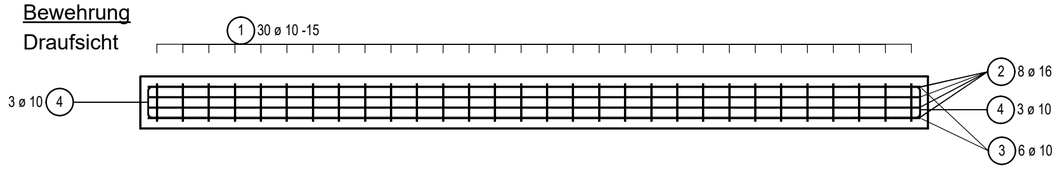

Ansicht

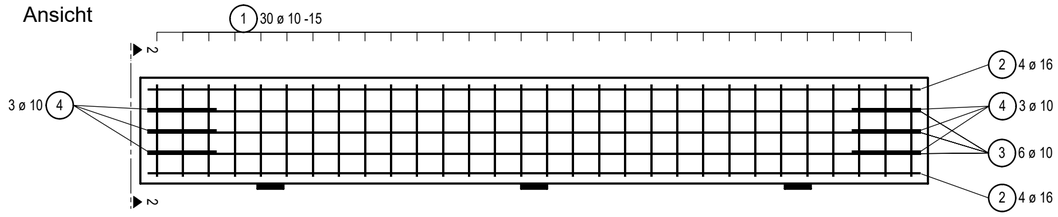

Schnitt 1 - 1

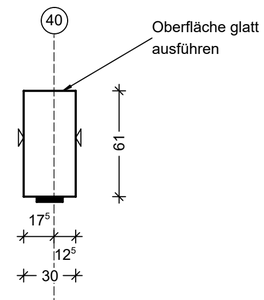

Schnitt 2 - 2

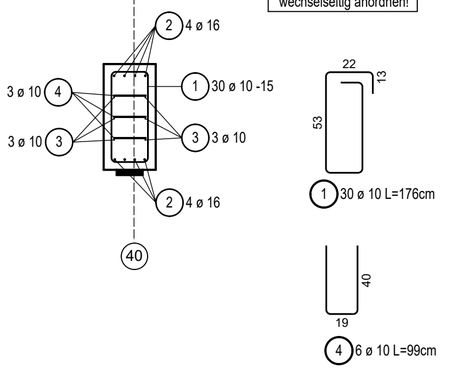

Detail Anschluss an Träger Feld 3

M 1:10

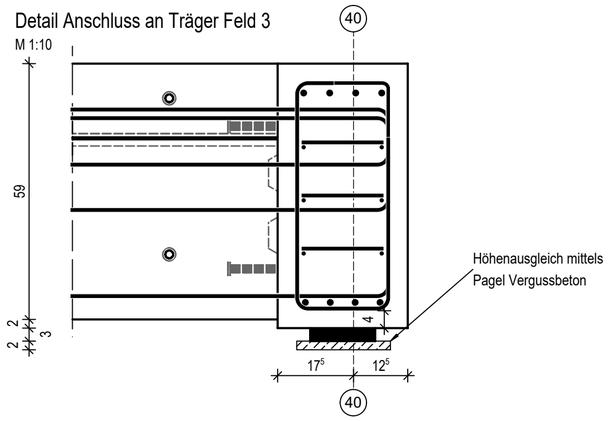

Übersicht Lage Endquerträger

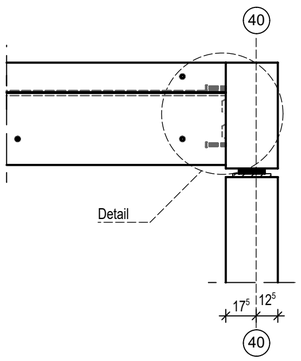

Stabliste

Pos.	Stck	ø [mm]	Einzel Länge [m]	Gesamt Länge [m]	Masse [kg]
1	30	10	1.76	52.80	32.58
2	8	16	4.46	35.68	56.37
3	6	10	4.46	26.76	16.51
4	6	10	0.99	5.94	3.66

Gesamtmasse : 109.13

Schalungszeichen:

Schalung | Waschbeton | gestrahlt

(1) Einfüllseite | gesäuert | Strukturschalung/Matrize

1. abgezogen/verreiben
2. geglättet
3. sauber geglättet

(M) Maschinen geglättet | Lammfell gewalzt | Kanten/ Fasen

BAUSTOFFANGABEN (Planspezifisch)

Bauteile	Expositionsklassen	Beton	Δc	min c	nom c
	XC4, XF	C50/60	15 mm	25 mm	40 mm
Bereiche mit höheren Betonfestigkeiten beachten					

Betonstahl : BSt 500 M(B) BSt 500 S(B) Standardfase: 1,0/ 1,0 cm

Biegen von Betonstählen nach DBV-Merkblatt "Betondeckung und Bewehrung"

Bei der Bestimmung des Biegerollendurchmessers D min ist DIN EN 1992-1-1/NA Tabelle 8.1DE zu beachten und nach der bautechnischen Funktion der Biegung zu unterscheiden:

A) Mindestwerte der Biegerollendurchmesser für Schrägstäbe oder andere gebogene Stäbe

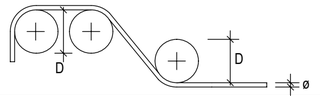

Mindestwerte der Betondeckung rechtwinklig zur Krümmungsebene	Biegerollendurchmesser D [mm]
> 100 mm und > 7 ø	D min = 10 ø
> 50 mm und > 3 ø	D min = 15 ø
< 50 mm oder < 3 ø	D min = 20 ø

Biegung nach A)
zur Herstellung und Überprüfung ist der erforderliche Biegerollendurchmesser immer anzugeben und zwar an der Biegeform im Bewehrungsplan und auf der Stabliste.

B) Mindestwerte der Biegerollendurchmesser für Haken, Winkelhaken, Schlaufen, Bügel

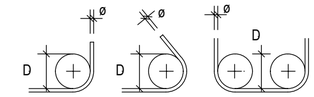

Stabdurchmesser ø	Biegerollendurchmesser D [mm]
< 20	D min = 4 ø
> 20	D min = 7 ø

Biegung nach B)
wird an der Biegeform weder im Bewehrungsplan noch auf der Stabliste ein Biegerollendurchmesser angegeben, so ist D min in Abhängigkeit von der obigen Tabelle zu entnehmen.

Bei Betonstahlmatten und geschweißter Bewehrung, die nach dem Schweißen gebogen werden, ist zu-

Biegerollendurchmesser gelten nur, wenn a > 4 ø
(a=Abstand der Schweißung vom Krümmungsbeginn).

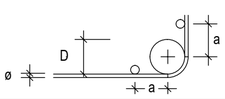

Ausführung von Bügelschlössern bei Stützen:

INDEX	DATUM	GEZ.	ART DER ÄNDERUNGEN / INHALT
e			
d			
c			
b			
a			

Werkplanung

Bauherr:

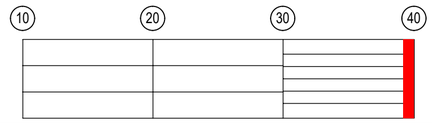

Bauvorhaben:
Demonstratorbauwerk IDA-KI

Bauteil:
Endquerträger Feld 3 Achse 40

Planung:

Hentschke
Betonfertigteilwerk Bautzen
Hentschke Bau GmbH
Hoyerswerdaer Straße 42
02625 Bautzen
Tel.: 03591 6703- Def
Fax: 03591 6703-42

Projekt-Nr.: 187.215 / 50 - 999 - 035

Beton: C50/60 Rez.Nr.: 701.1	Expositionsklasse: XC4, XF	Stückzahl: 1	St.-verbrauch kg/m³	stat.-Pos./ Bez. Arch. EQT 40	Maßstab: M 1 : 25
Betondeckung: 4 cm	Oberfläche: siehe Zeichnung	gezeichnet:	Erstelldatum: 07.11.2023	Ersteller: F. Collin	Plan-Nr.: EQT 40 / Index: 0
Volumen: 0.831 m³ Gewicht: 2.08 t	Beschichtung:	~~Mit dem Prüfexemplar gleichgestellt und zur Ausführung freigegeben:~~			