



Schalplan Unterbauten Achse 10

Schalung
Draufsicht

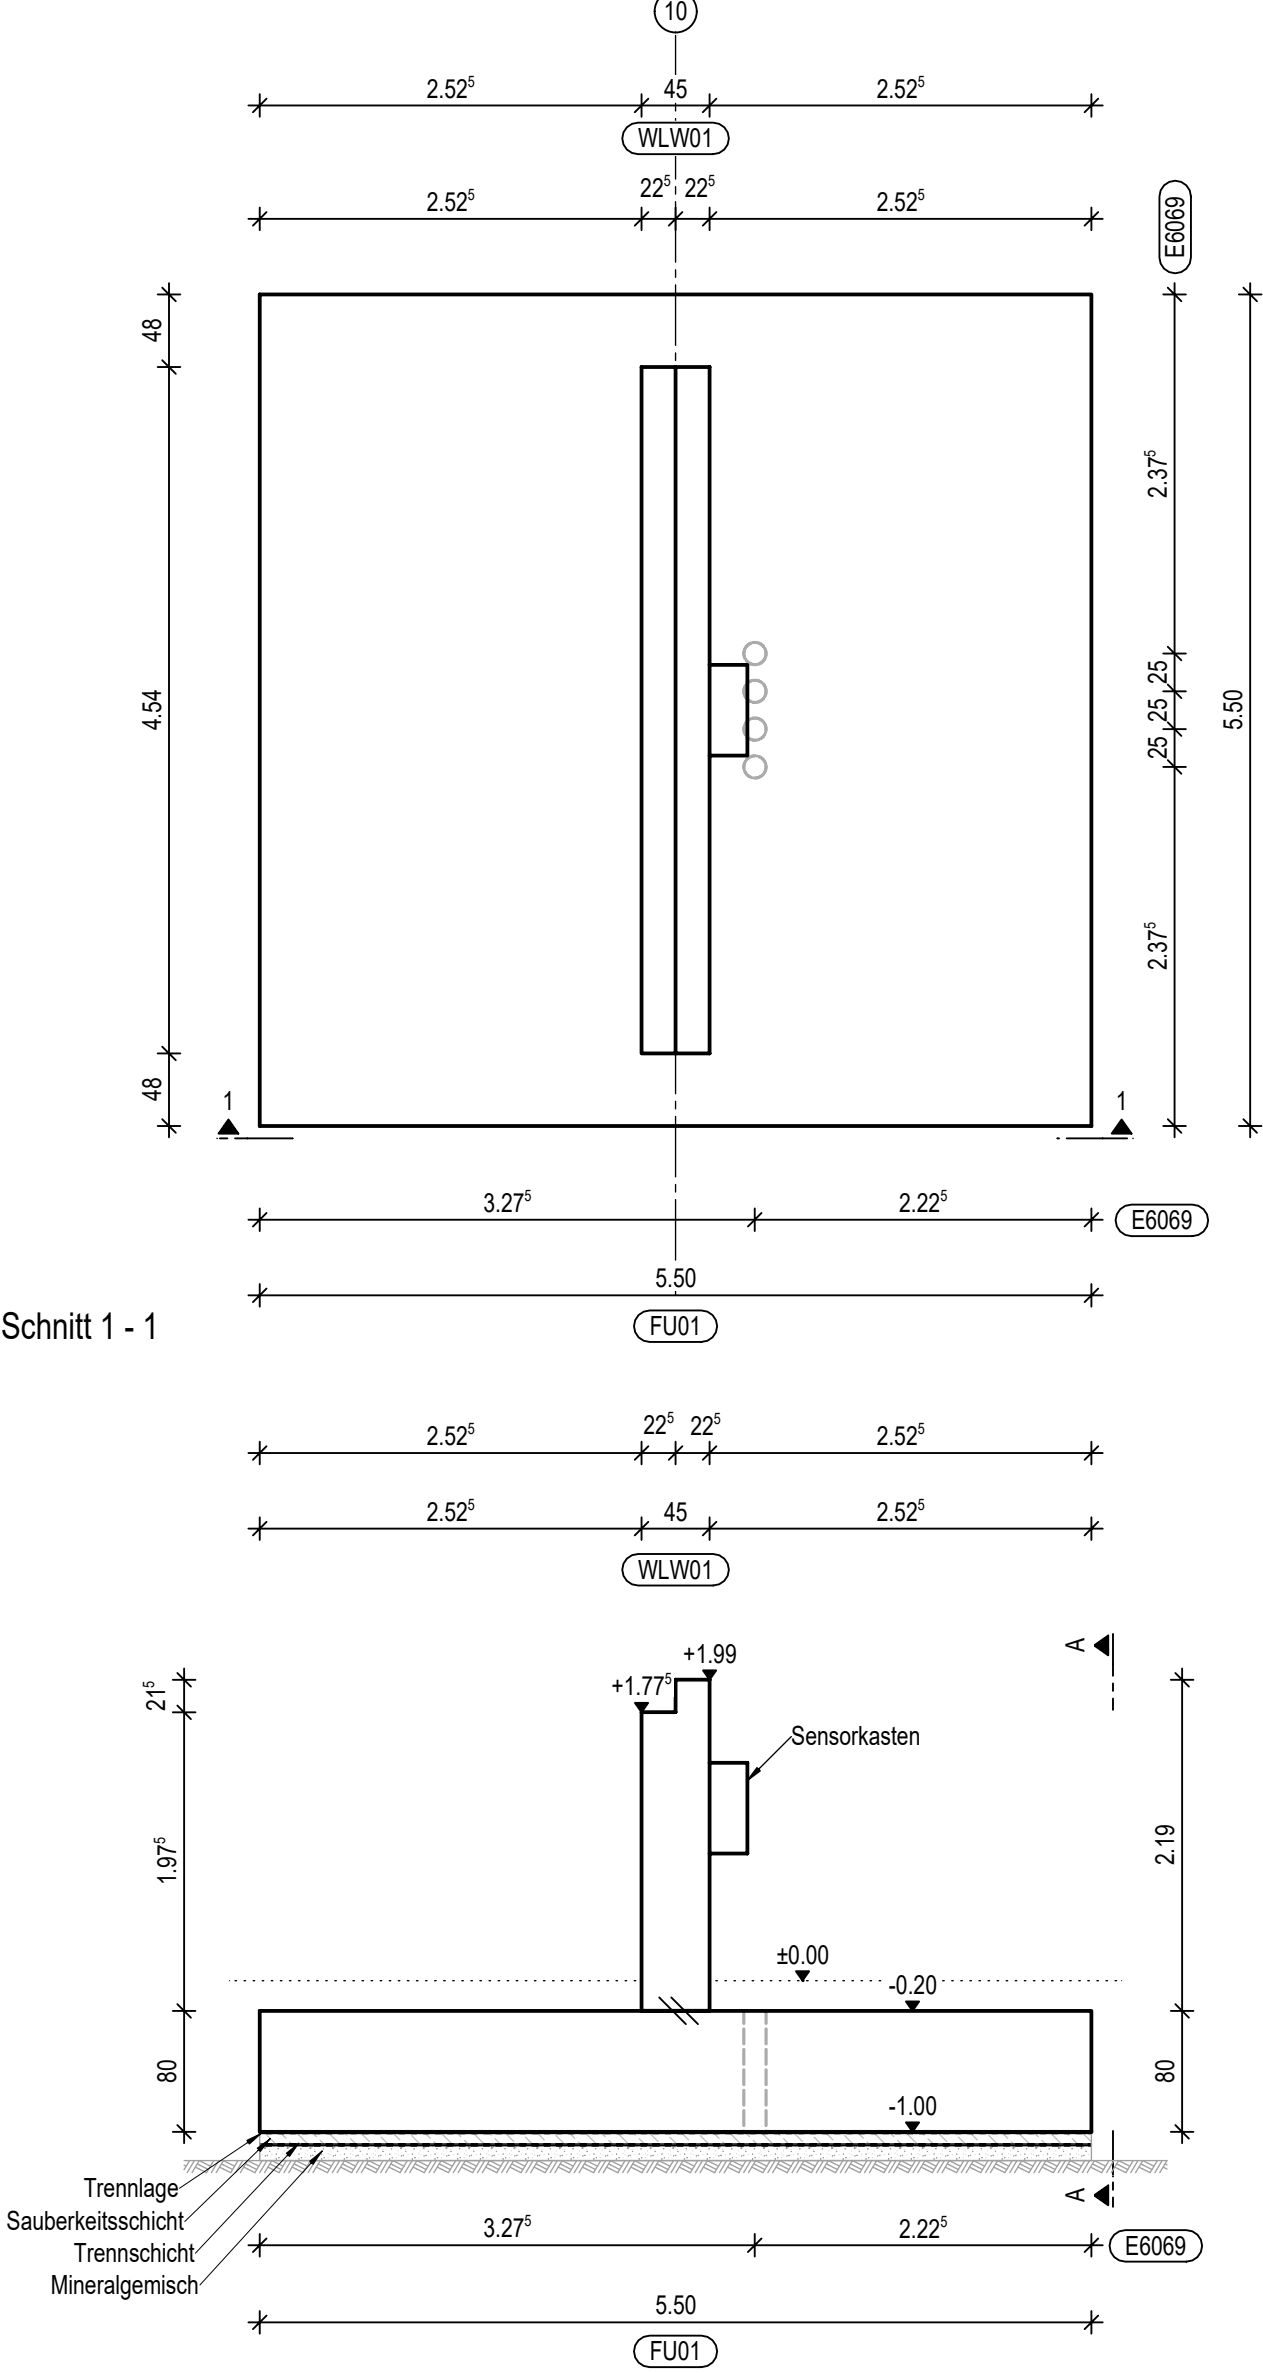

Übersicht 3-Feld-Brücke
M1:200

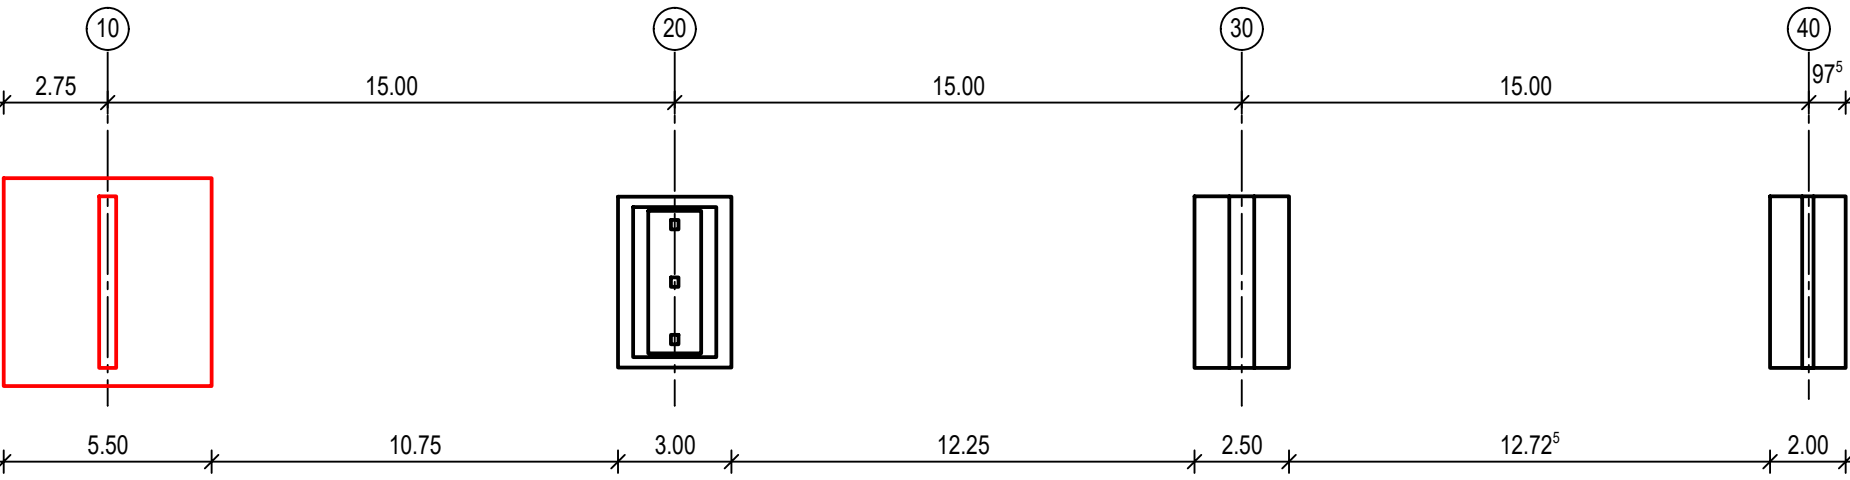

Einbauteile

Pos.	Anzahl [Stk]	Bezeichnung
E6069	4	Montagerohr, KG-Rohr DN150, l=500mm

BAUSTOFFANGABEN (Planspezifisch)

Bauteile	Expositionsklassen	Beton	Δs	min c	nom c
Fundament (FU01)	XC2	C30/37			3,5cm
Widerlagerwand (WLW01)	XC4	C30/37			4,0cm
Bereiche mit höheren Betonfestigkeiten beachten					

Betonstahl : BSt 500 M(B) Standardfase: 1,0/ 1,0 cm
BSt 500 S(B)

Schalungszeichen:					
▽	Schalung	①	abgezogen/verreiben	Ⓜ	Maschinen geglättet
▽	Waschbeton	②	geglättet	⌋	Lammfell gewalzt
▽	gestrahlt	③	sauber geglättet	⌋	Kanten/ Fasen
▽			gesäuert		
▽			Strukturschalung/Matrize		

f			
e			
d			
c			
b			
a	11.07.2023	Graf	Freigabe
INDEX	DATUM	GEZ.	

Werkplanung

Bauherr:
Intern

Bauvorhaben:
IDA-KI
Errichtung einer 3-Feld-Brücke

Darstellung:
Schalplan Unterbauten Achse 10

Planung:

Hentschke
Betonfertigteilewerk Bautzen
Hentschke Bau GmbH
Hoyerswerdaer Straße 42
02625 Bautzen
Tel.: 03591 6703-
Fax: 03591 6703-42

Projekt-Nr.: XXXX-XX
50 - 999 - 035

gezeichnet: Graf

Datum: 03.07.2023


Unterschrift:

Maßstab: 1 : 50

Plan-Nr.
Planbezeichnung SP-UB10

a

Schnitt A - A

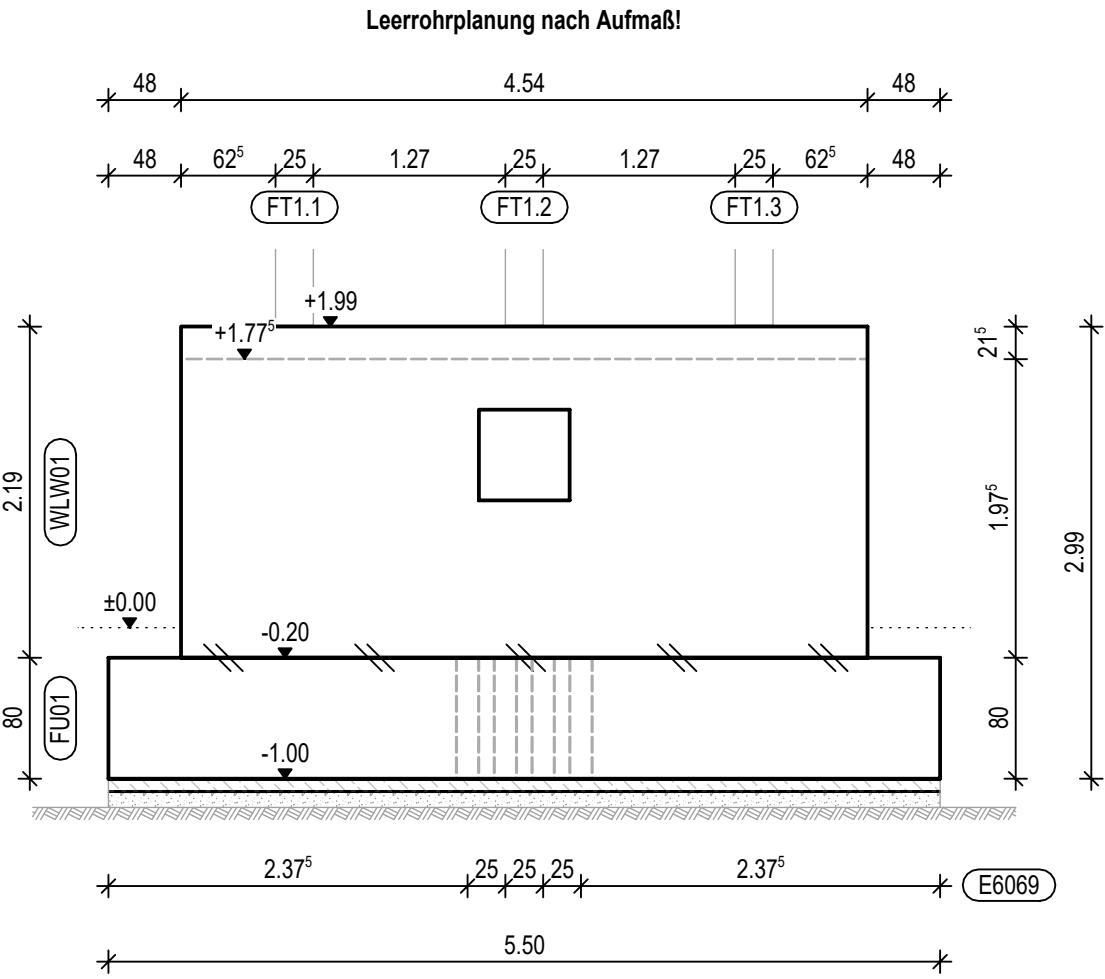

Positionsübersicht Fertigteile

Pos.	Anzahl [Stk.]	Volumen [m³]	E.-Gewicht [kg]	Bezeichnung
FU01	1	24.200	60500.00	Fundament Achse 10
WLW01	1	4.255	10636.37	Widerlagerwand Achse 10
Ges.-Anzahl:	2			
Ges.-Volumen:	28.455			
Ges.-Gewicht [kg]:	71136.00			