



Schalplan Unterbauten Achse 20


Draufsicht

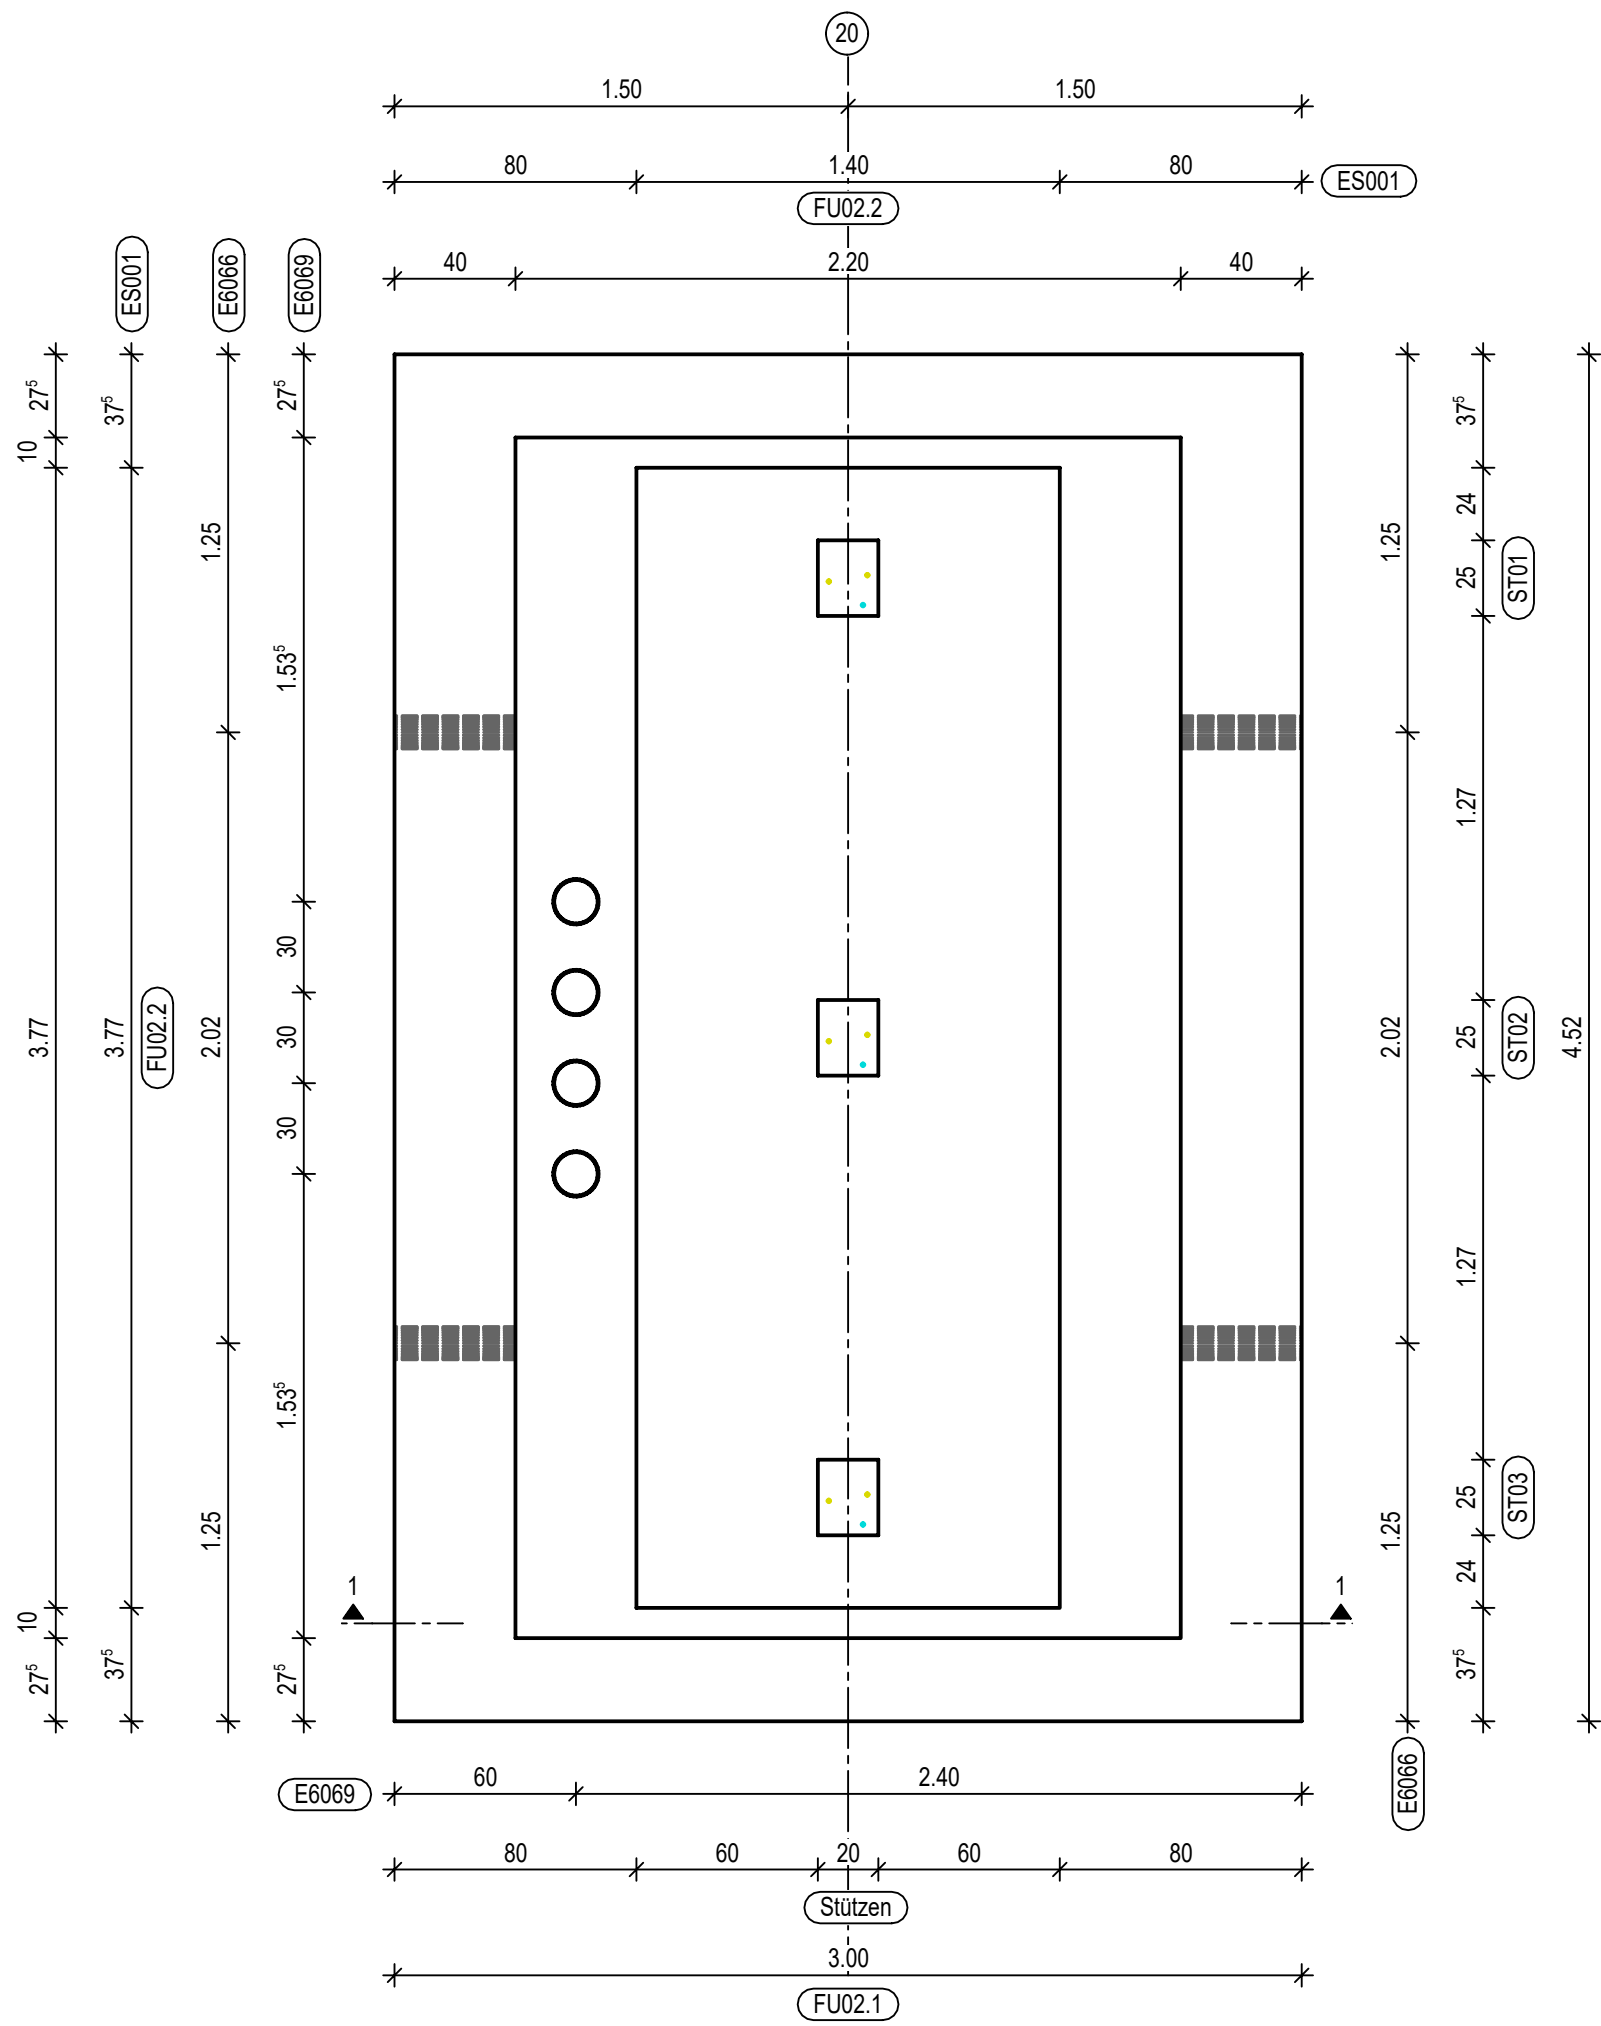


Schnitt 1 - 1

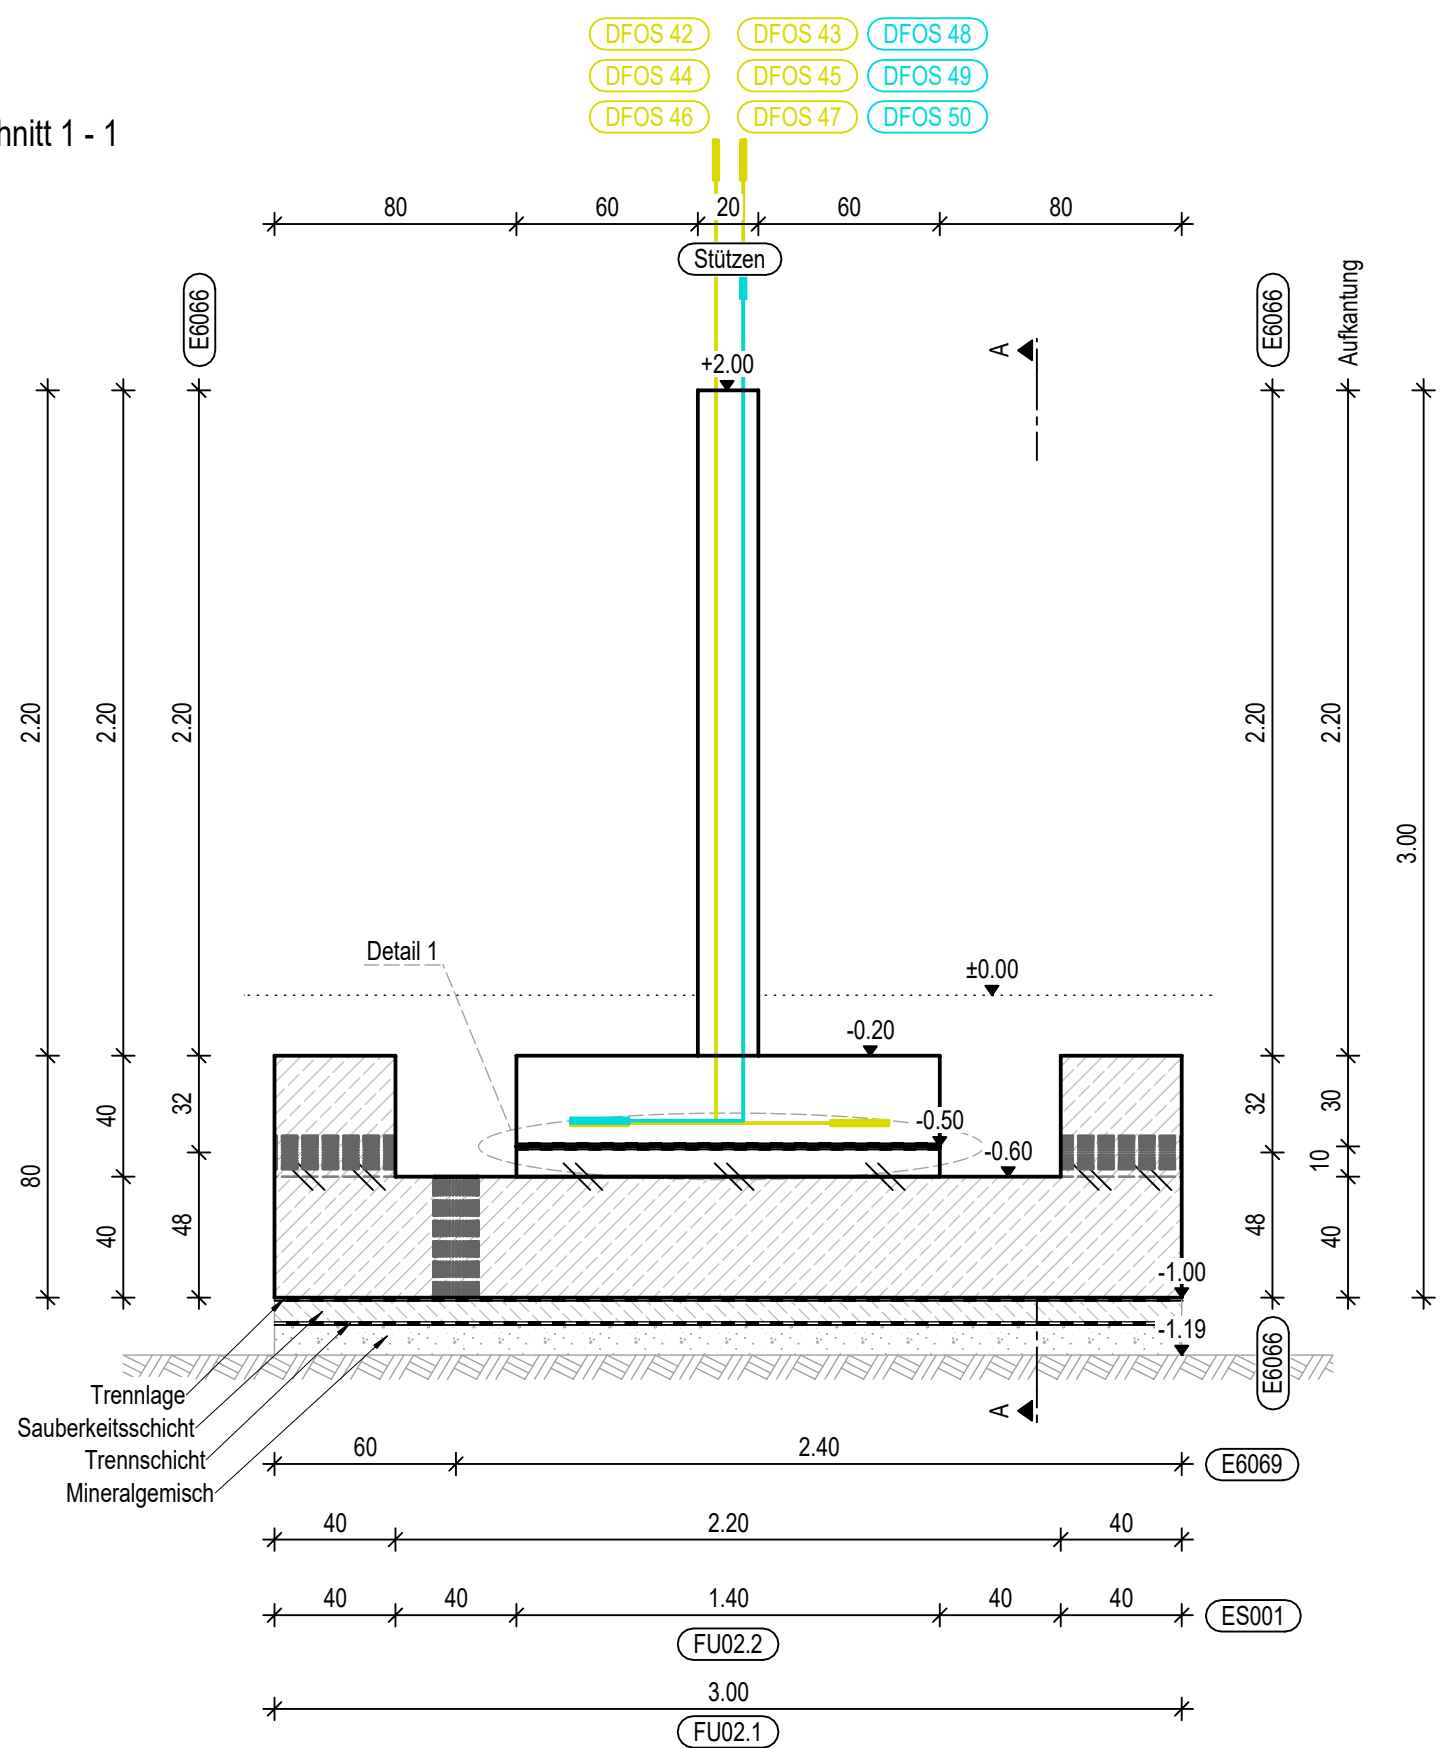

Detail 1
Großflächengleitfolie
M1:10
Oberfläche Aufkantung
FU02.1 Flügelgeglättet!

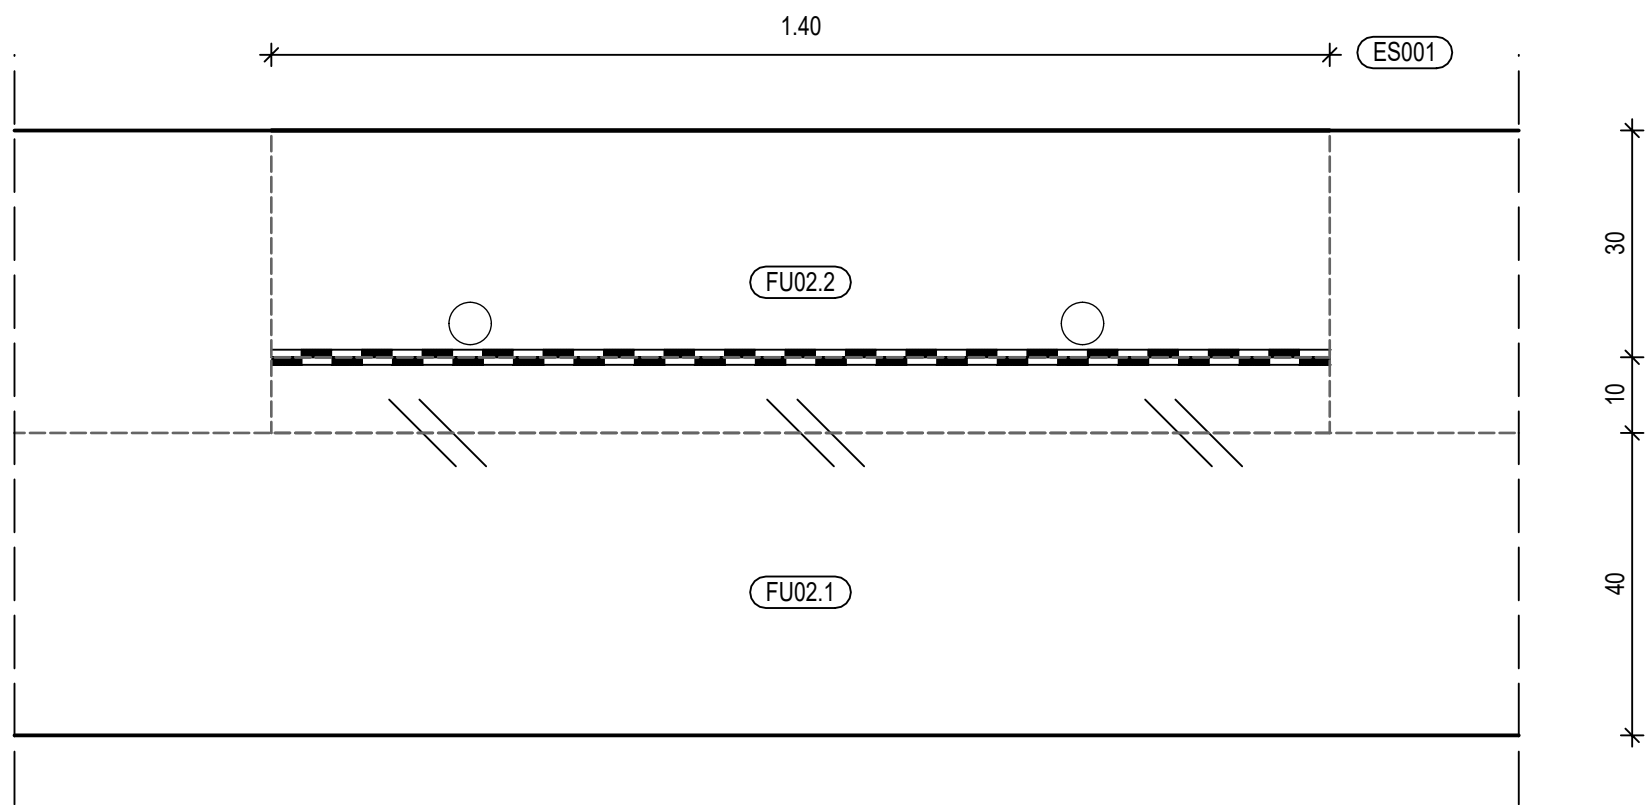


Schnitt A - A

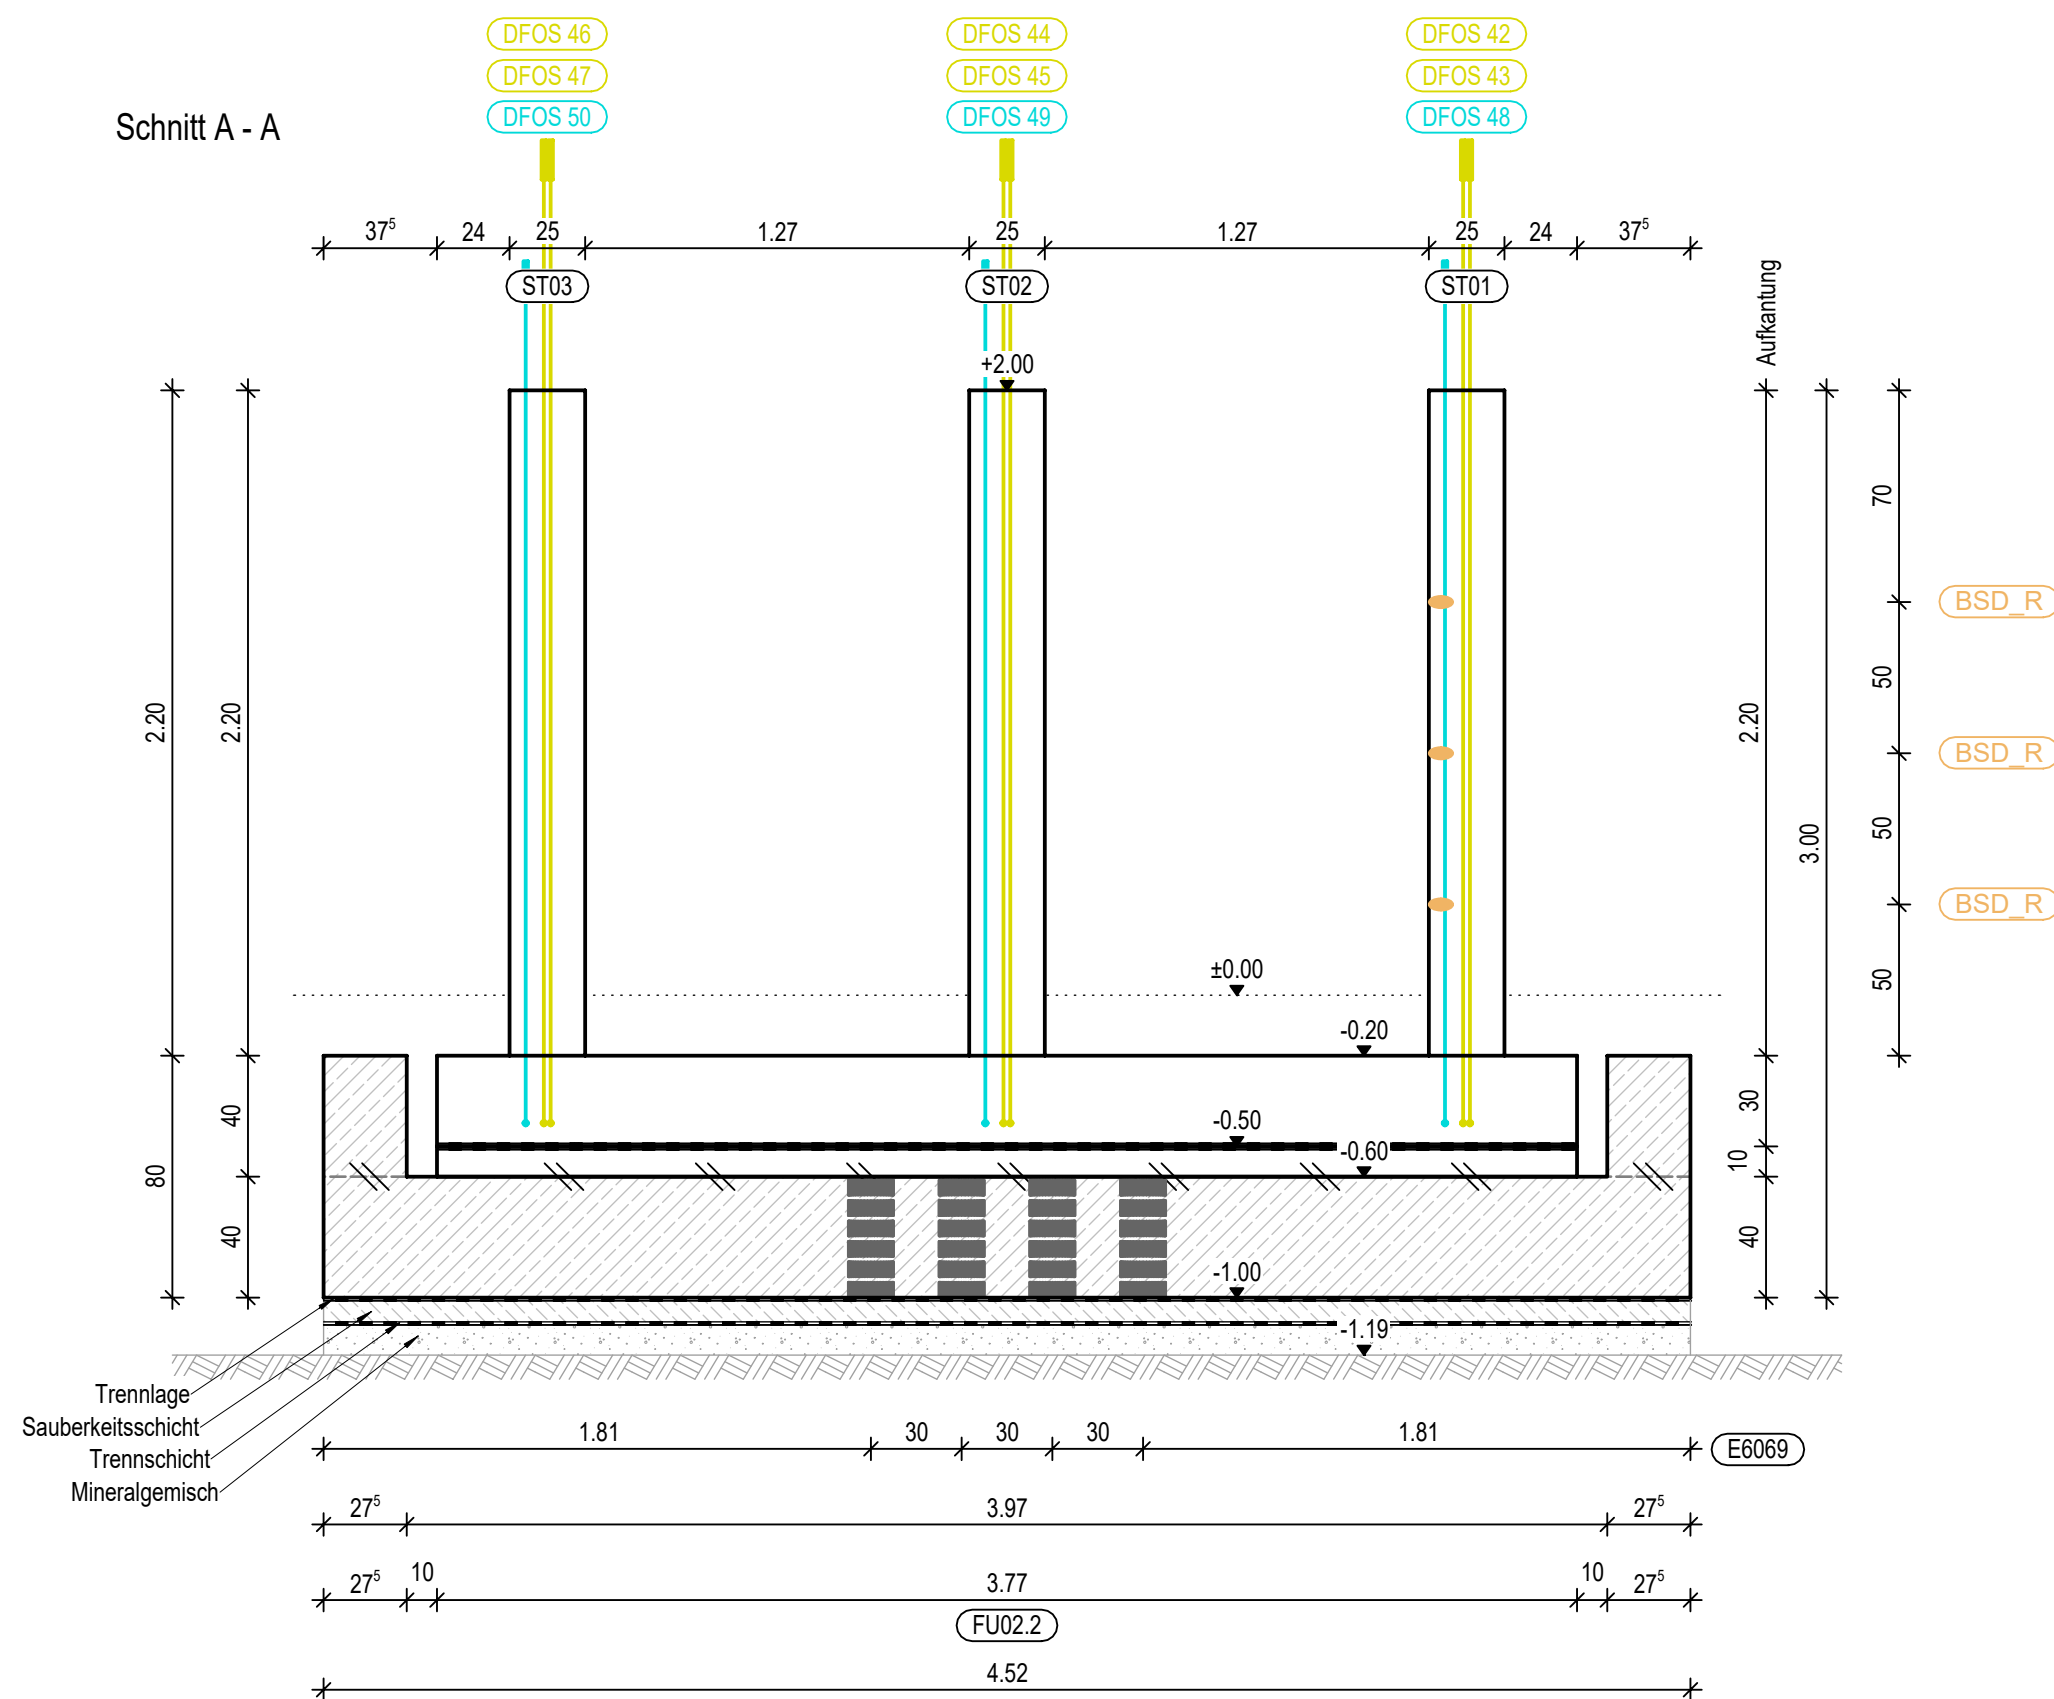

Übersicht 3-Feld-Brücke

M1:200

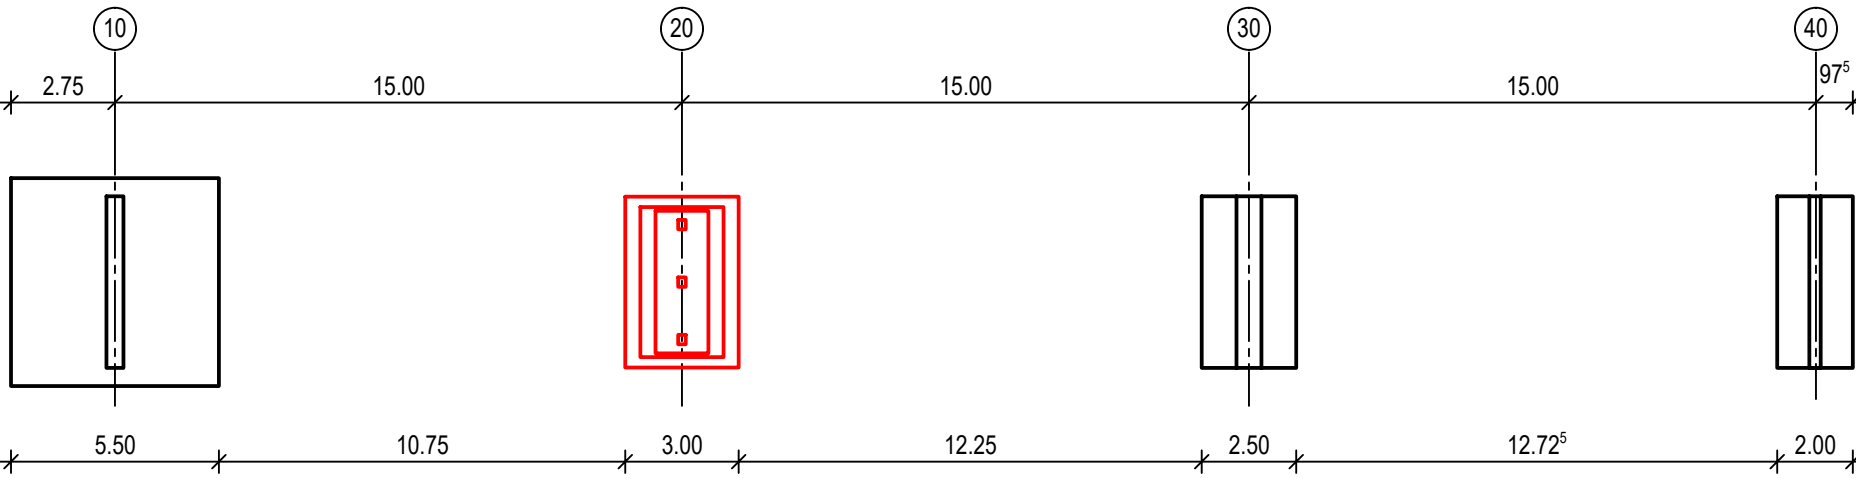

Einbauteile

Pos.	Anzahl [Stk]	Bezeichnung
BSD_R	3	Stahldehnung (Redundanz)
DFOS 42	1	EpsilonSensor 3,0 m.R. UAKd C2=0,19m; A=3,50m; C1=0,13m; P1=3,50m
DFOS 43	1	EpsilonSensor 3,0 m.R. UAKd C2=0,19m; A=3,50m; C1=0,13m; P1=4,20m
DFOS 44	1	EpsilonSensor 3,0 m.R. UAKd C2=0,19m; A=3,50m; C1=0,13m; P1=2,10m
DFOS 45	1	EpsilonSensor 3,0 m.R. UAKd C2=0,19m; A=3,50m; C1=0,13m; P1=3,00m
DFOS 46	1	EpsilonSensor 3,0 m.R. UAKd C2=0,19m; A=3,50m; C1=0,13m; P1=3,50m
DFOS 47	1	EpsilonSensor 3,0 m.R. UAKd C2=0,19m; A=3,50m; C1=0,13m; P1=4,20m
DFOS 48	1	EpsilonSensor 1,0 o.R. UAKs C2=0,19m; A=3,10m; C1=0,13m; P1=3,75m
DFOS 49	1	EpsilonSensor 1,0 o.R. UAKs C2=0,19m; A=3,10m; C1=0,13m; P1=3,35m
DFOS 50	1	EpsilonSensor 1,0 o.R. UAKs C2=0,19m; A=3,10m; C1=0,13m; P1=3,75m
E6066	4	PVC-Rohr DN100, l=400mm
E6069	4	Montagerohr, KG-Rohr DN150, l=400mm
ES001	1	Großflächengleitfolie Typ RUKK 3,77m x 1,40m

Positionsübersicht Fertigteile

Pos.	Anzahl [Stk.]	Volumen [m³]	E.-Gewicht [kg]	Bezeichnung
FU02.1	1	7.882	19705.50	Fundament Achse 20
FU02.2	1	1.583	3958.50	Zwischenfundament Achse 20
ST01	1	0.110	275.00	Stütze Achse 20
ST02	1	0.110	275.00	Stütze Achse 20
ST03	1	0.110	275.00	Stütze Achse 20
Ges.-Anzahl:		5		
Ges.-Volumen:		9.796		
Ges.-Gewicht [kg]:		24488.50		

BAUSTOFFFANGABEN (Planspezifisch)

Bauteile	Expositionsklassen	Beton	z _{st}	min c	nom c
Fundamente (FU02.1) (FU02.2)	XC2	C30/37			3,5cm
Stützen (ST01) (ST02) (ST03)	XC4	C50/60			3,5cm
Bereiche mit höheren Betonfestigkeiten beachten					
Betonstahl : BSt 500 M(B) Standardfase: 1,0/ 1,0 cm BSt 500 S(B)					
Schalungszeichen:					
Schalung ① abgezogen/verreiben ② geglättet ③ sauber geglättet ④ gesäuert ⑤ gestrahlt ⑥ gestrahlt ⑦ gestrahlt ⑧ gestrahlt ⑨ gestrahlt ⑩ gestrahlt ⑪ gestrahlt ⑫ gestrahlt ⑬ gestrahlt ⑭ gestrahlt ⑮ gestrahlt ⑯ gestrahlt ⑰ gestrahlt ⑱ gestrahlt ⑲ gestrahlt ⑳ gestrahlt ㉑ gestrahlt ㉒ gestrahlt ㉓ gestrahlt ㉔ gestrahlt ㉕ gestrahlt ㉖ gestrahlt ㉗ gestrahlt ㉘ gestrahlt ㉙ gestrahlt ㉚ gestrahlt ㉛ gestrahlt ㉜ gestrahlt ㉝ gestrahlt ㉞ gestrahlt ㉟ gestrahlt ㊱ gestrahlt ㊲ gestrahlt ㊳ gestrahlt ㊴ gestrahlt ㊵ gestrahlt ㊶ gestrahlt ㊷ gestrahlt ㊸ gestrahlt ㊹ gestrahlt ㊺ gestrahlt ㊻ gestrahlt ㊼ gestrahlt ㊽ gestrahlt ㊾ gestrahlt ㊿ gestrahlt					
f					
e					
d					
c					
b	12.09.2023	Collin	Sensorik		
a	11.07.2023	Graf	Freigabe		
INDEX	DATUM	GEZ.			

Werkplanung

Bauherr:
Intern

Bauvorhaben:
IDA-KI
Errichtung einer 3-Feld-Brücke

Darstellung:

Schalplan Unterbauten Achse 20

Planung:

Hentschke
Betonfertigteilewerk Bautzen
Hentschke Bau GmbH
Hoyerswerdaer Straße 42
02625 Bautzen
Tel.: 03581 6703-
Fax: 03581 6703-42

Projekt-Nr.: 187.215

50 - 999 - 035

gezeichnet: Collin

Datum: 12.09.2023

Unterschrift:

Maßstab:

1 : 25

Plan-Nr.

Planbezeichnung SP-UB20

b