




Schalplan Unterbauten Achse 40
Schalung
Draufsicht

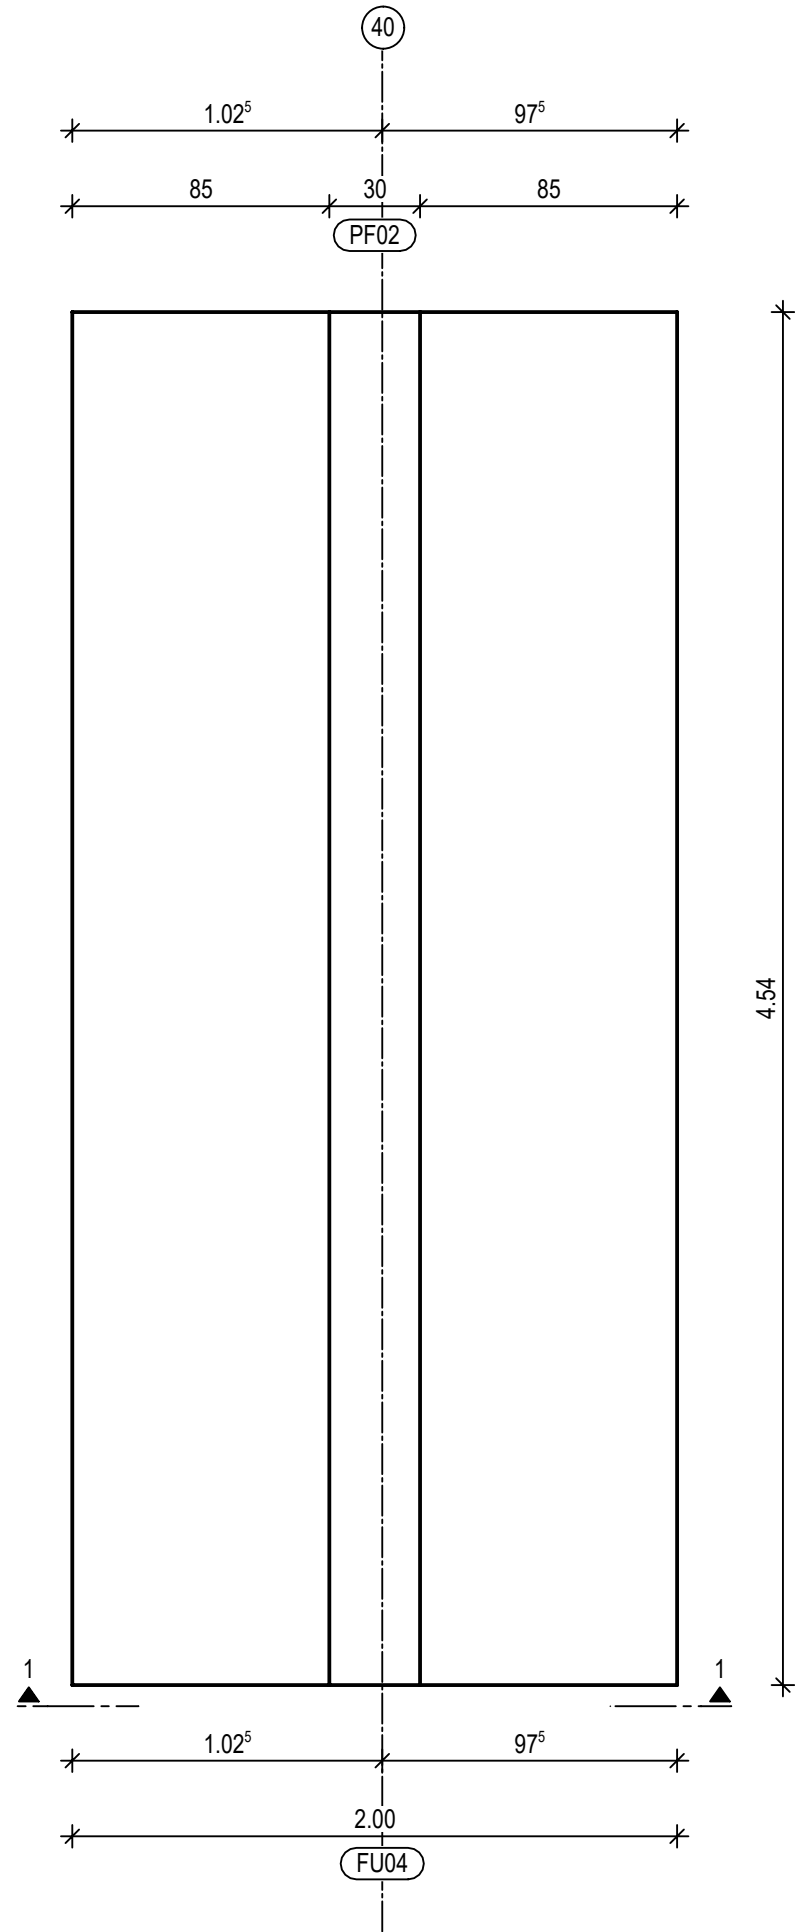


Schnitt 1 - 1

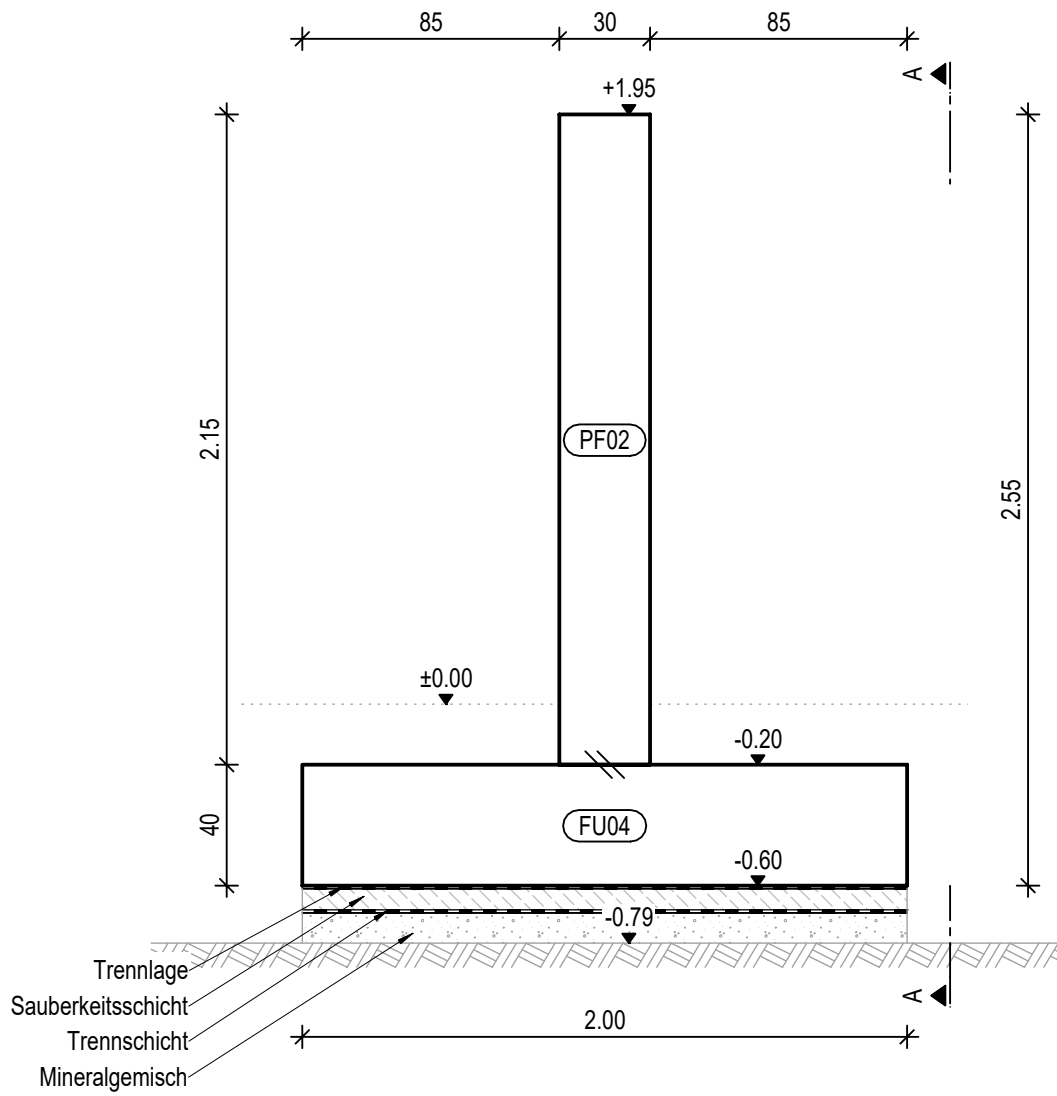

Schnitt A - A

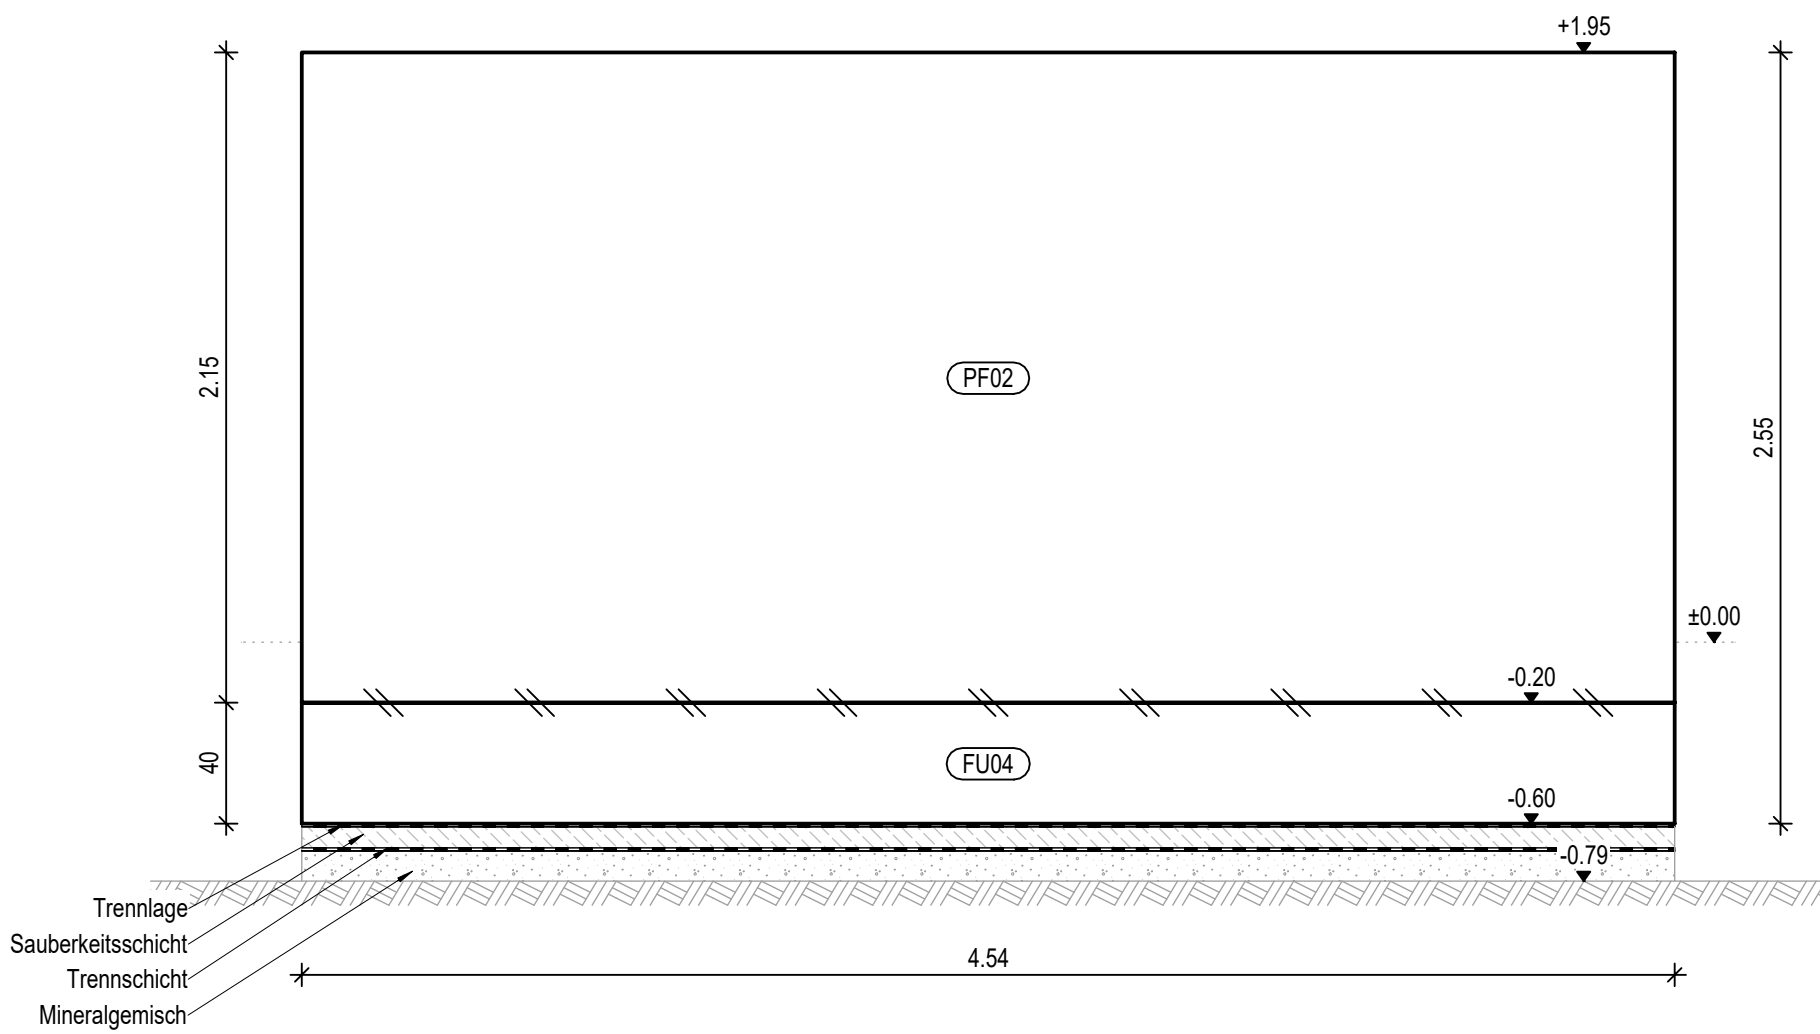

Übersicht 3-Feld-Brücke
M1:200

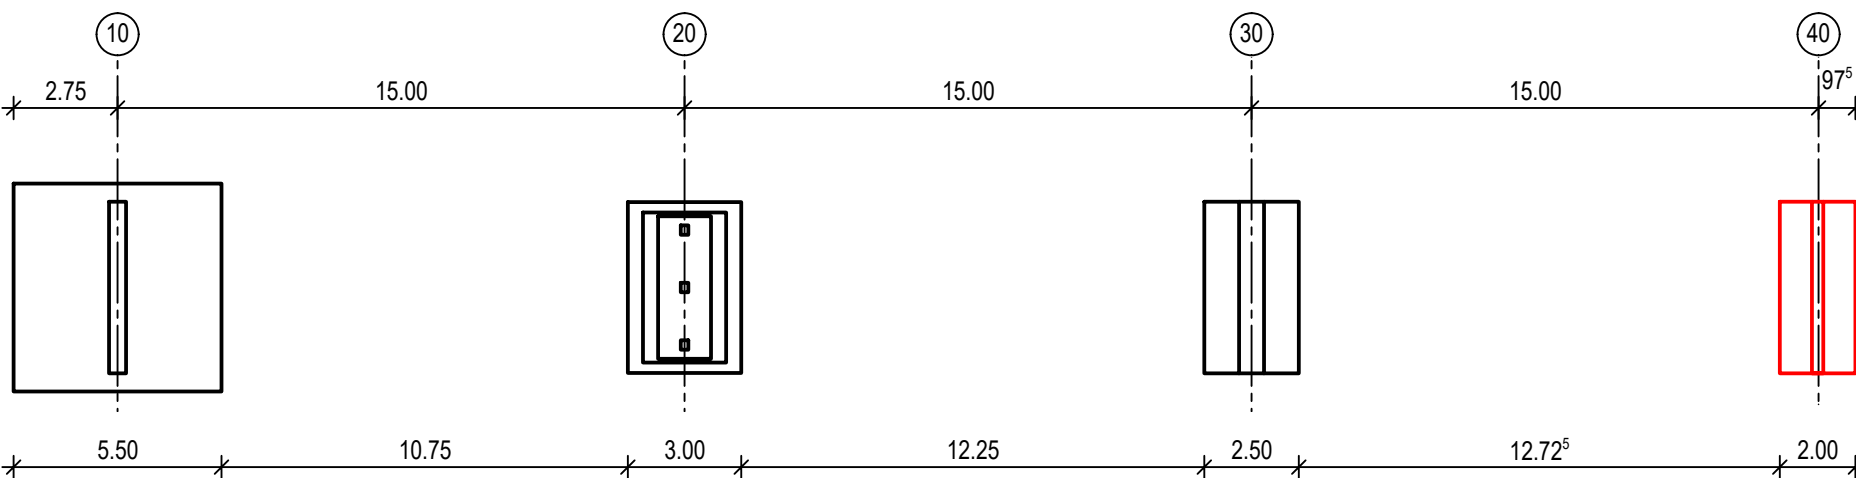

Positionsübersicht Fertigteile

Pos.	Anzahl [Stk.]	Volumen [m³]	E.-Gewicht [kg]	Bezeichnung
FU04	1	3.632	9080.00	Fundament Achse 40
PF02	1	2.928	7320.75	Pfeiler Achse 40
Ges.-Anzahl: 2 Ges.-Volumen: 6.560 Ges.-Gewicht [kg]: 16400.70				

BAUSTOFFFANGABEN (Planspezifisch)

Bauteile	Expositions-Klassen	Beton	Δs	min c	nom c
Fundament (FU04)	XC2	C30/37			4,5cm
Pfeiler (PF02)	XC4	C30/37			3,5cm
Bereiche mit höheren Betonfestigkeiten beachten					
Betonstahl : BSt 500 M(B) Standardfaser: 1,0/ 1,0 cm BSt 500 S(B)					
f					
e					
d					
c					
b					
a	11.07.2023	Graf	Freigabe		
INDEX	DATUM	GEZ.			

Werkplanung		Planung: Hentschke Betonfertigteilewerk Bautzen Hentschke Bau GmbH Hoyerswerdaer Straße 42 02625 Bautzen Tel.: 03591 6703- Fax: 03591 6703-42	
		Projekt-Nr.: XXXX-XX 50 - 999 - 035	
Bauherr: Intern		gezeichnet:	Graf
Bauvorhaben: IDA-KI Errichtung einer 3-Feld-Brücke		Datum:	06.07.2023
Darstellung: Schalplan Unterbauten Achse 40		Unterschrift:	
		Maßstab:	1 : 50
		Plan-Nr.	
		Planbezeichnung SP-UB40	a