




Montageplan 3-Feld-Brücke
Draufsicht

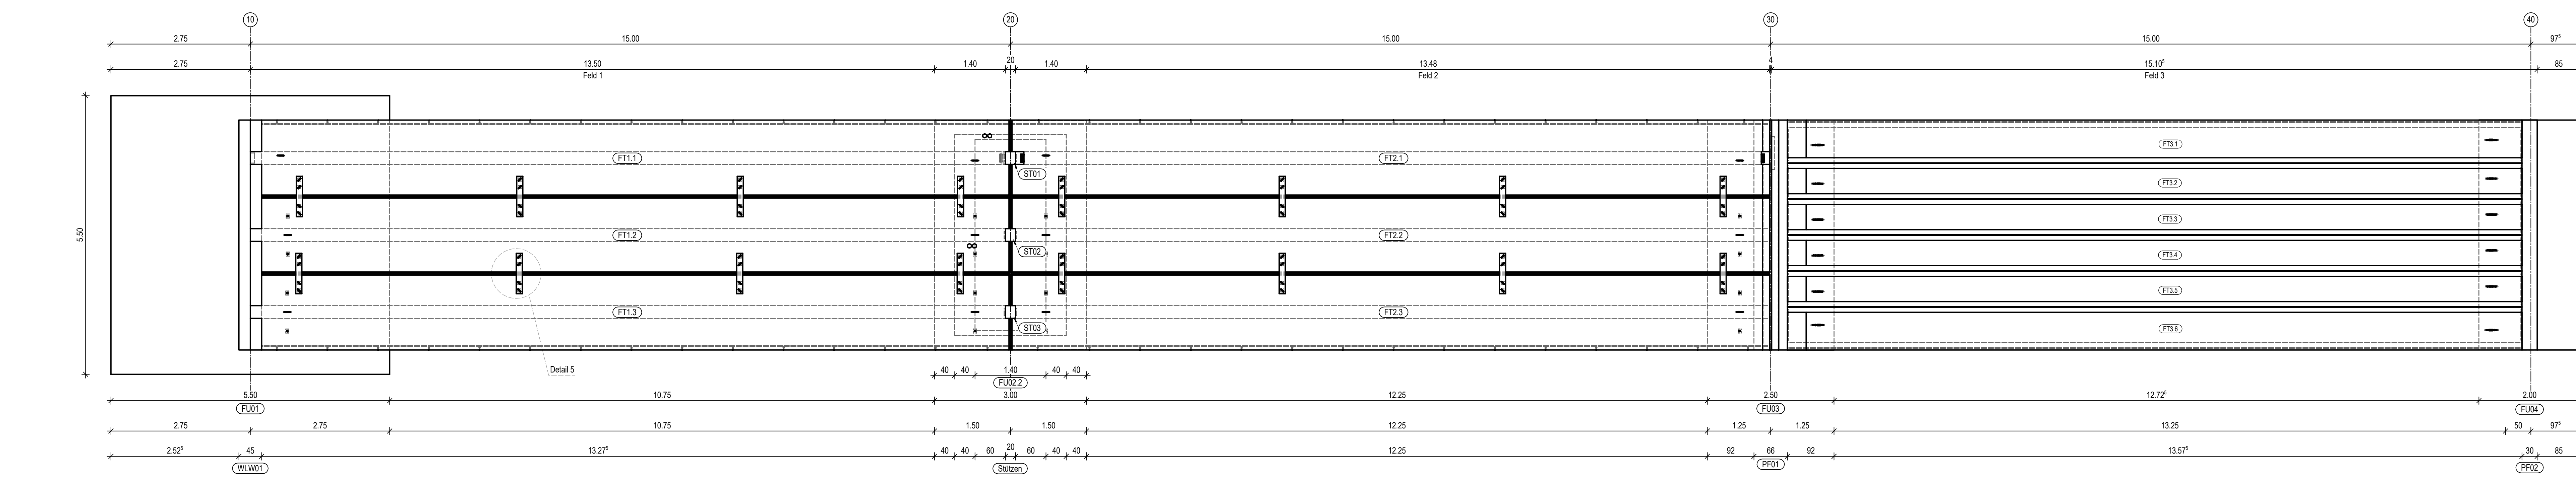


Ansicht (mit Ortbetonergänzung)

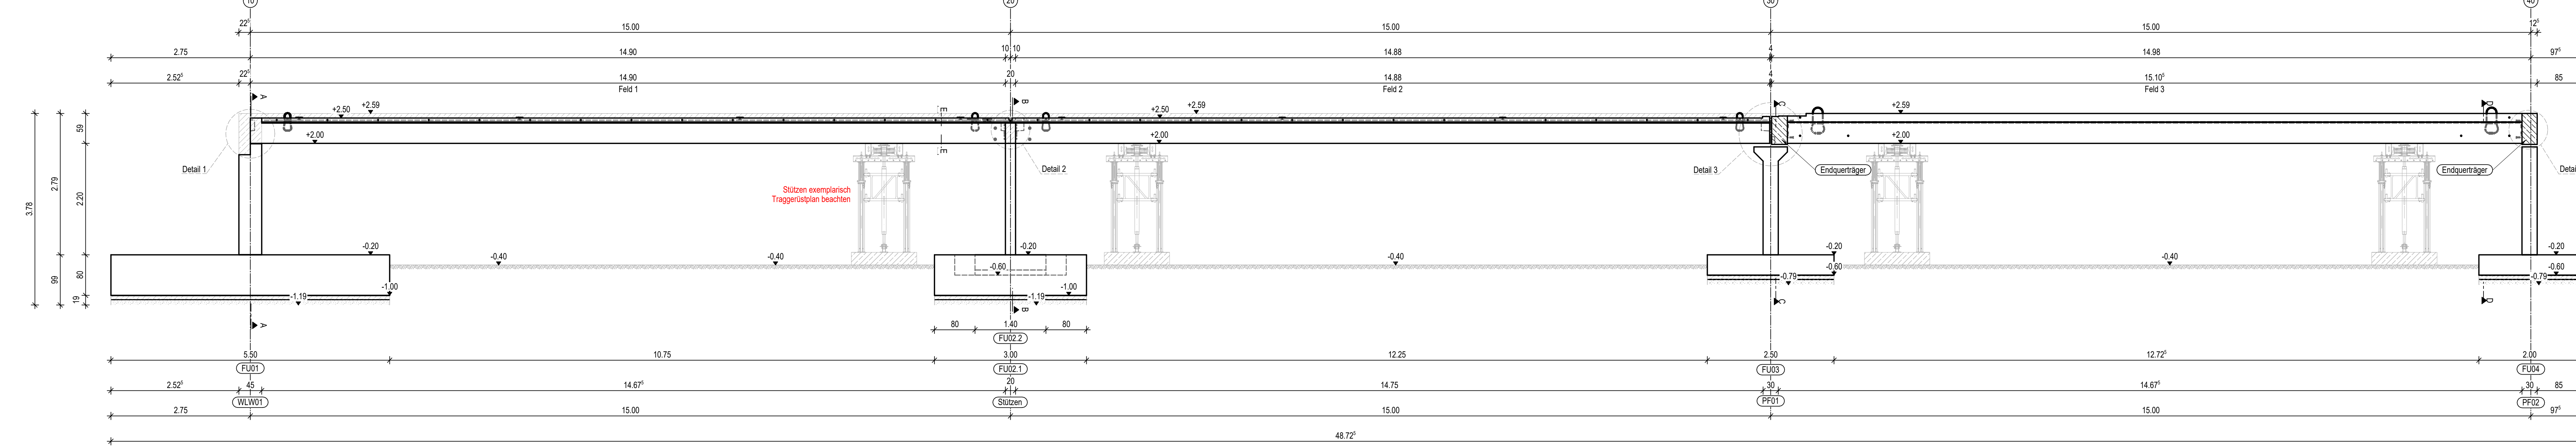


Schnitt A - A
M1:25

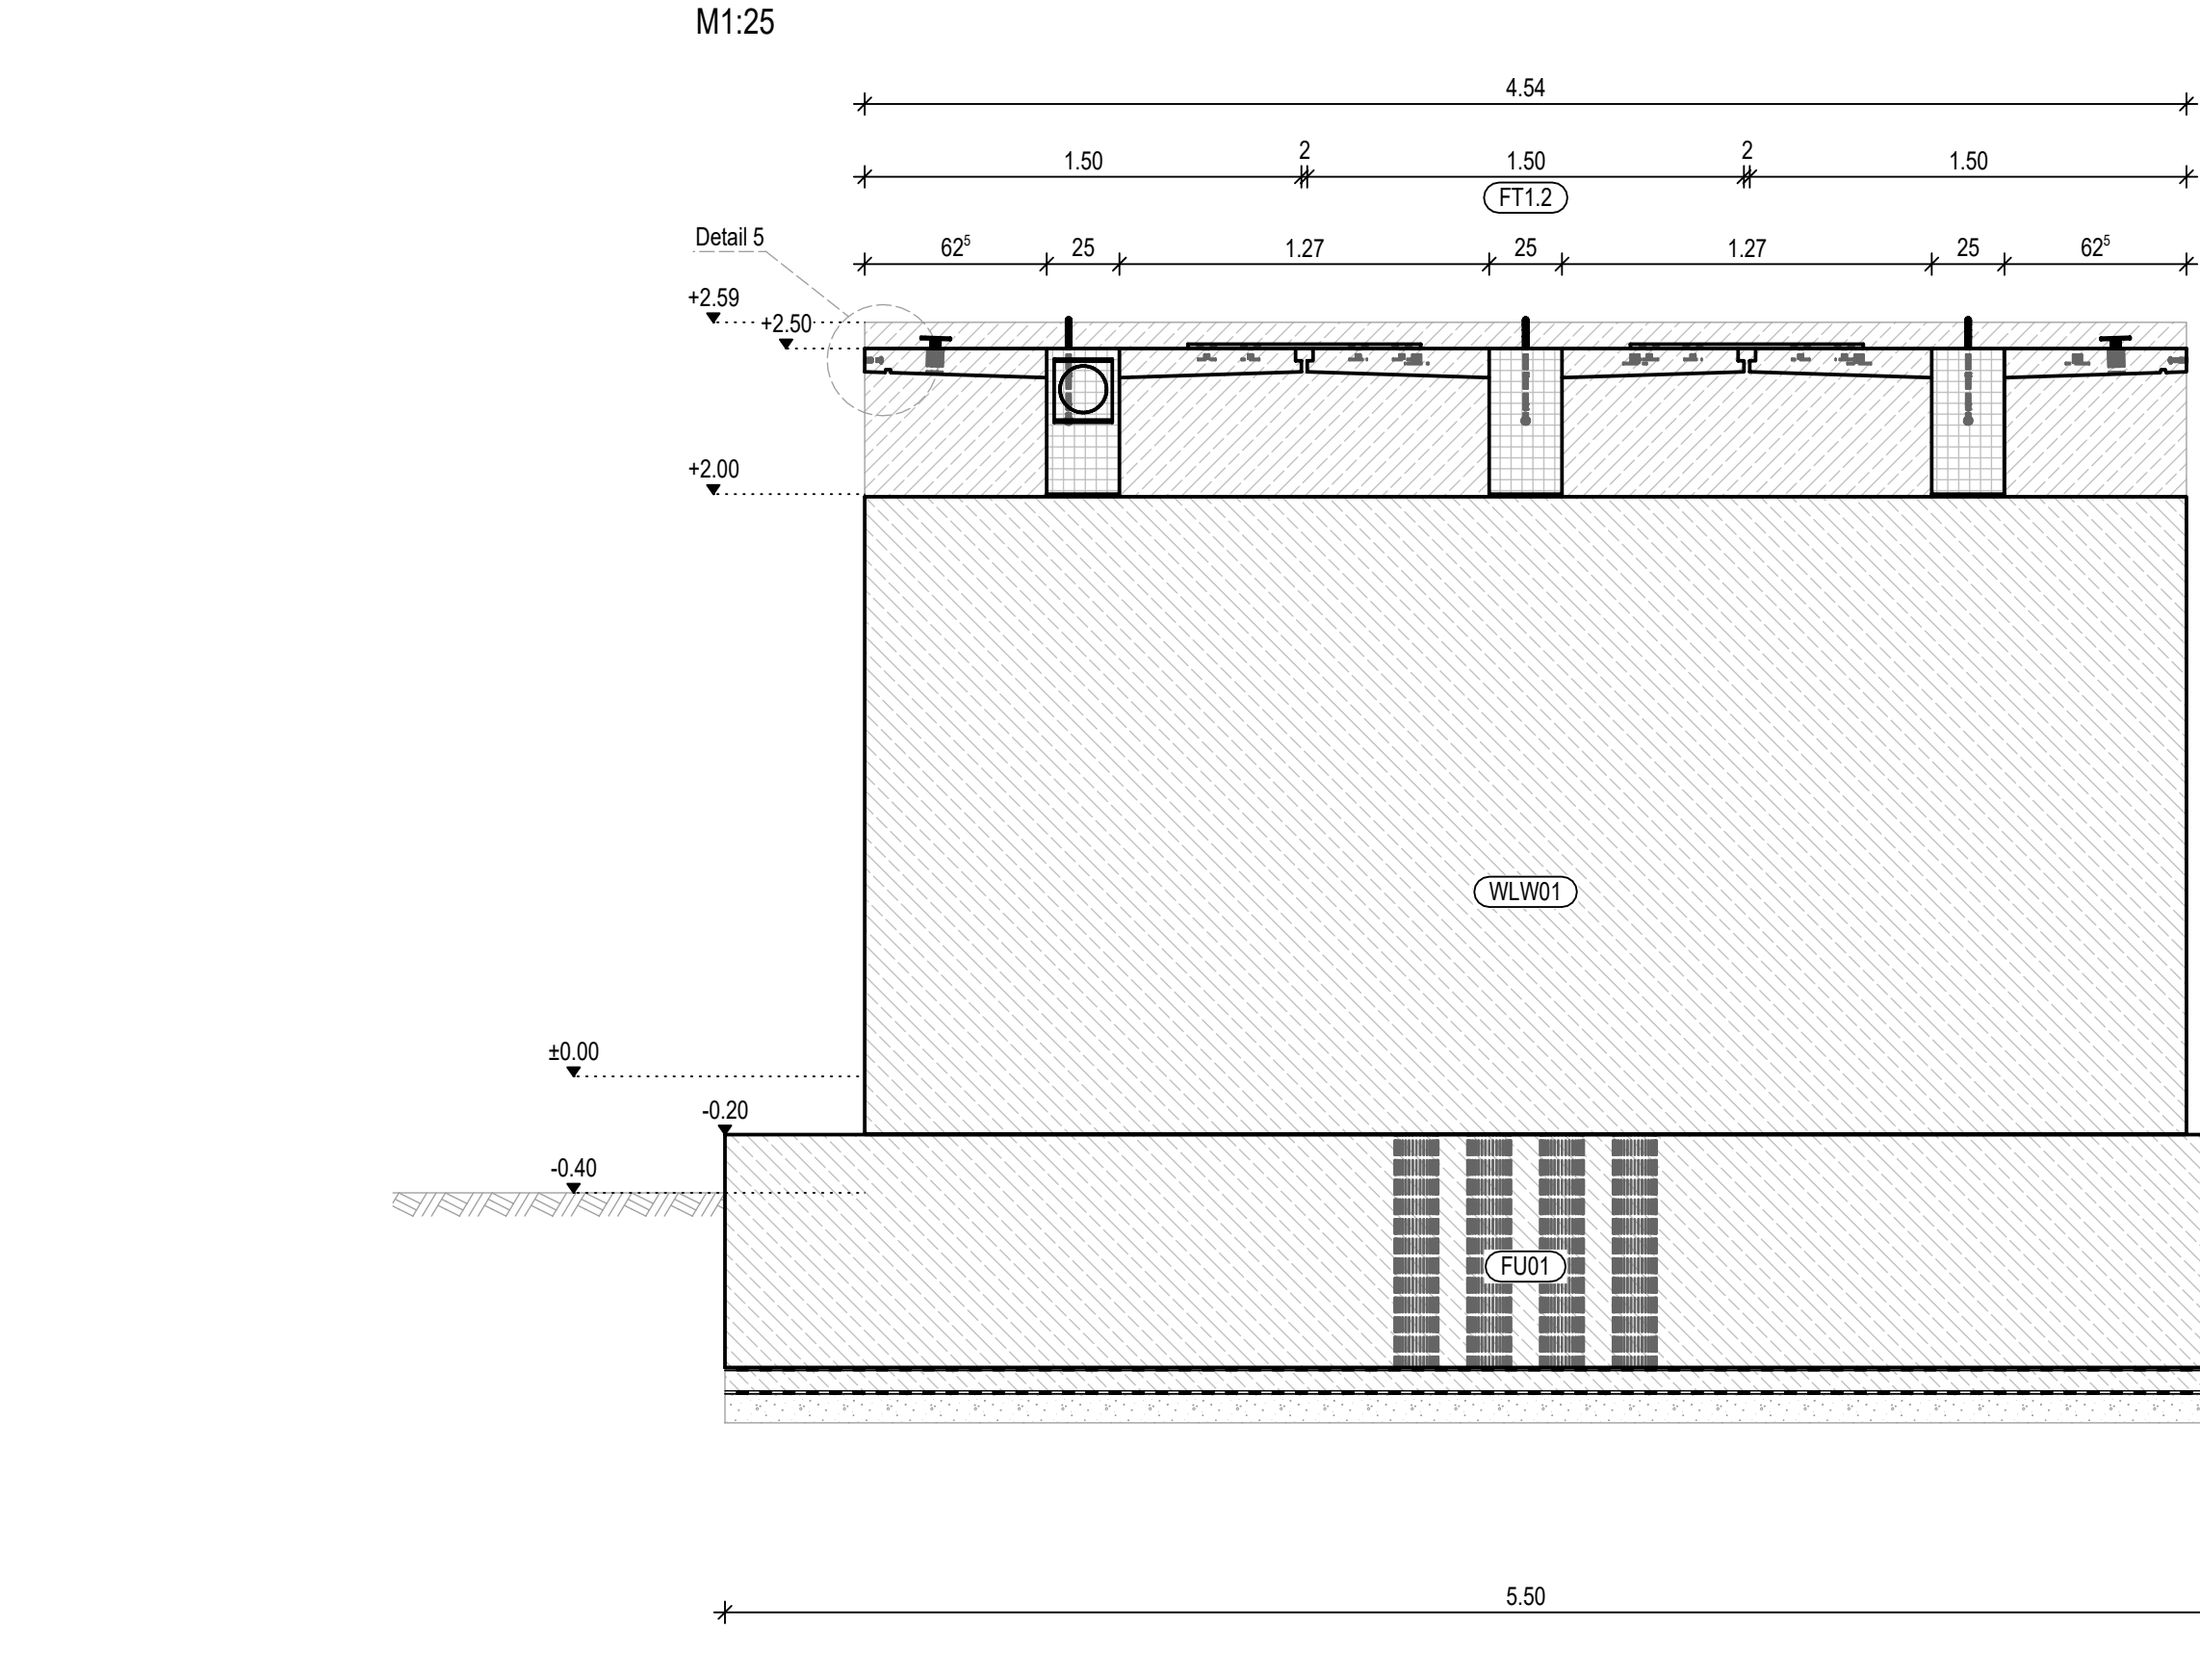


Schnitt B - B
M1:25

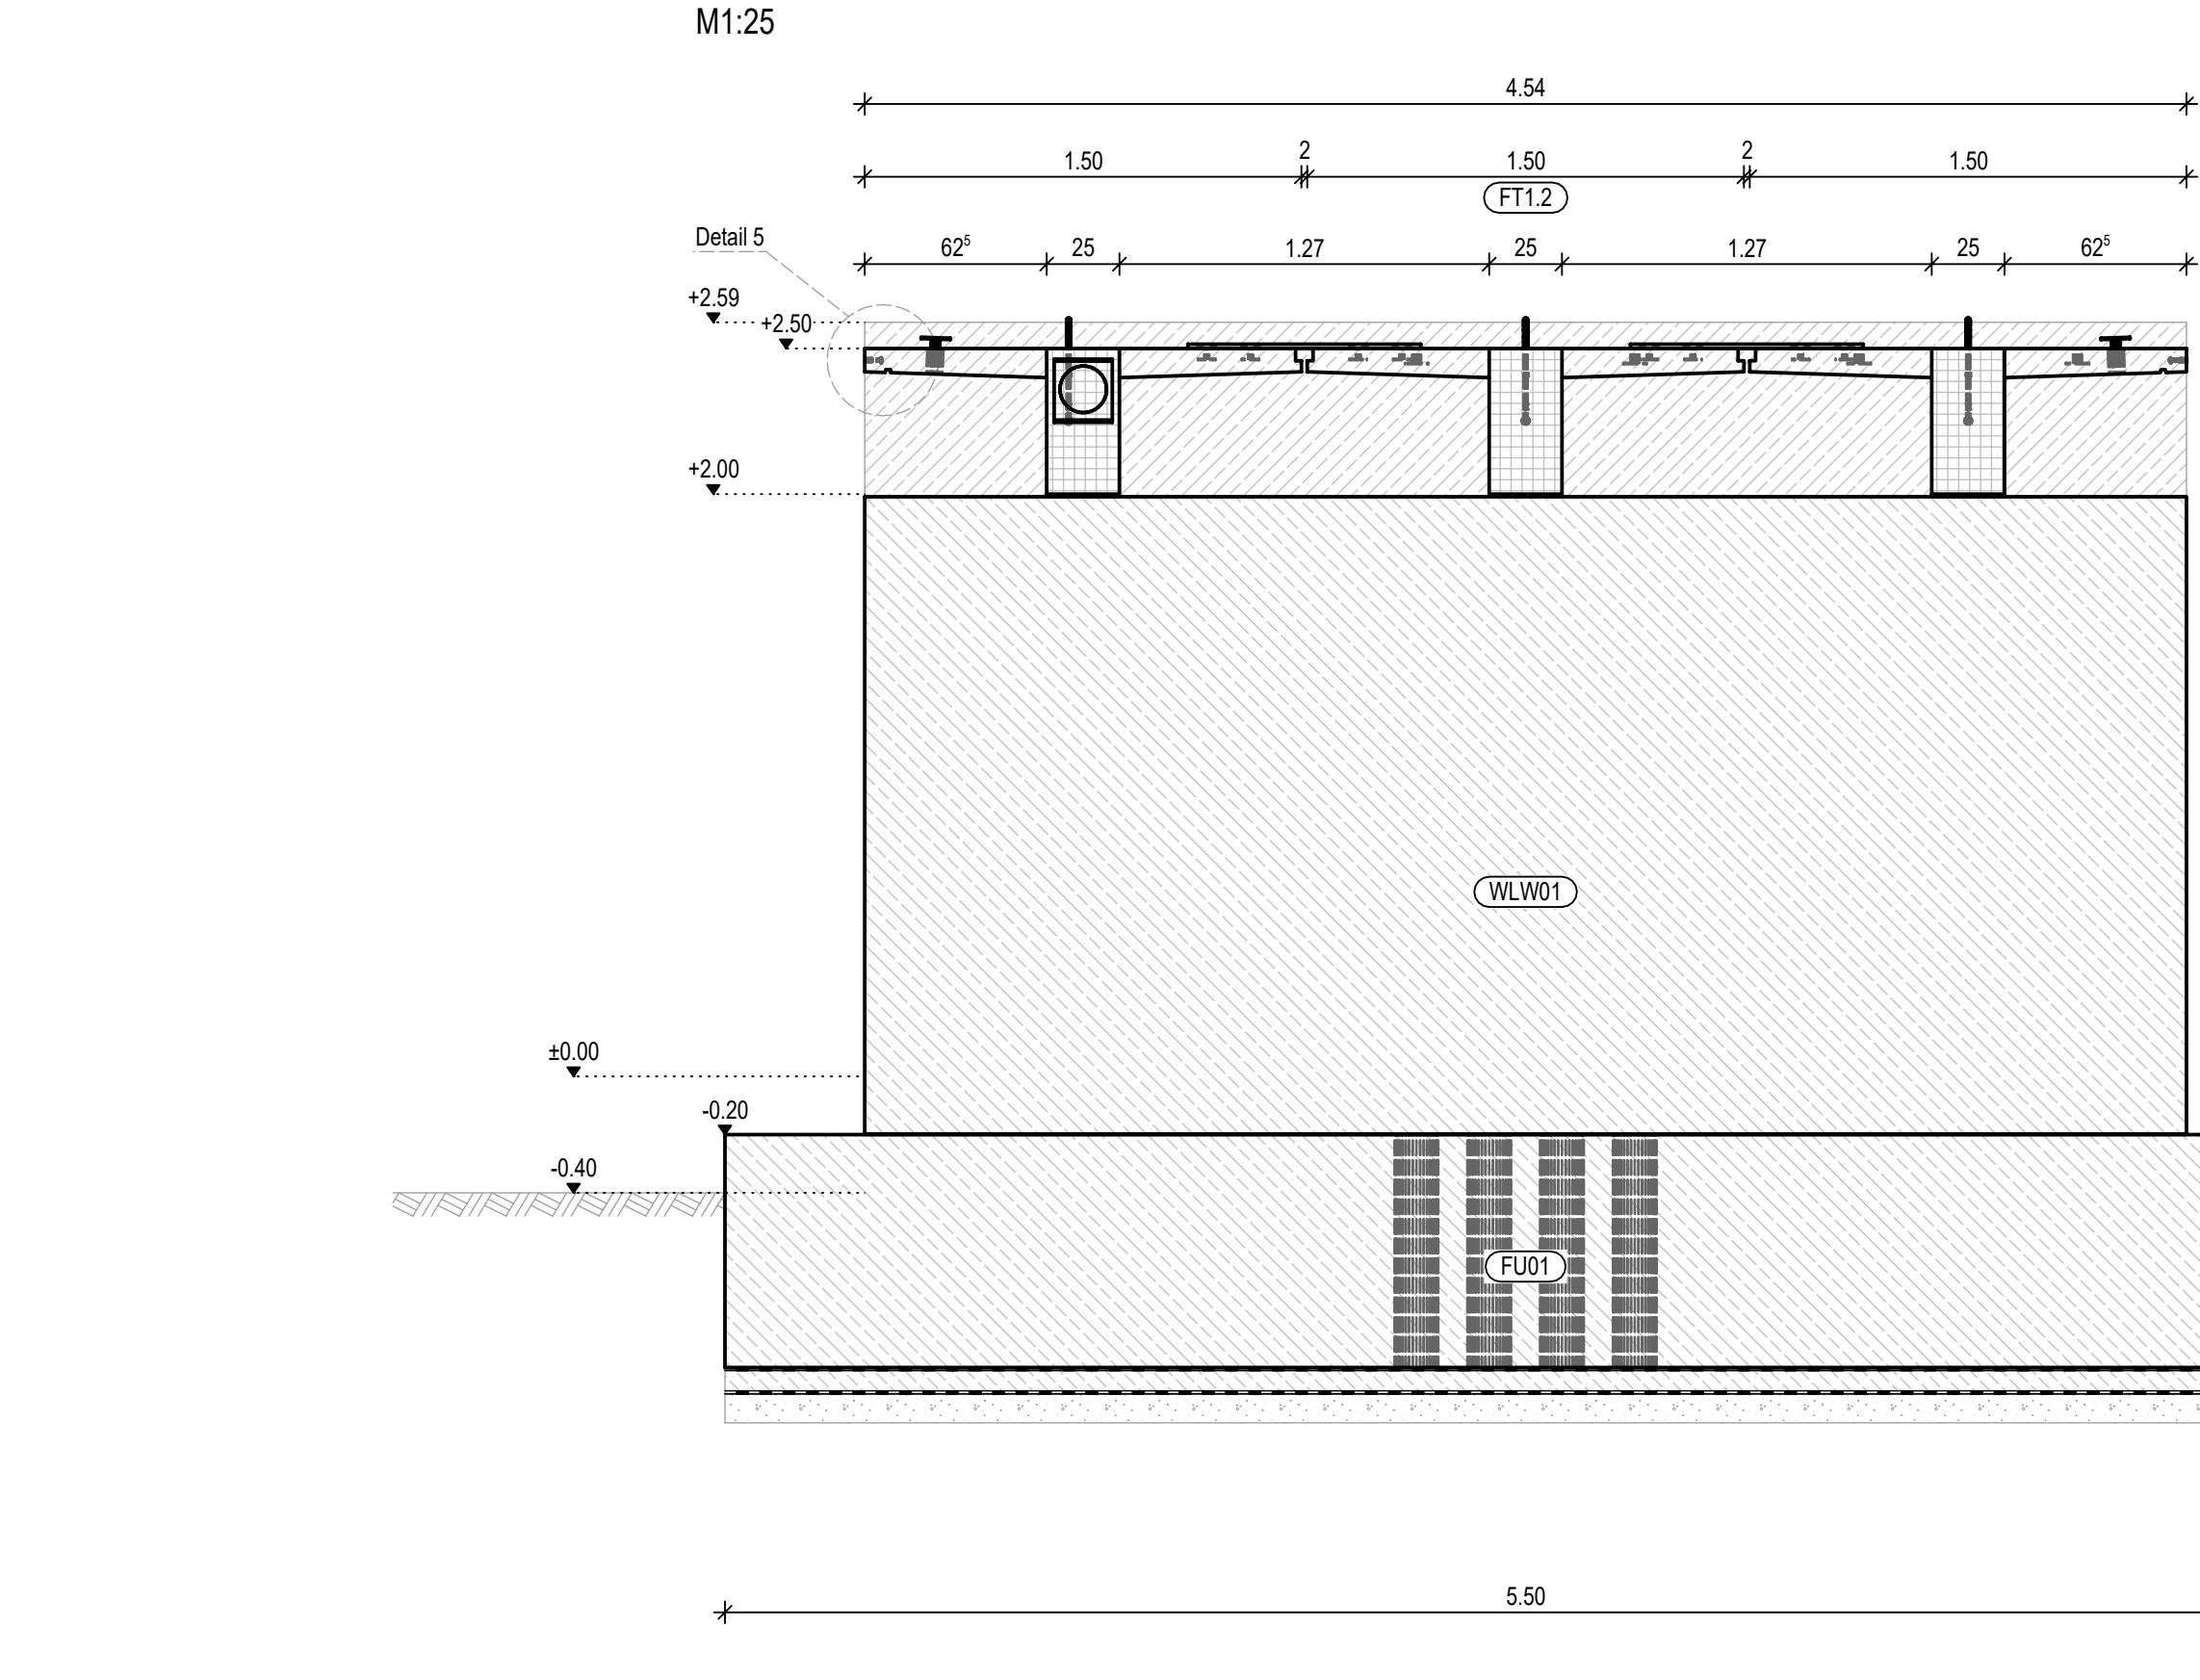


Schnitt C - C
M1:25

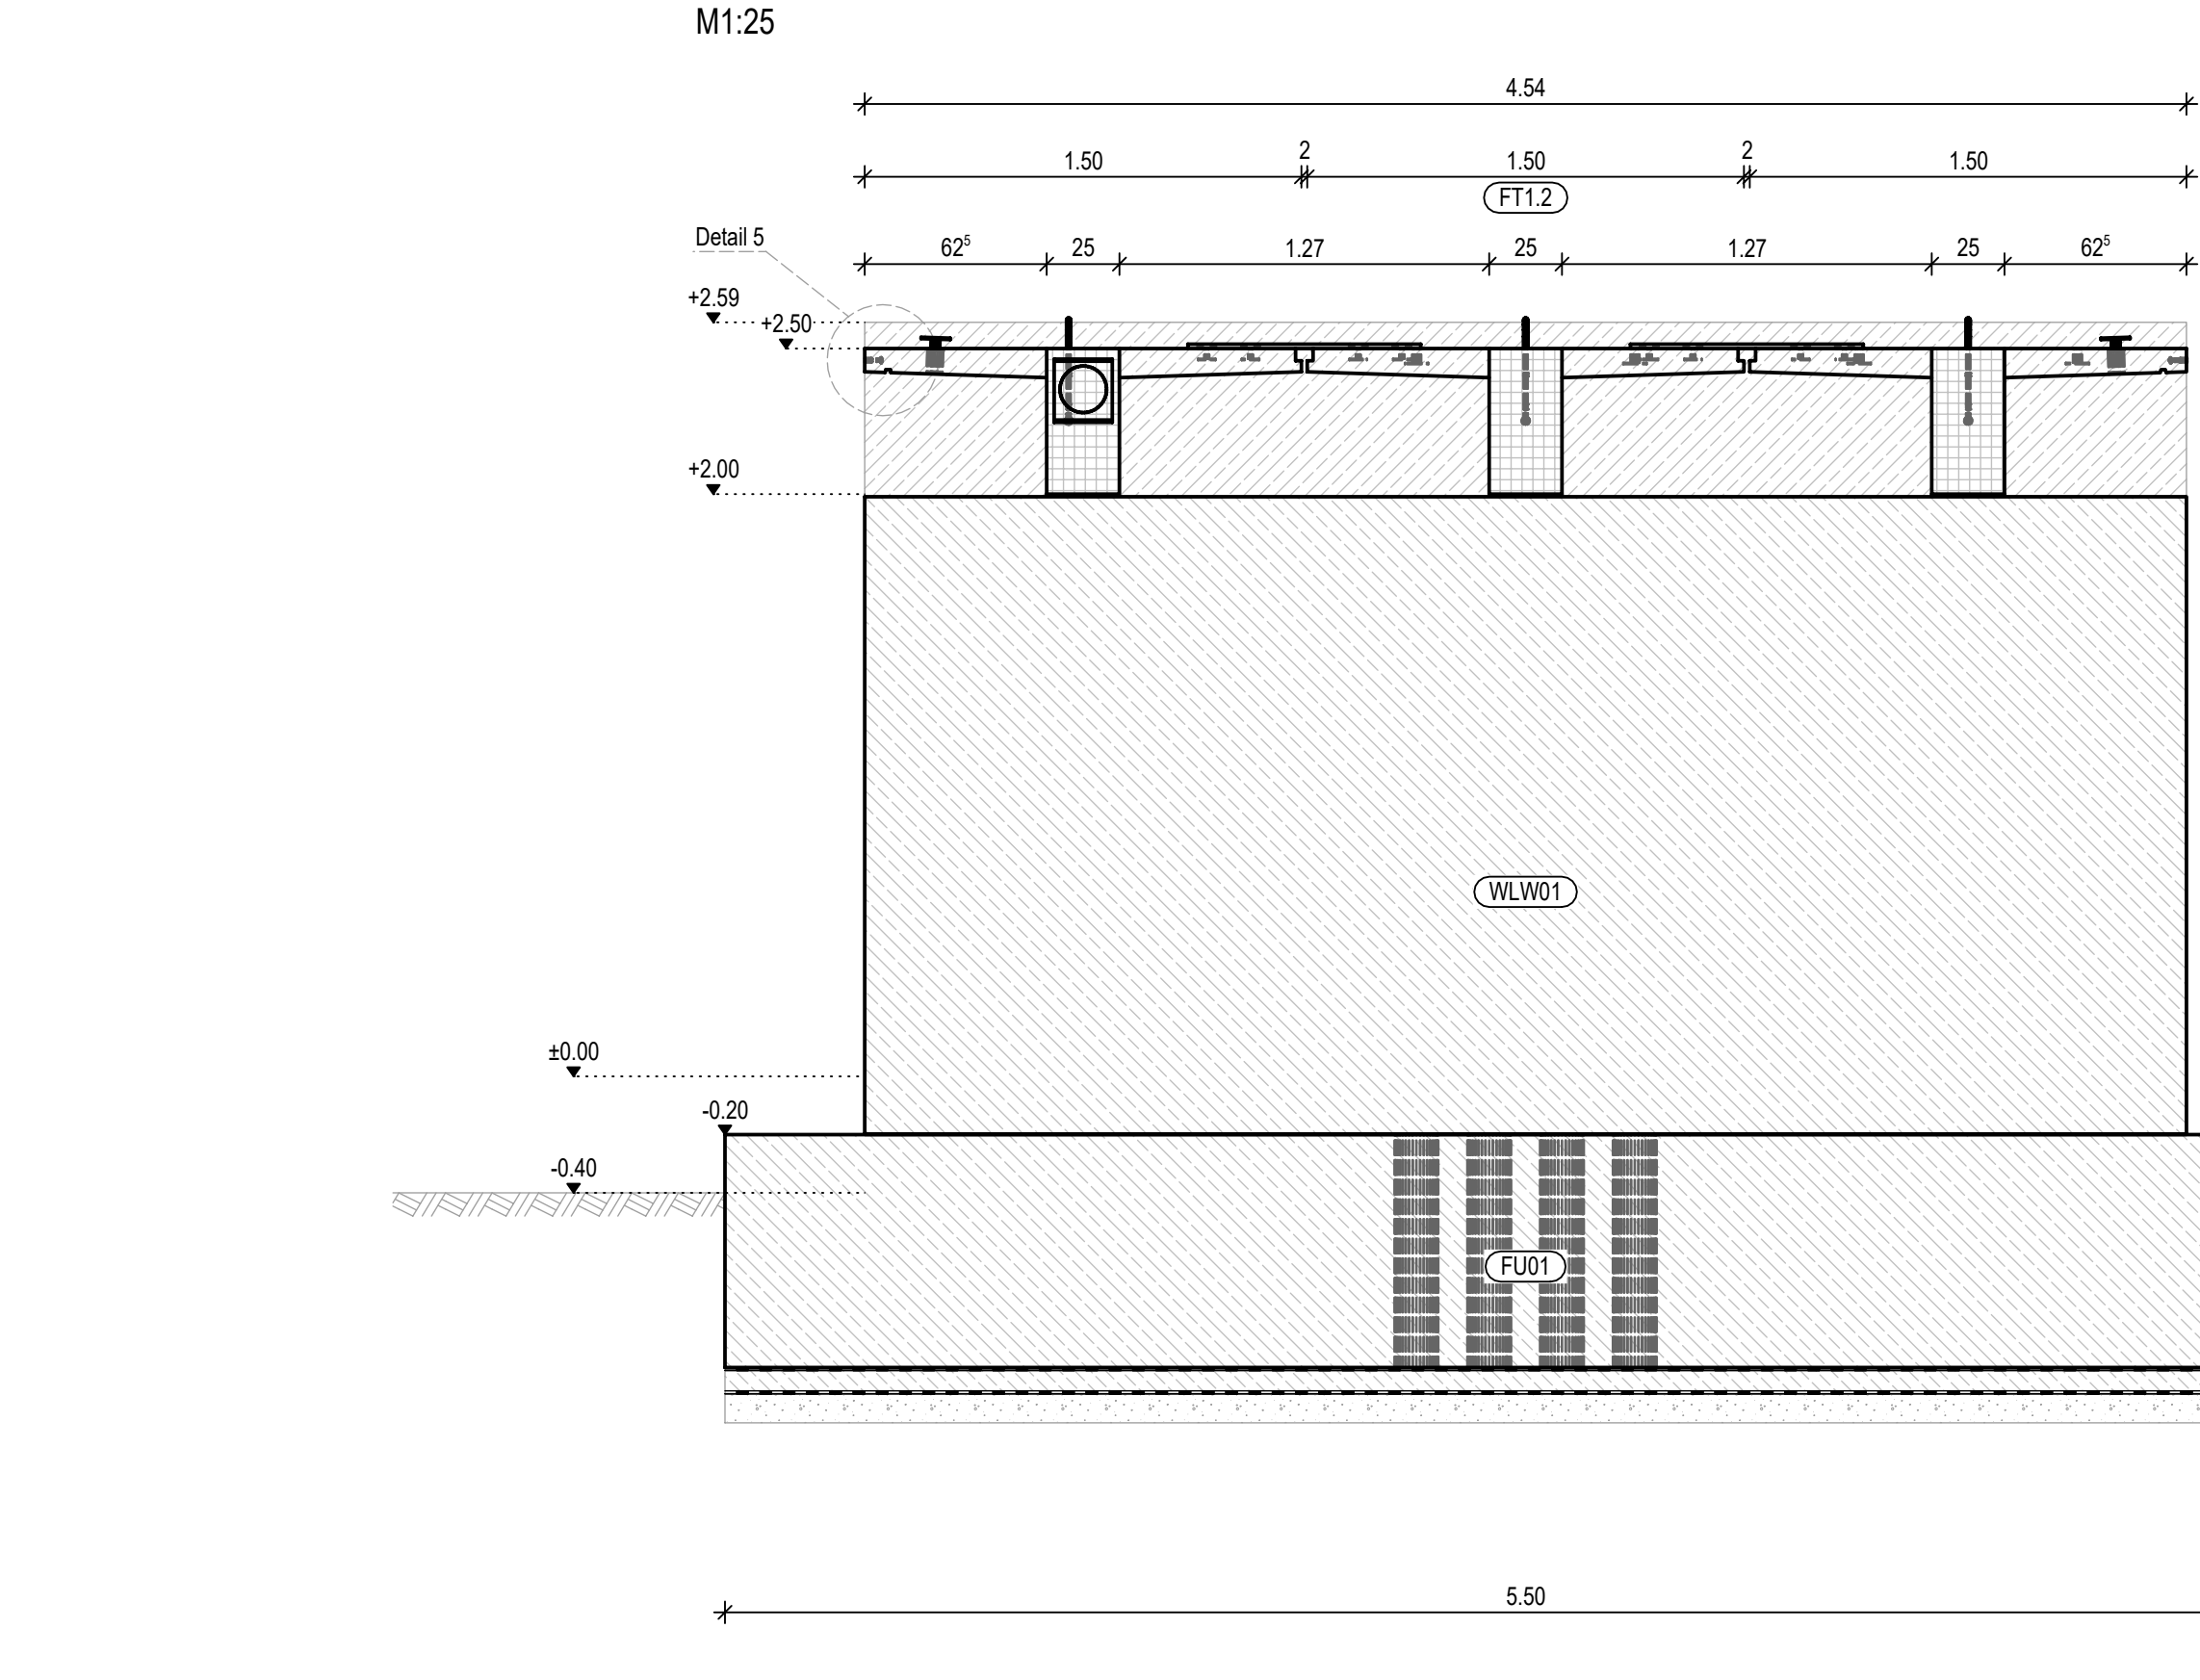


Schnitt D - D
M1:25

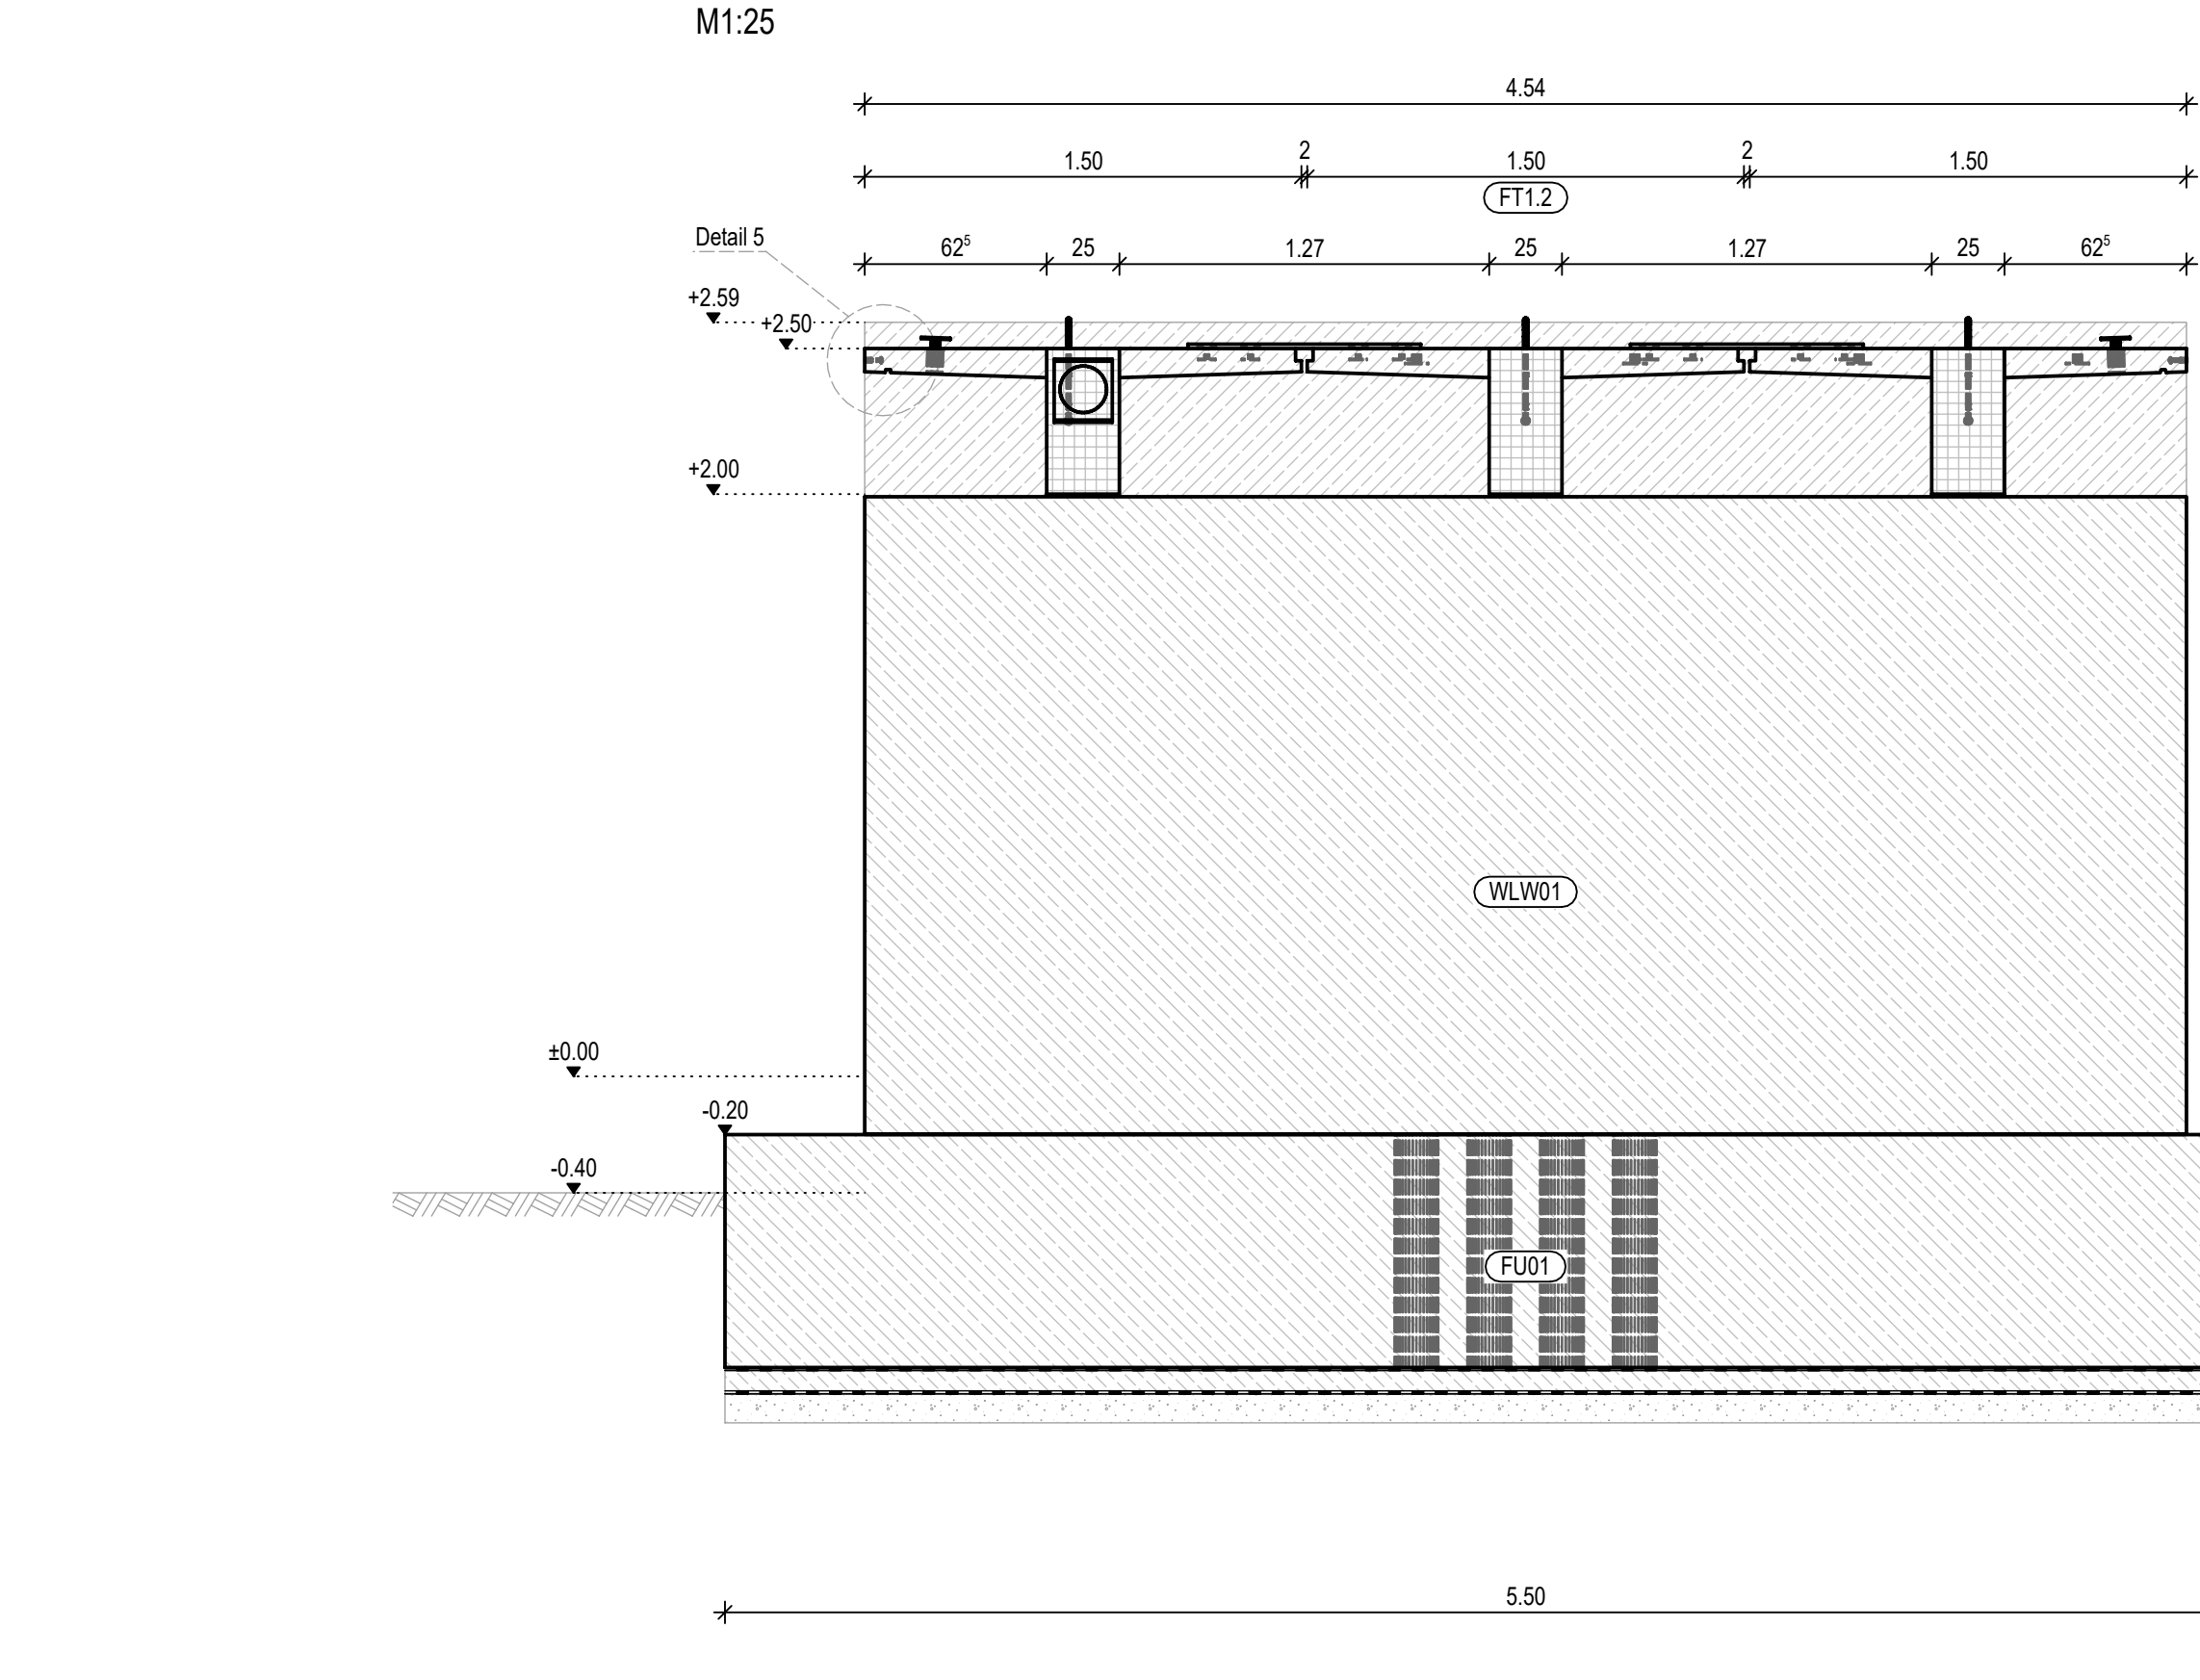


Schnitt E - E Querverbindung
M1:10

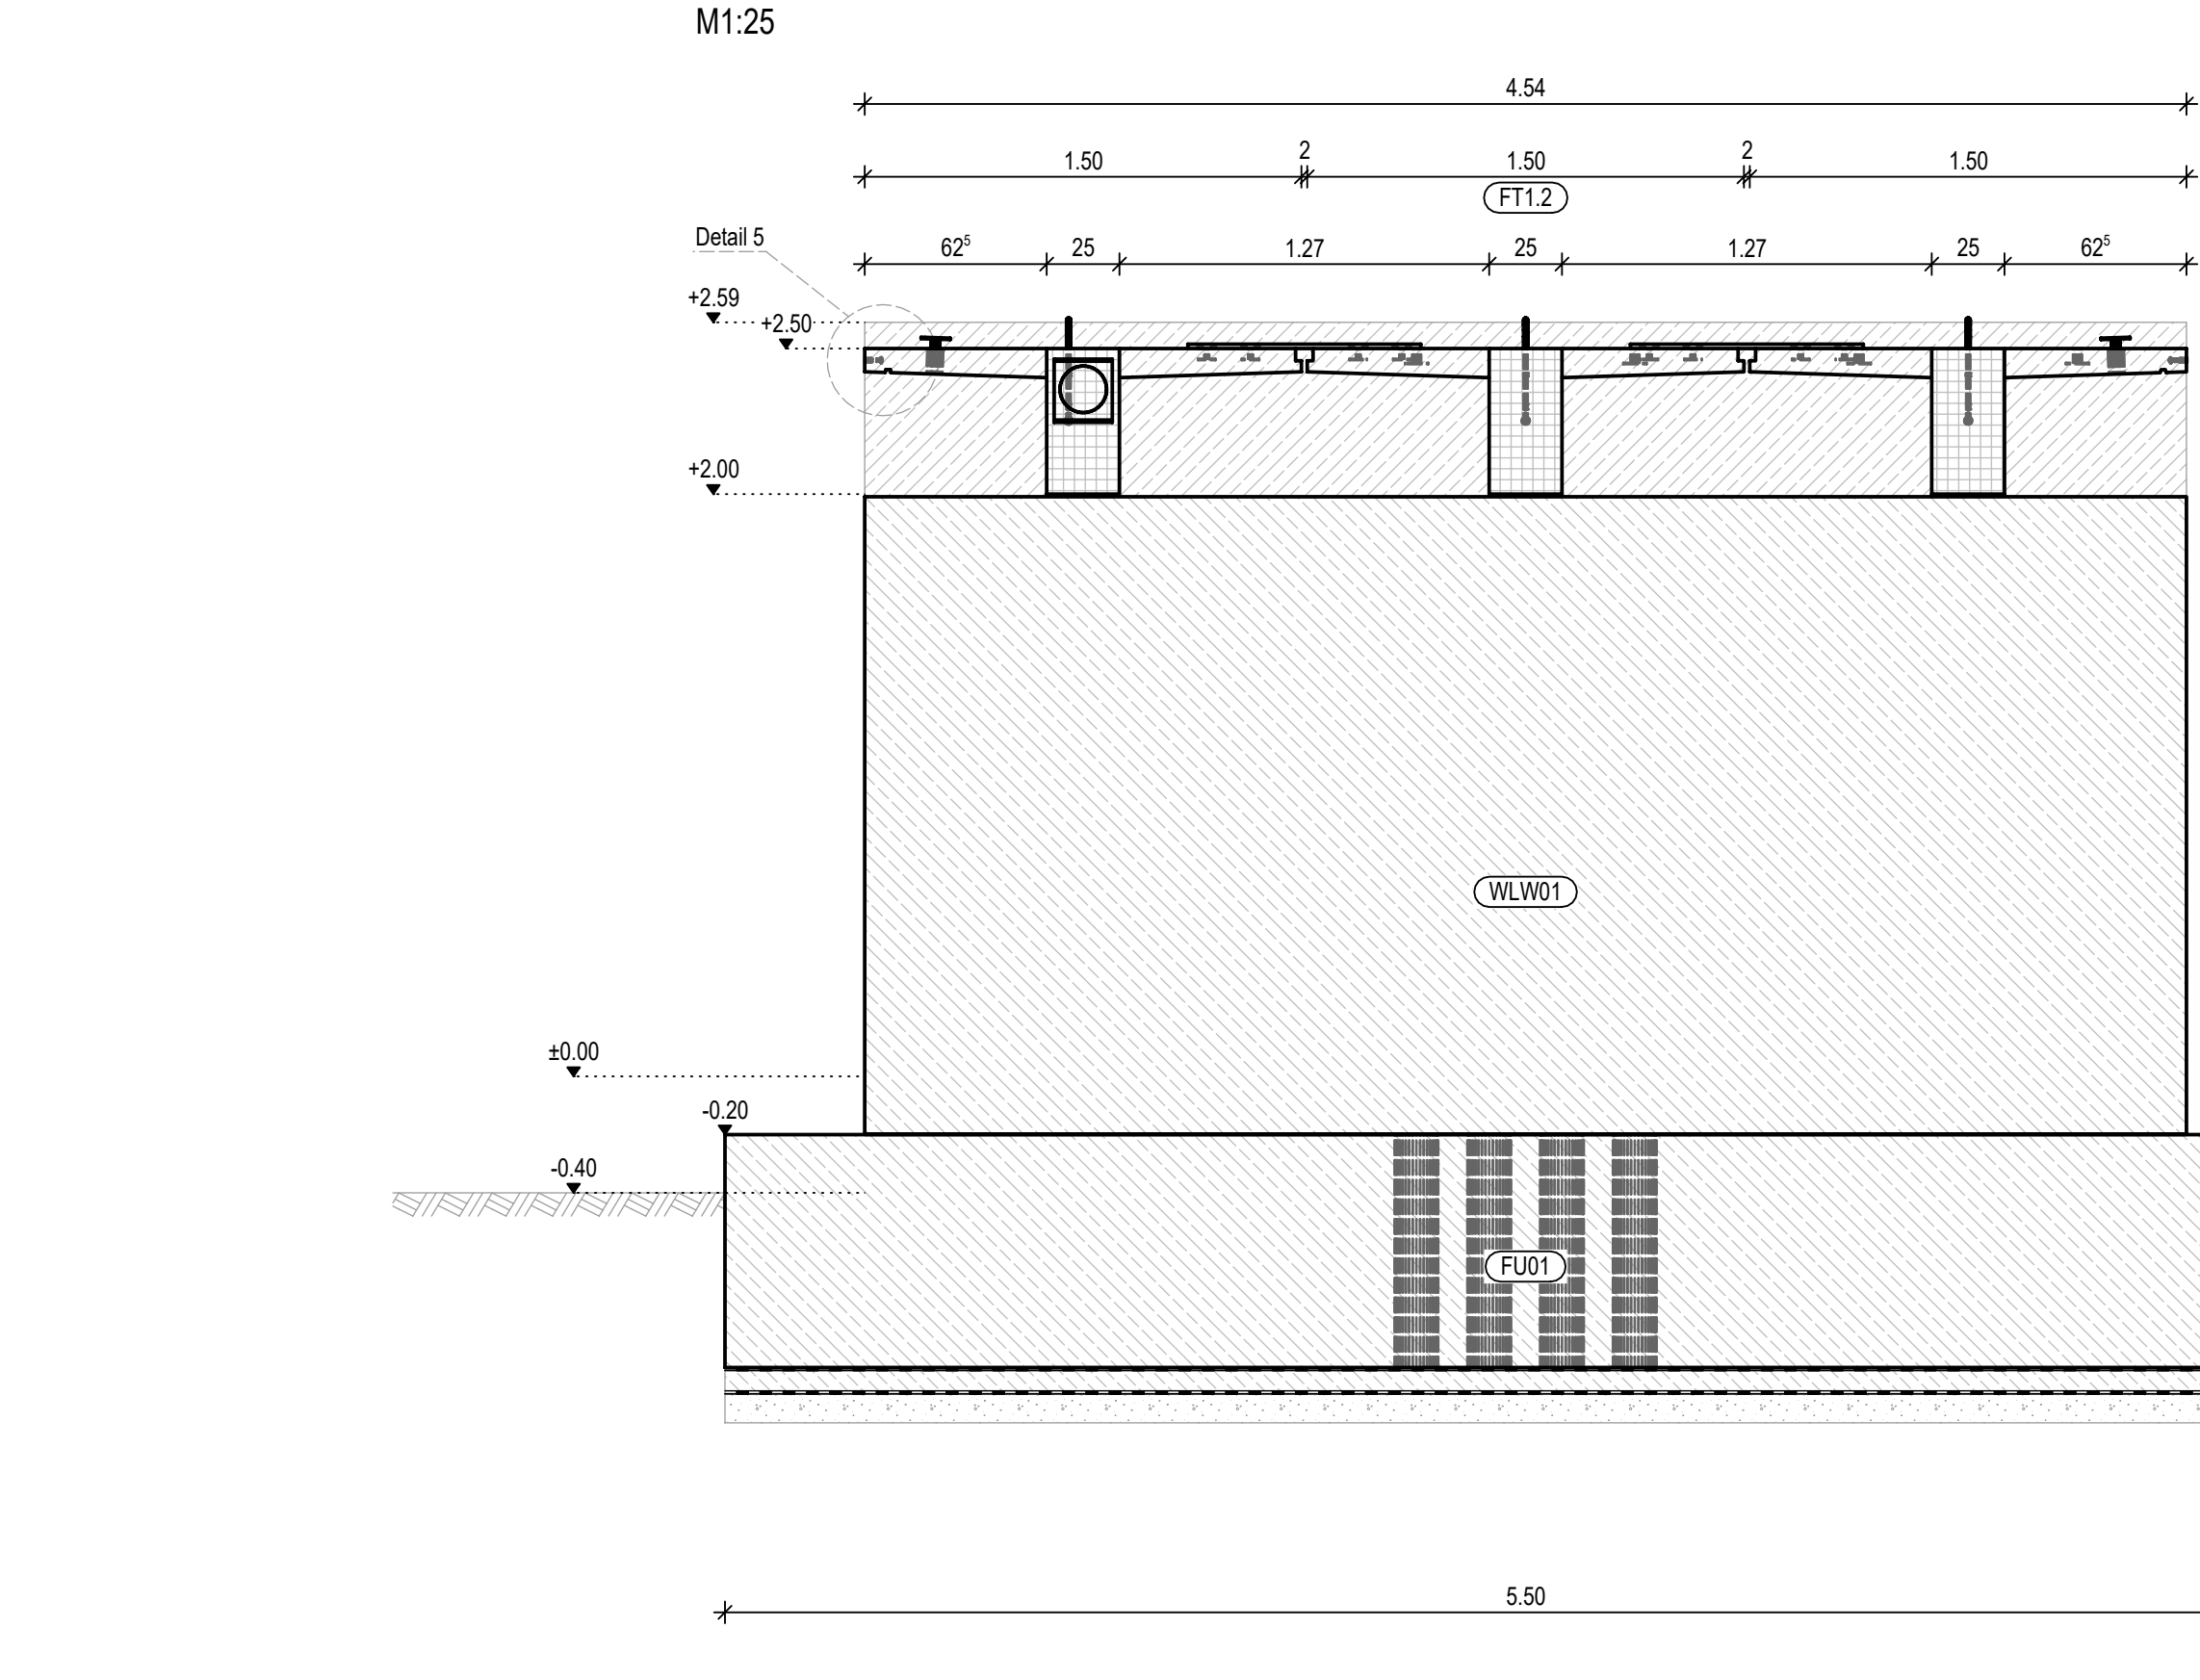


Detail 1 Anschluss an Widerlagwand
M1:10 (Schnitt mit Anschlussbewehrung)

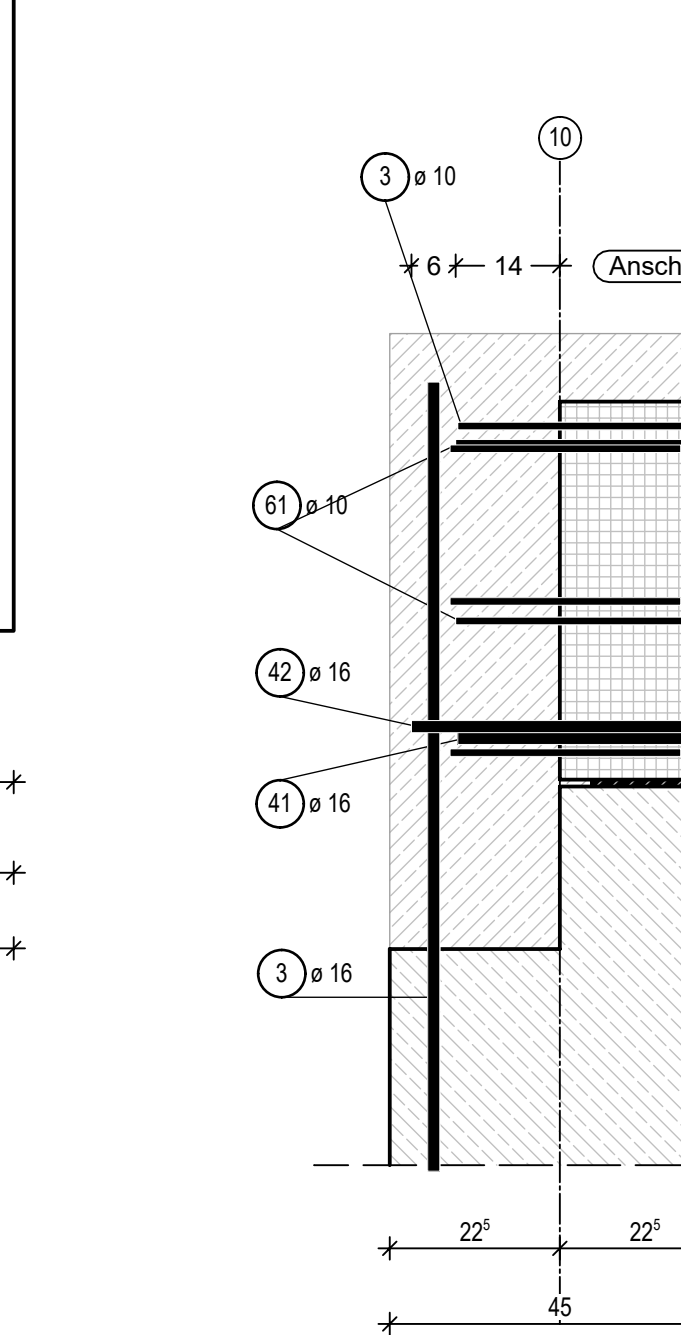


Draufsicht
(mit Anschlussbewehrung)

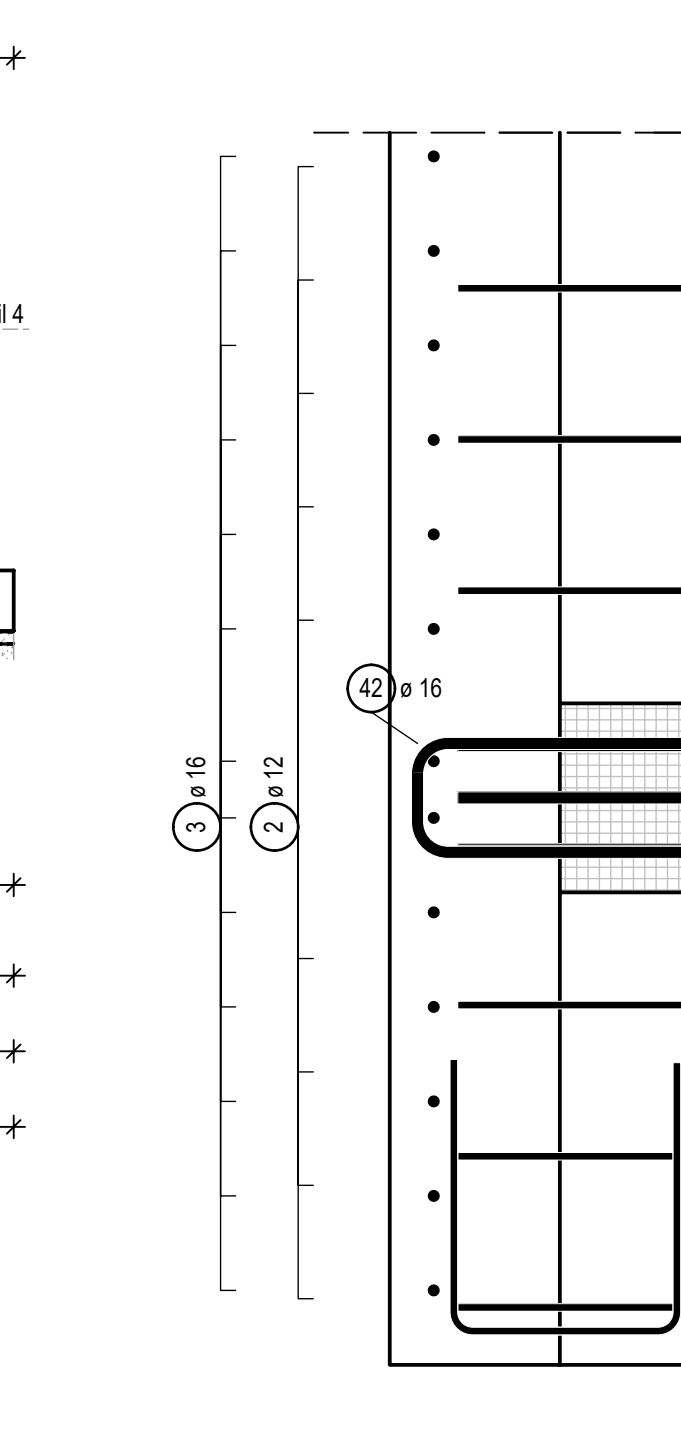


Detail 2 Stützanschluss
M1:10 (Schnitt mit Anschlussbewehrung)

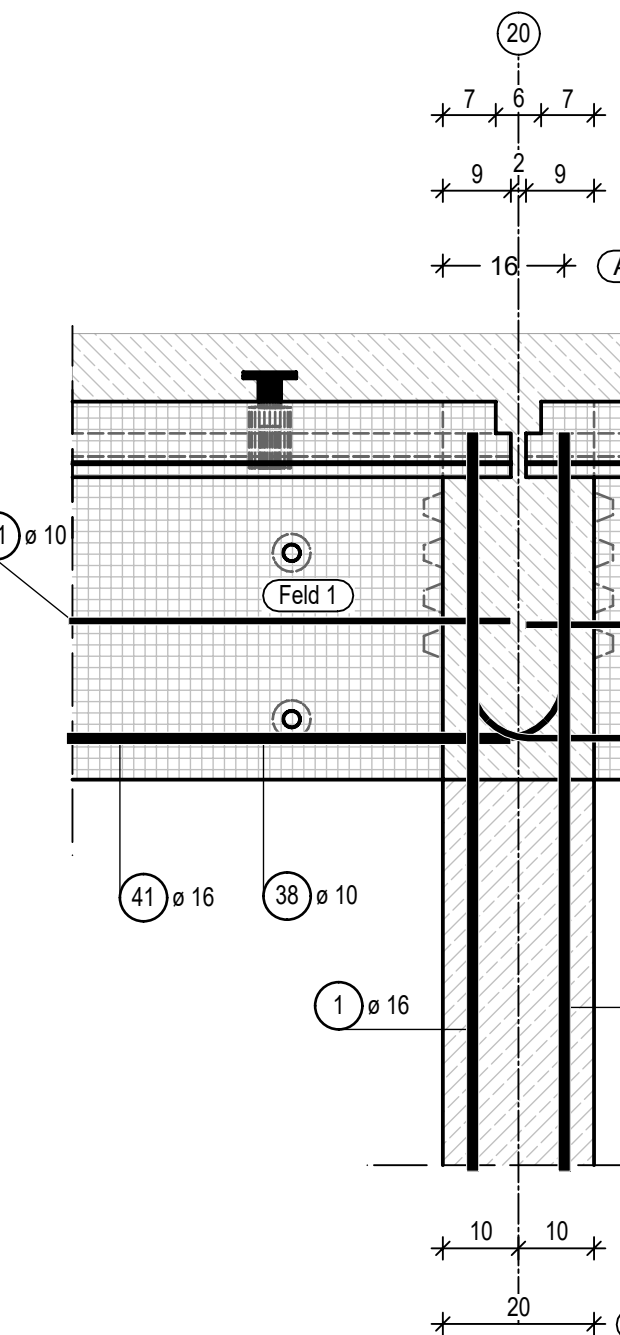

Draufsicht
(mit Anschlussbewehrung)

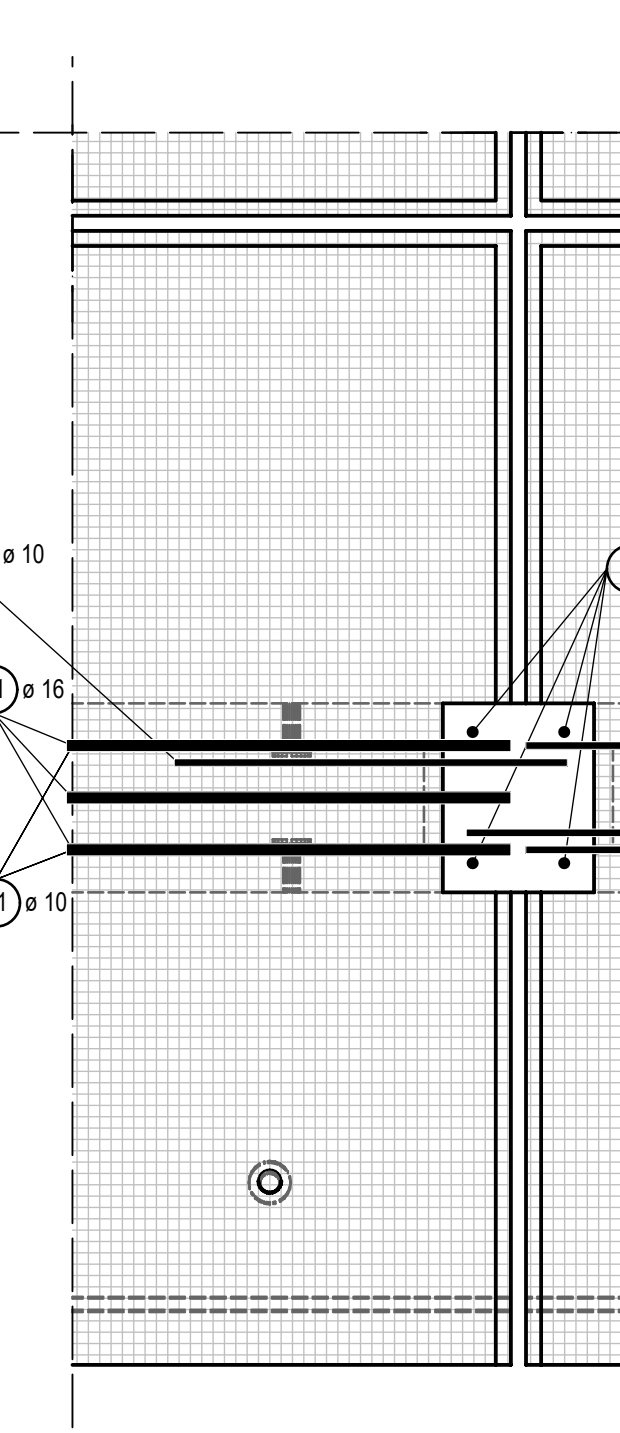


Detail 3 Anschluss Pfeiler
M1:10 (Schnitt mit Anschlussbewehrung)

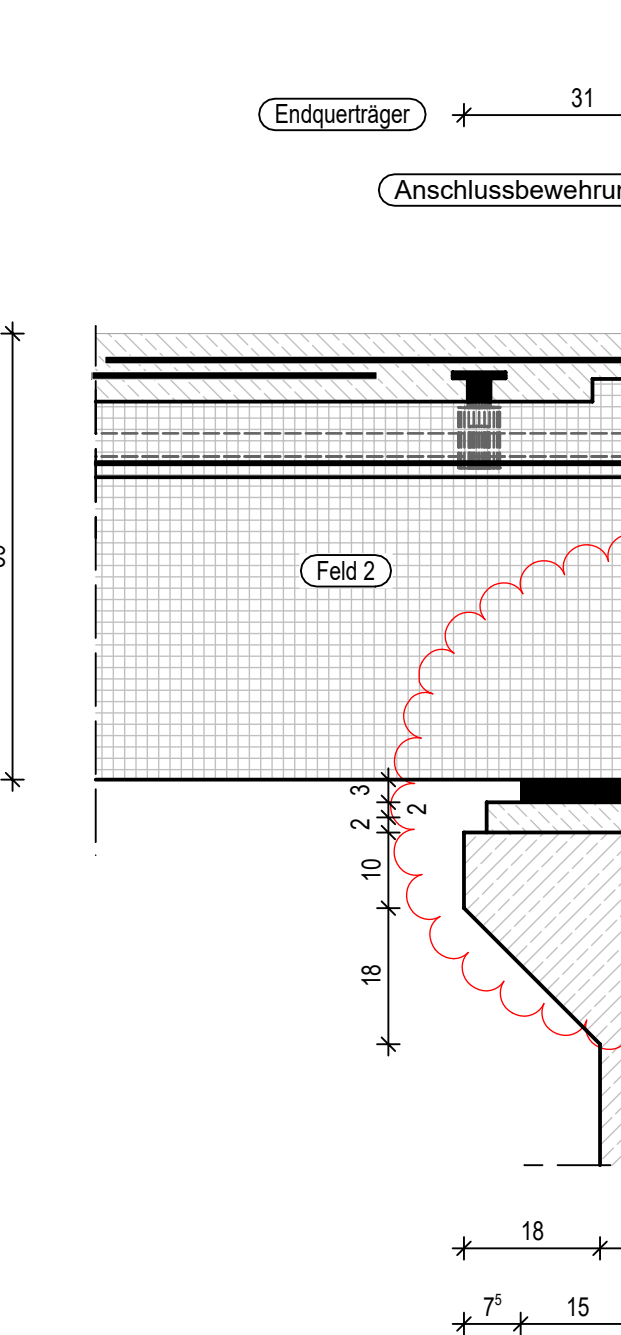


Draufsicht
(mit Anschlussbewehrung)




Detail 4 Anschluss Pfeiler
M1:10 (Schnitt mit Anschlussbewehrung)

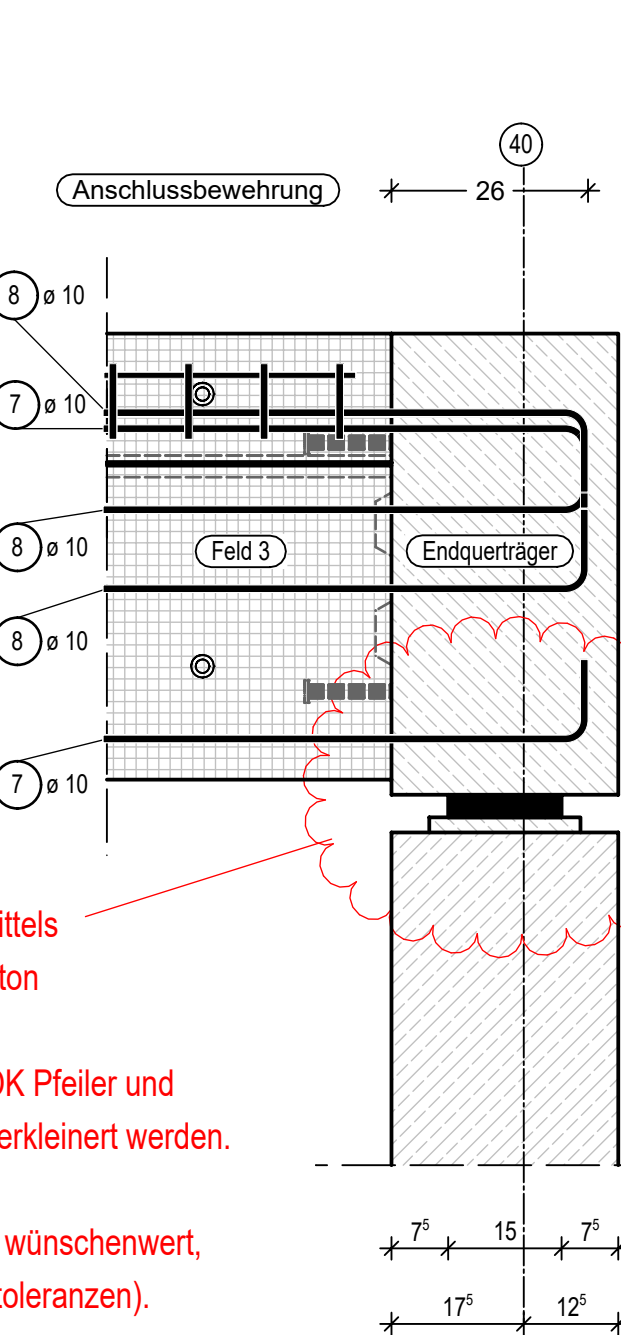

Draufsicht
(mit Anschlussbewehrung)

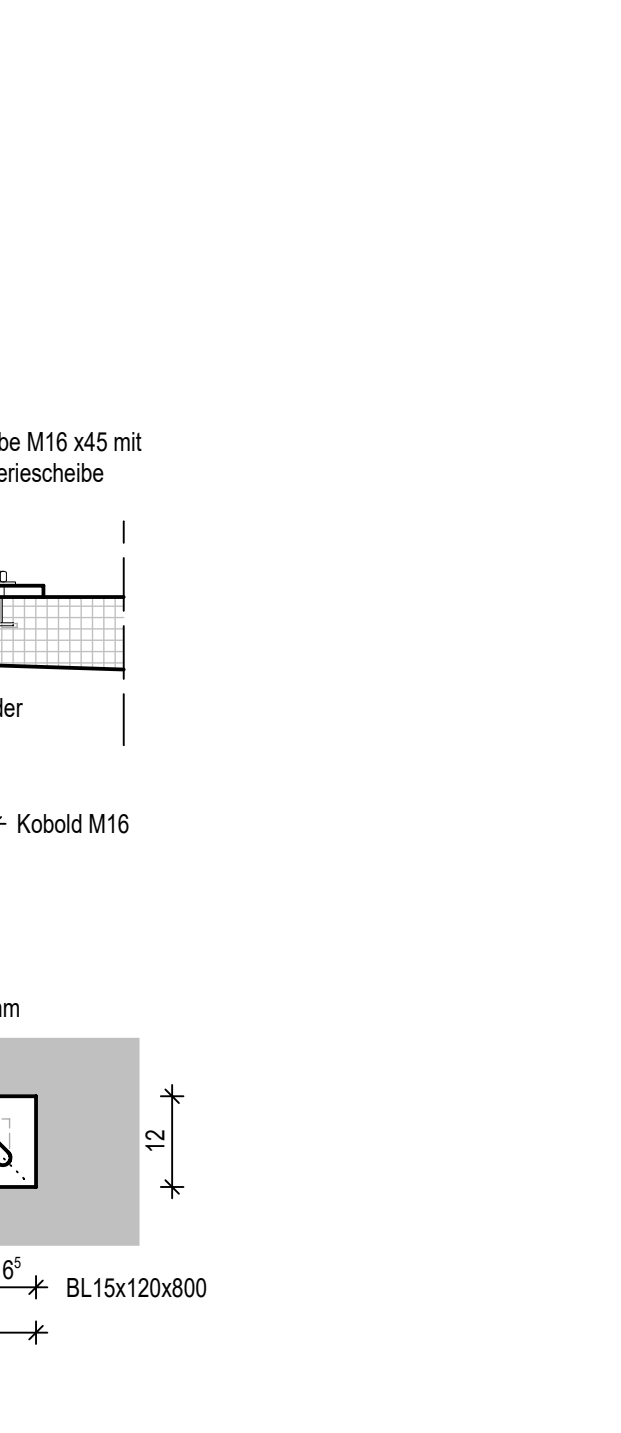

Detail 5 Koppellasse
M1:10

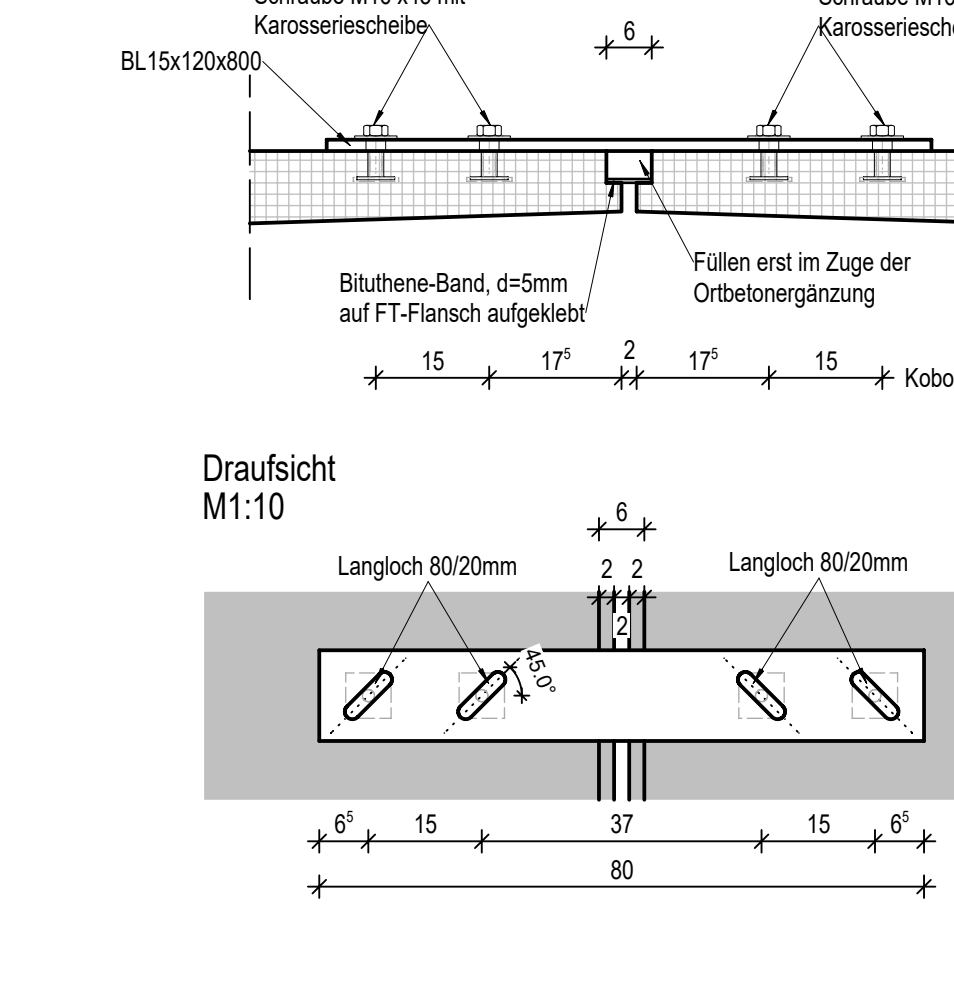

Draufsicht
M1:10

